Орион

ПРОЕКТ ИНДИВИДУАЛЬНОГО ЖИЛОГО ДОМА



Конструктивные решения.
Конструкции деревянные.

г. Великий Новгород
2026

Общие данные

Ведомость чертежей раздела КД		
Лист	Имя Макета	Примечание
1	Общие данные	
2	Силовой каркас: общие виды	
3	Схема монтажа фундамента	
4	Схема монтажа ростверка	
5	Ростверк: 3D-вид	
6	Схема монтажа цокольного перекрытия	
7	Узлы цокольного перекрытия	
8	План стен 1-го этажа	
9	Узлы каркасных стен (1)	
10	Узлы каркасных стен (2)	
11	Узлы каркасных стен (3)	
12	Узлы каркасных стен (4)	
13	Стена Ст-01	
14	Стена Ст-02	
15	Стена Ст-02: спецификация	
16	Стена Ст-03	
17	Стена Ст-04	
18	Стена Ст-04: спецификация	
19	Стена Ст-05	
20	Стена Ст-05: спецификация	
21	Стена Ст-06	
22	Стена Ст-07	
23	Стена Ст-08	
24	Стена Ст-09	
25	Стена Ст-10	
26	Стена Ст-11	
27	Стена Ст-12	
28	Стена Ст-13	
29	Стена Ст-14	
30	Стена Ст-15	
31	Стена Ст-16	
32	Стена Ст-17	


Ведомость чертежей раздела КД		
Лист	Имя Макета	Примечание
33	Стена Ст-18	
34	Обвязка стен 1-го этажа	
35	Обвязка стен: 3D-вид	
36	Балки 1-го этажа	
37	Балки 1-го этажа: сечения	
38	План чердачного перекрытия	
39	План подстропильных конструкций	
40	Стена Ст-19	
41	Стена Ст-20	
42	Стена Ст-21	
43	Стена Ст-22	
44	Стены Ст-23/24	
45	План стропильной системы	
46	Стропильная система: сечения	
47	Спецификация деревянных элементов силового каркаса	

КД Спецификация пиломатериалов силового каркаса			
Профиль	Сечение		Объем
	Высота	Ширина	
25x150			
	150	25	0,102
			0,102 м³
40x100			
	40	100	1,371
	100	40	0,003
			1,374 м³
40x150			
	40	150	5,501
	150	40	3,412
			8,913 м³
40x200			
	200	40	8,653
	250	20	0,089
			8,741 м³
45x145			
	145	45	0,279
			0,279 м³
45x195			
	195	45	0,553
			0,553 м³
			19,962 м³

1. Настоящий раздел рабочего проекта индивидуального жилого дома (участок заказчика) разработан на основании архитектурной части, СП 64.13330.2017 "Деревянные конструкции", СП 20.13330.2016 "Нагрузки и воздействия".
2. Для обеспечения заданных уклонов кровли (см. лист "План кровли" раздела АР) все отметки и длины позиций, указанные на чертежах до монтажа в проектное положение уточнить по месту.
3. Материал конструкций – древесина хвойных пород I сорта с влажностью не более 30%.
4. Выполнить огнезащитную обработку древесины и защиту ее от гниения путём глубокой пропитки антисептиком.
5. Примыкание деревянных элементов силового каркаса друг к другу по периметру теплого контура уплотняется джутовым полотном/ монтажной пеной/политермом.
6. Опоры и балки террасы, а также матица 1-го этажа выполняются из пакета строганых досок, окрашенных на производстве.

						КД			
						#Полный Адрес Участка			
Изм.	Кол.	Лист	№ док.	Подп.	Дата				
						Индивидуальный жилой дом	Стадия	Лист	Листов
							П	1	48
Разработал					03/2026				
Проверил					03/2026	Общие данные	КАРКАСНИК		
Утвердил					03/2026				


Силовой каркас: общие виды

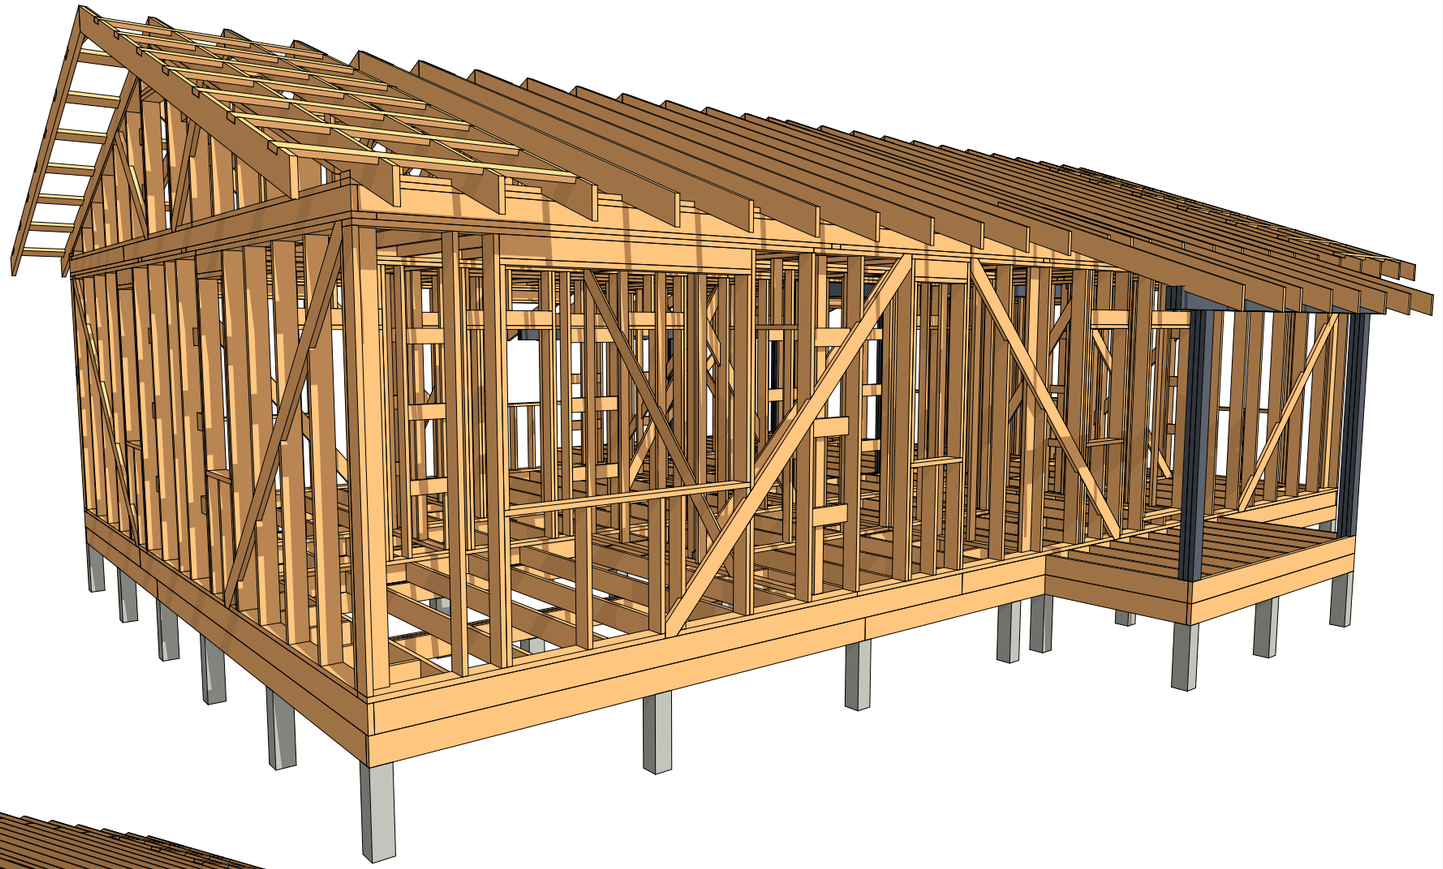




1				03/2026	Силовой каркас: общие виды	Лист 2
Изм.	Лист	№ докум.	Подпись	Дата		

Схема монтажа фундамента

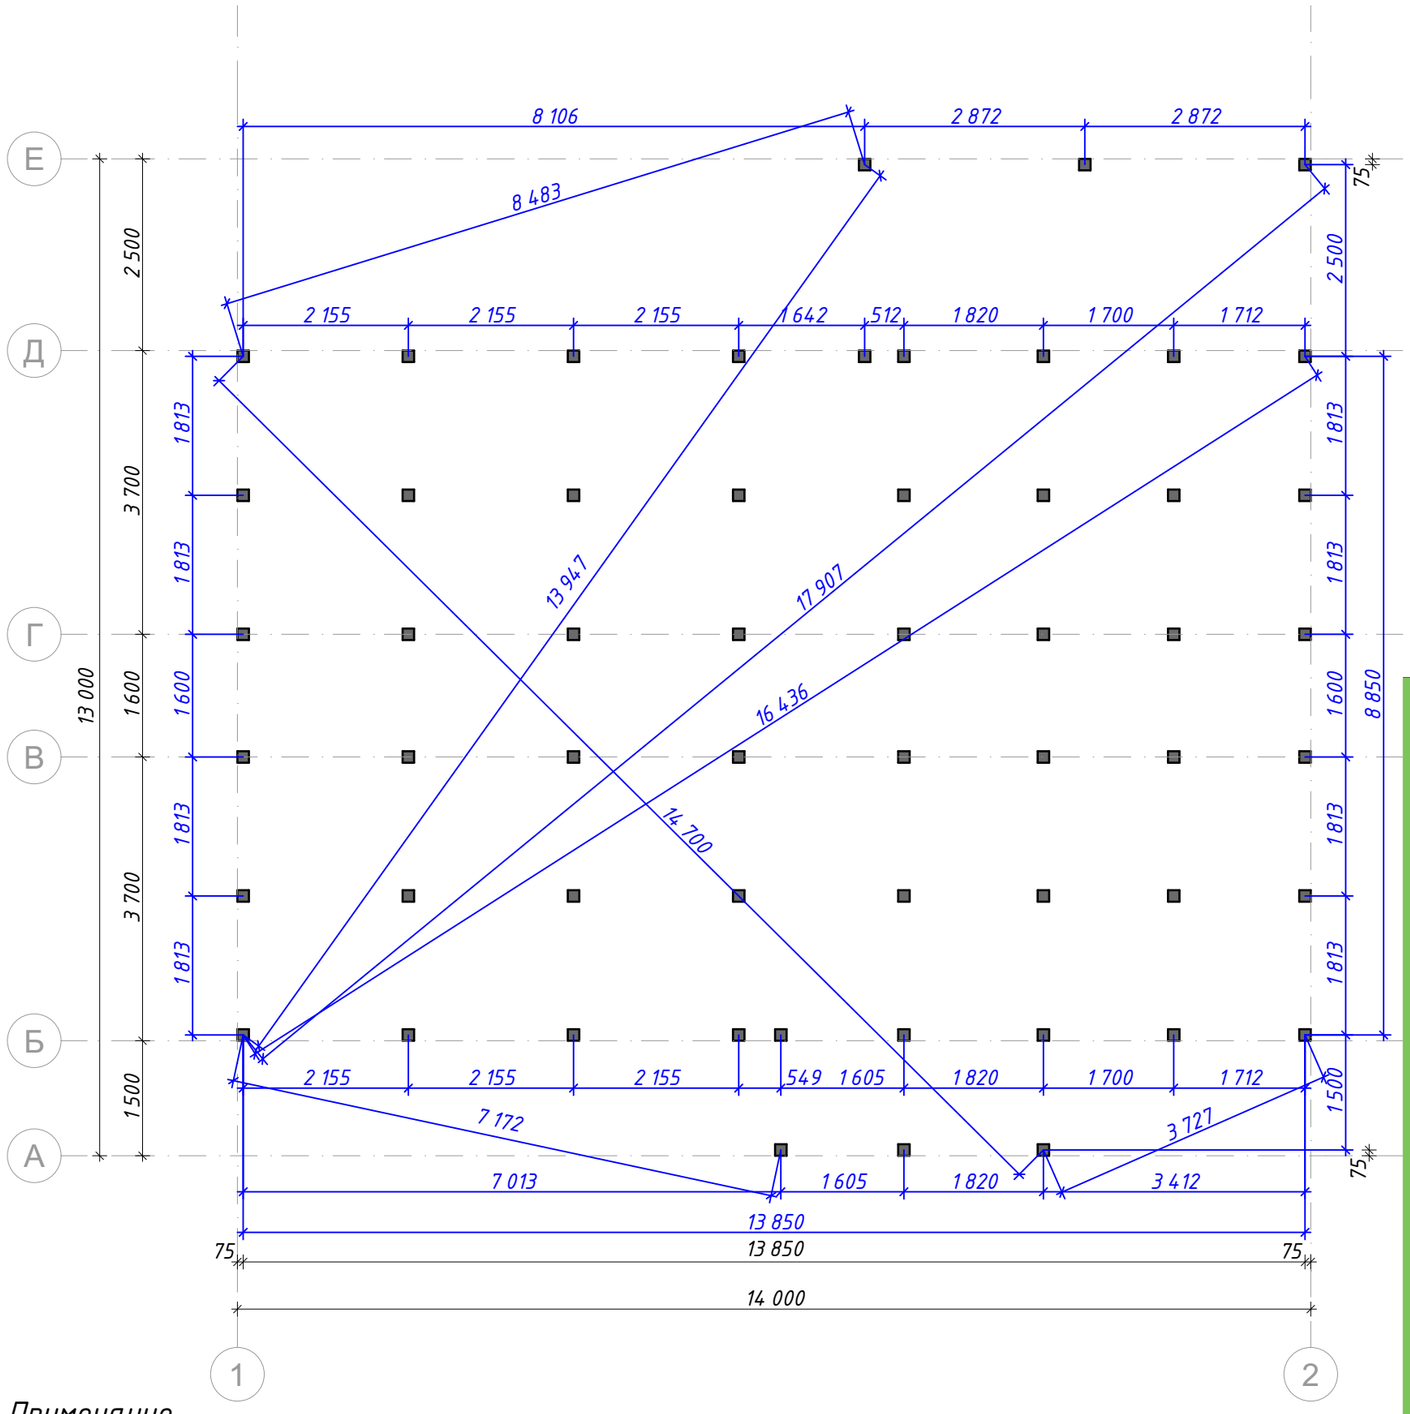

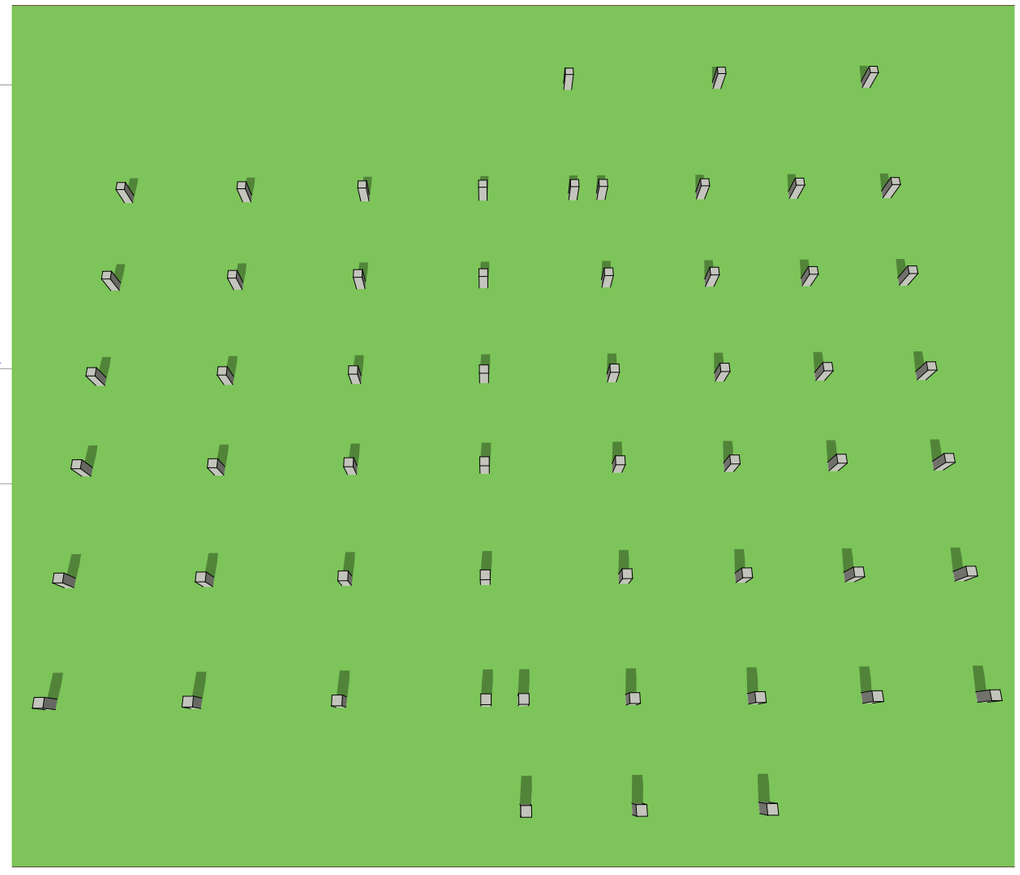

Спецификация ж/б свай					
Марка	Наим.	Длина сечения	Ширина сечения	Длина сваи	Кол-во
ЖБ-1	ЖБ Свая	150	150	3 000	56
					56


Примечание.

1. В разделе КР настоящего проекта приведен предварительный план свайного фундамента и обвязки свай. Точные характеристики фундамента определить на основании данных исследования грунта до начала монтажных работ.

2. Синими размерными линиями на плане обозначены расстояния между центрами свай.

Изм.	Лист	№ докум.	Подпись	Дата	Схема монтажа фундамента	Лист
1				03/2026		3

Схема монтажа ростверка

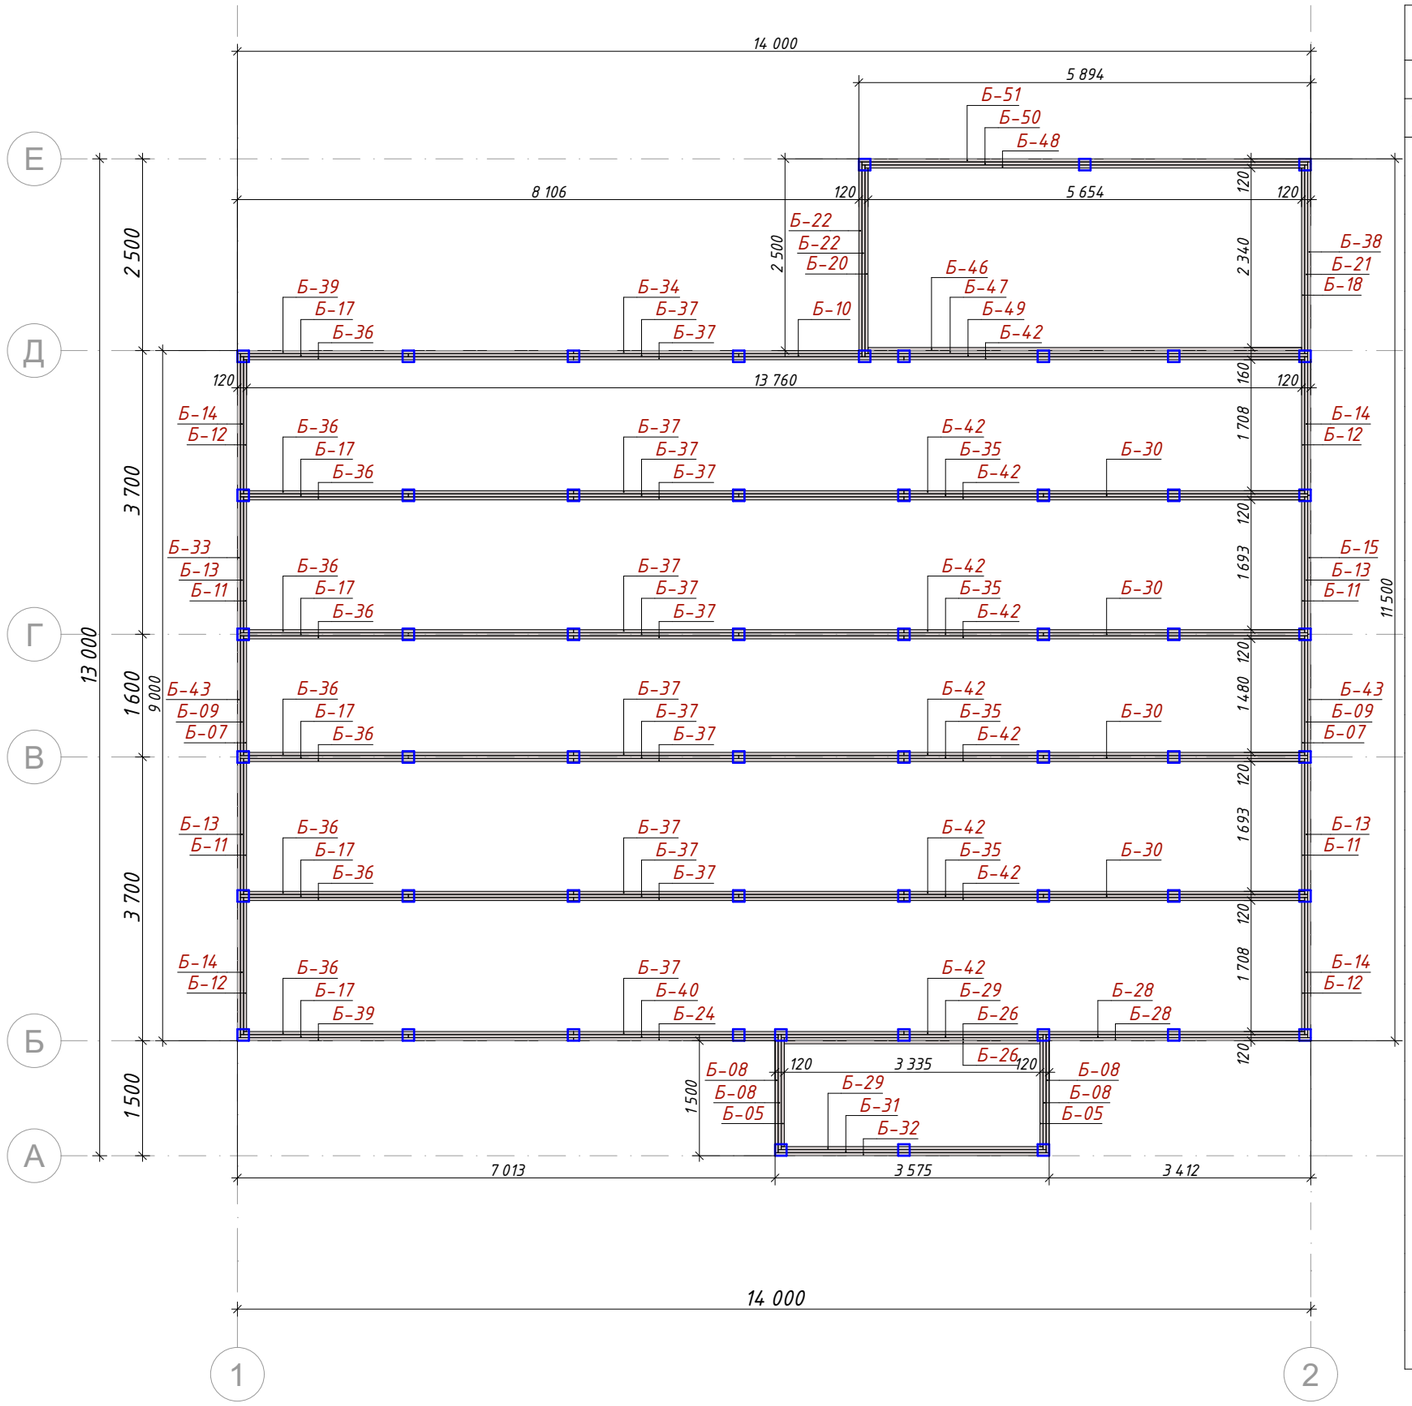

КД Спецификация деревянных элементов ростверка

Сечение	Марка	Длина	Кол-во	Объем
40х200				
	Б-05	1 420	2	0,023
	Б-07	1 480	2	0,024
	Б-08	1 500	4	0,048
	Б-09	1 560	2	0,025
	Б-10	1 607	1	0,013
	Б-11	1 693	4	0,054
	Б-12	1 708	4	0,055
	Б-13	1 773	4	0,057
	Б-14	1 788	4	0,057
	Б-15	1 813	1	0,015
	Б-17	2 190	6	0,105
	Б-18	2 380	1	0,019
	Б-20	2 420	1	0,019
	Б-21	2 460	1	0,020
	Б-22	2 500	2	0,040
	Б-24	2 629	1	0,021
	Б-26	3 335	2	0,053
	Б-28	3 412	2	0,055
	Б-29	3 415	2	0,055
	Б-30	3 447	4	0,110
	Б-31	3 495	1	0,028
	Б-32	3 575	1	0,029
	Б-33	3 660	1	0,029
	Б-34	3 722	1	0,030
	Б-35	3 974	4	0,127
	Б-36	4 304	10	0,344
	Б-37	4 309	15	0,517
	Б-38	4 348	1	0,035
	Б-39	4 384	2	0,070
	Б-40	4 823	1	0,039
	Б-42	5 226	10	0,418
	Б-43	5 260	2	0,084

КД Спецификация деревянных элементов ростверка


Сечение	Марка	Длина	Кол-во	Объем
	Б-46	5 654	1	0,045
	Б-47	5 694	1	0,046
	Б-48	5 734	1	0,046
	Б-49	5 774	1	0,046
	Б-50	5 814	1	0,047
	Б-51	5 894	1	0,047
				2,893 м³

Примечание:


1. Синими линиями обозначены ж/б сваи.

Изм.	Лист	№ докум.	Подпись	Дата	Схема монтажа ростверка	Лист
1				03/2026		4


Ростверк: 3D-вид

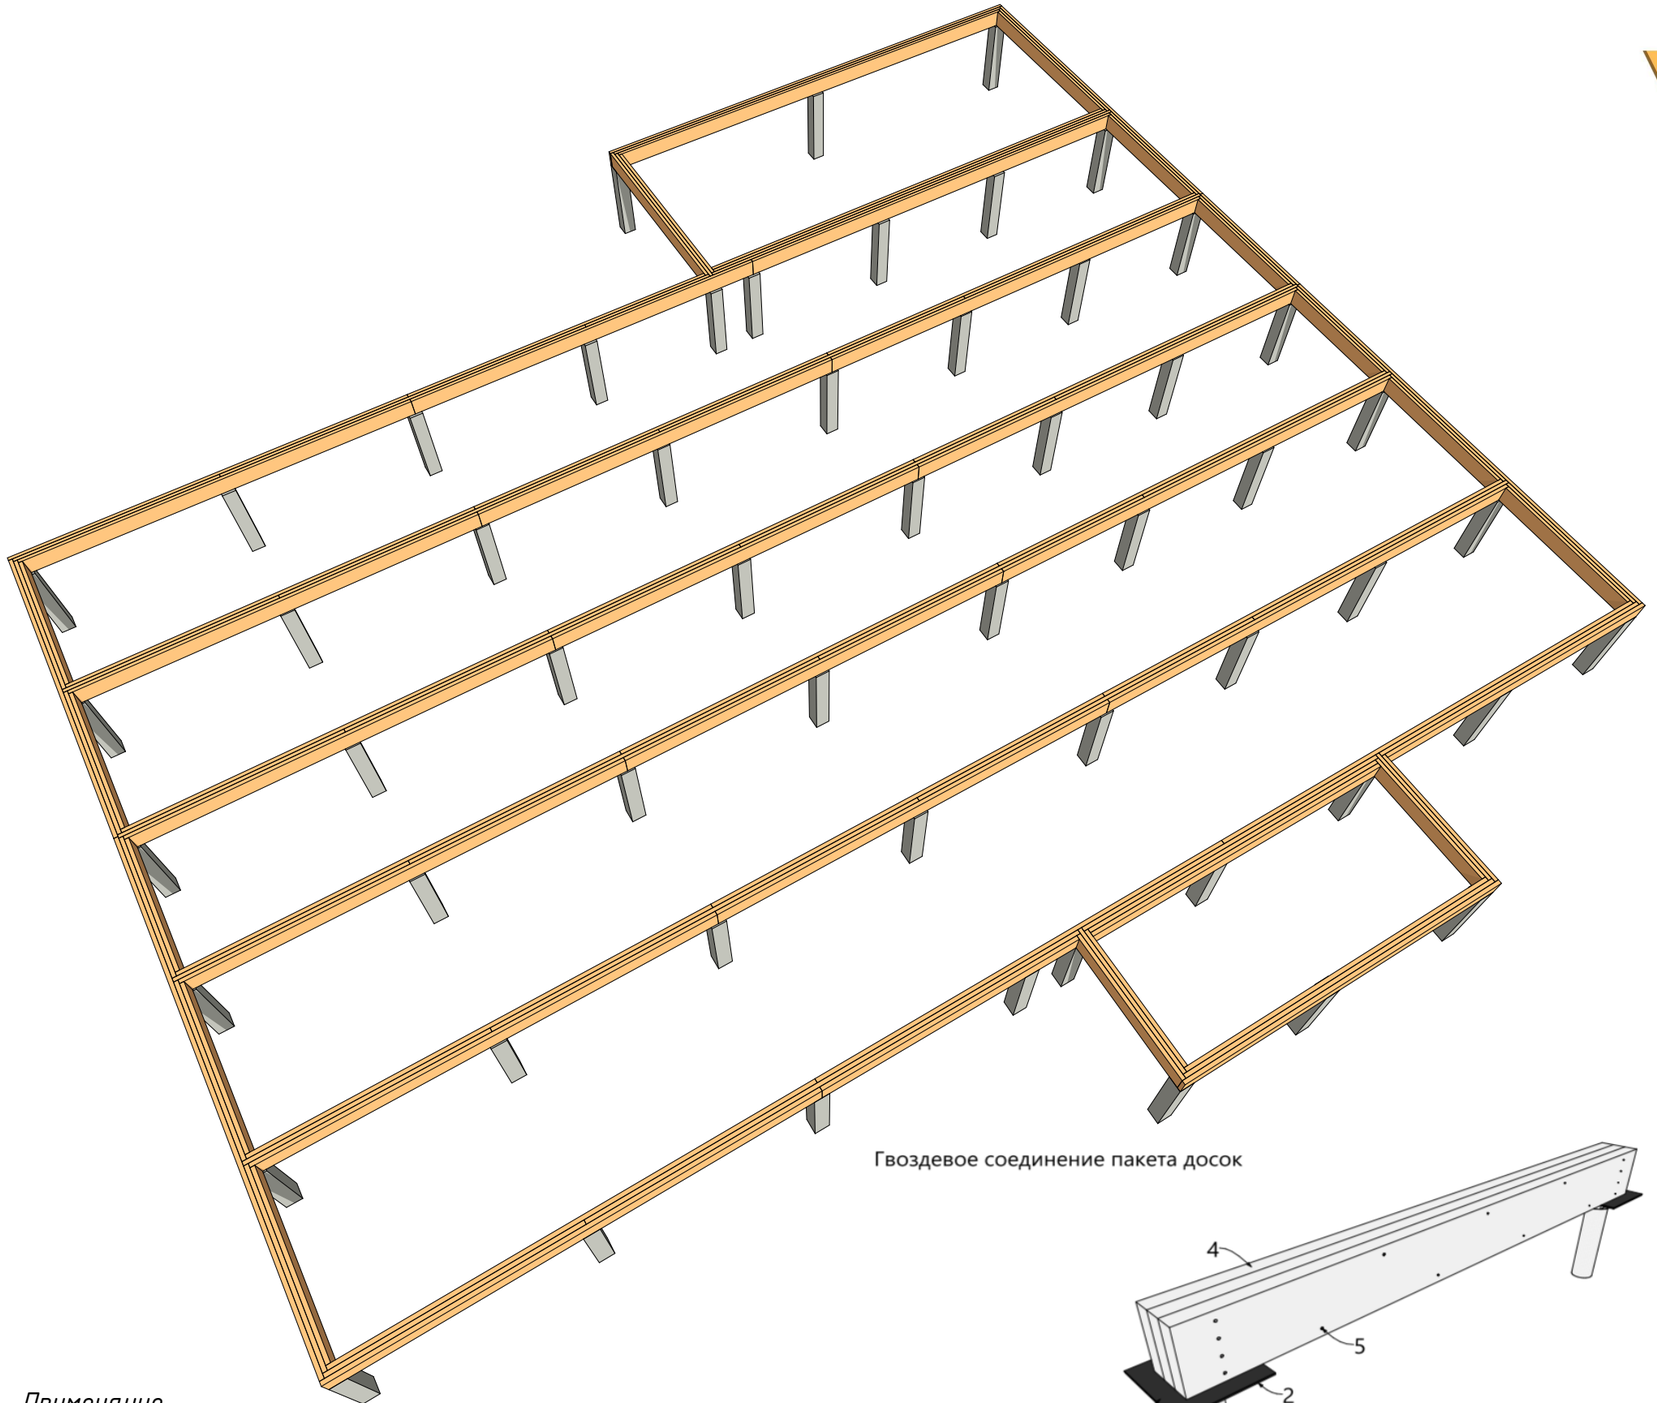

Монтаж сборного ростверка

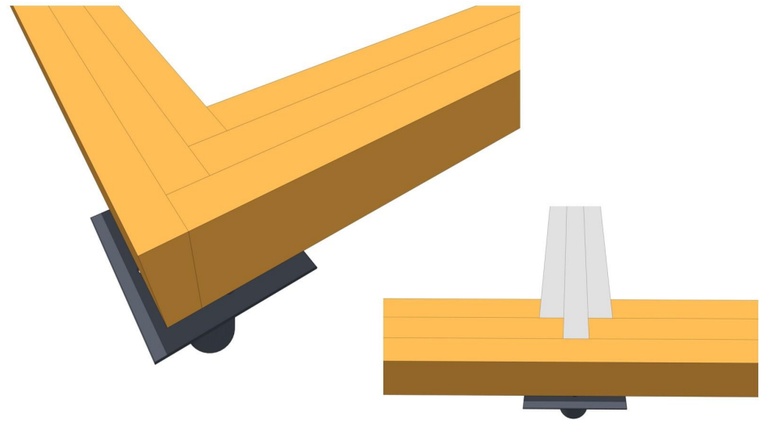


Ф3.03 **Т-образное соединение 1**

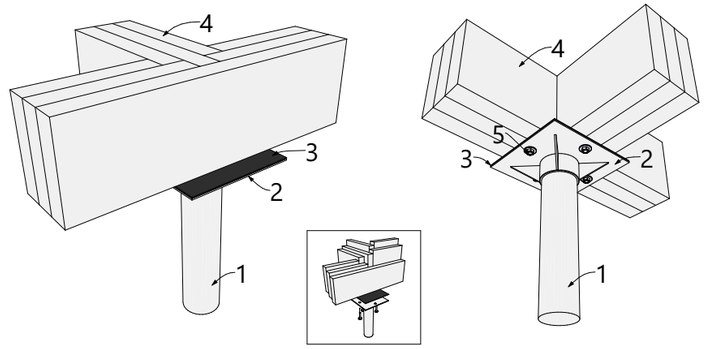


1-свая винтовая; 2-оголовок сваи; 3-рубероид ГОСТ 10923-93; 4-доска;
5-болт сантехнический 10х140 DIN 571 с шайбой DIN 9021.

Гвоздевое соединение пакета досок

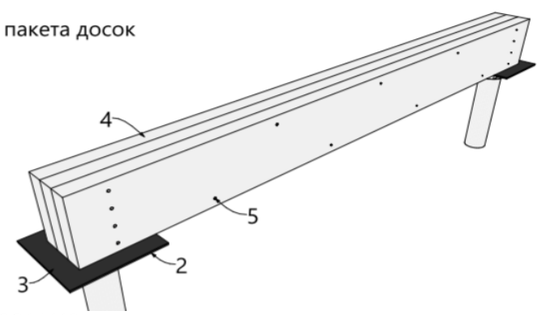

Ф3.01 **Угловое соединение**

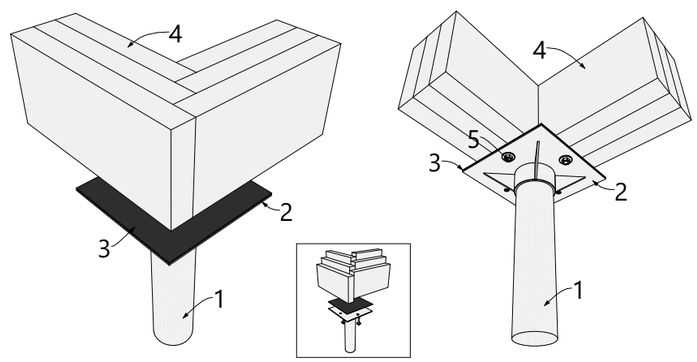

1-свая винтовая; 2-оголовок сваи; 3-рубероид ГОСТ 10923-93; 4-доска;
5-болт сантехнический 10х140 DIN 571 с шайбой DIN 9021.

Примечание.


1. Крепление ростверка к оголовкам свай шурупами для лаг через увеличенную шайбу DIN 9021 M10.


2. Ростверк укладывается на гидроизоляцию стеклоизол/рубероид.

3. Доски ростверка скрепляются между собой оцинкованными гвоздями длиной 150 мм. по 4 гвоздя в торец (для доски 200 мм.) и в два ряда в шахматном порядке с шагом не более 450 мм. в ряду. Минимальное расстояние от кромки – 25 мм.

					Ростверк: 3D-вид	Лист
1				03/2026		5
Изм.	Лист	№ докум.	Подпись	Дата		

Схема монтажа цокольного перекрытия

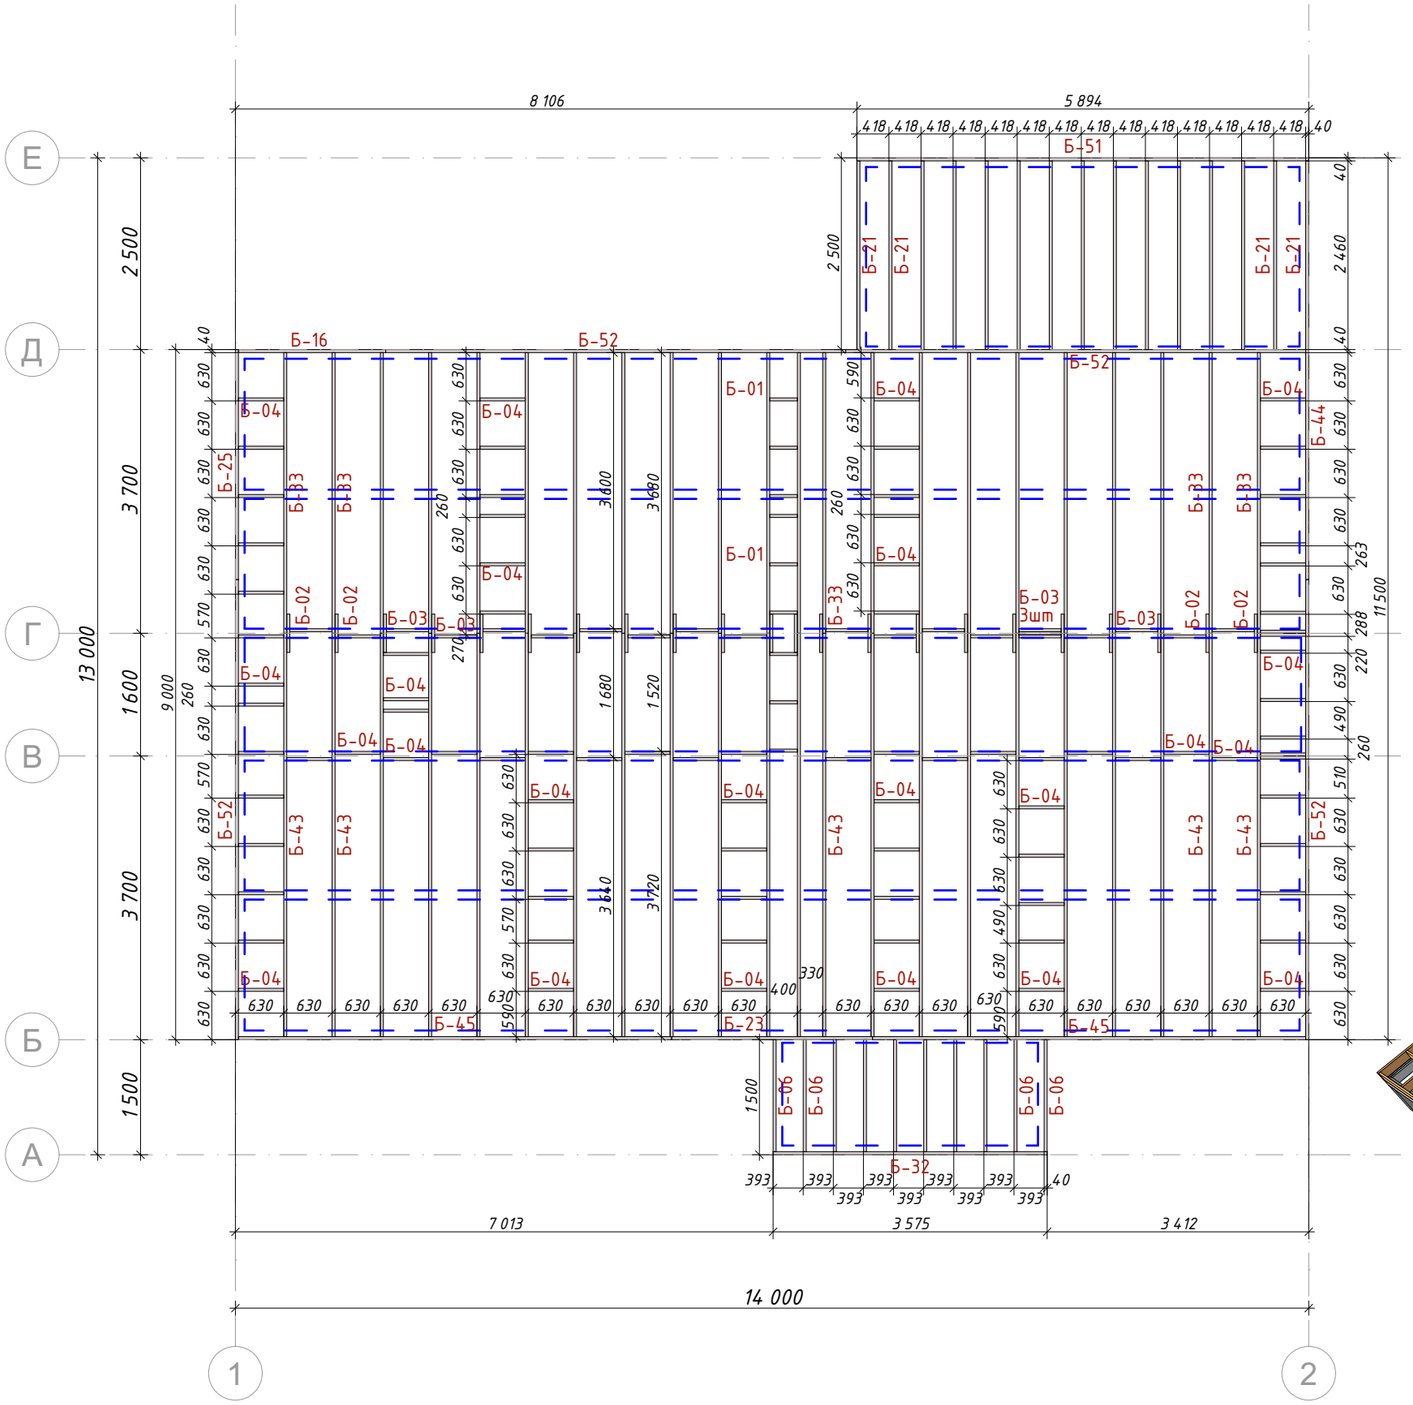

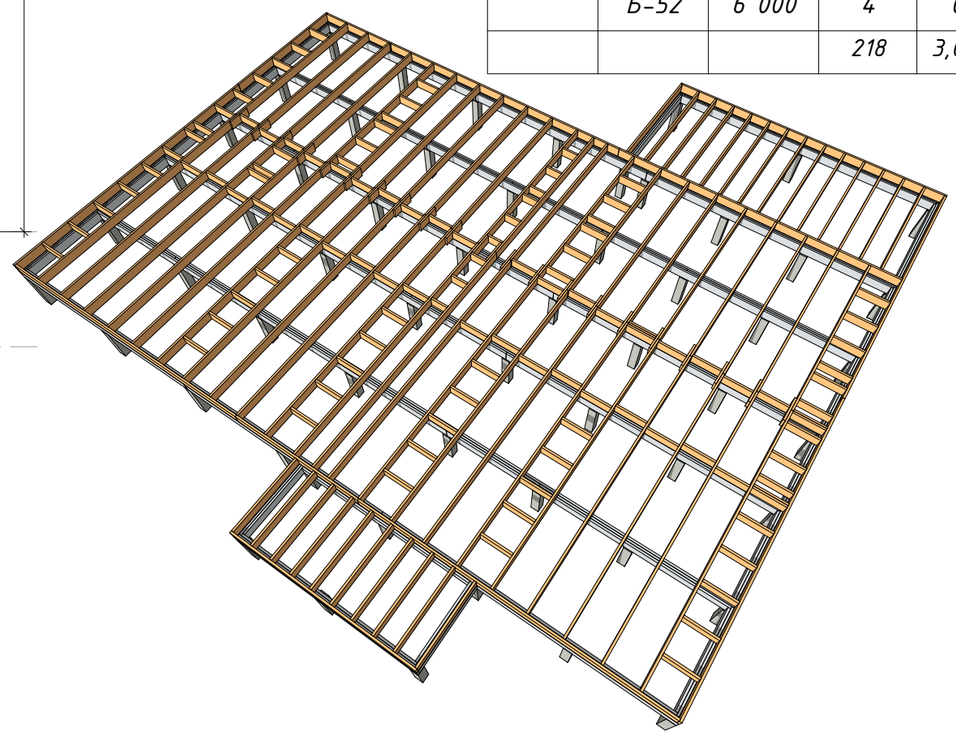

КД Спецификация деревянных элементов цокольного перекрытия				
Сечение	Марка	Длина	Кол-во	Объем
40х200				
	Б-01	360	9	0,026
	Б-02	500	22	0,088
	Б-03	550	21	0,092
	Б-04	590	86	0,406
	Б-06	1 460	10	0,117
	Б-16	1 920	1	0,015
	Б-21	2 460	14	0,276
	Б-23	2 620	1	0,021
	Б-25	3 000	1	0,024
	Б-32	3 575	1	0,029
	Б-33	3 660	22	0,644
	Б-43	5 260	22	0,926
	Б-44	5 460	1	0,044
	Б-45	5 650	2	0,090
	Б-51	5 894	1	0,047
	Б-52	6 000	4	0,192
			218	3,037 м³


Примечание:

1. Синими линиями обозначены контуры ростверка.

					Схема монтажа цокольного перекрытия	Лист
1				03/2026		6
Изм.	Лист	№ докум.	Подпись	Дата		


Узлы цокольного перекрытия

П1.01 Крепление обвязочной доски перекрытия

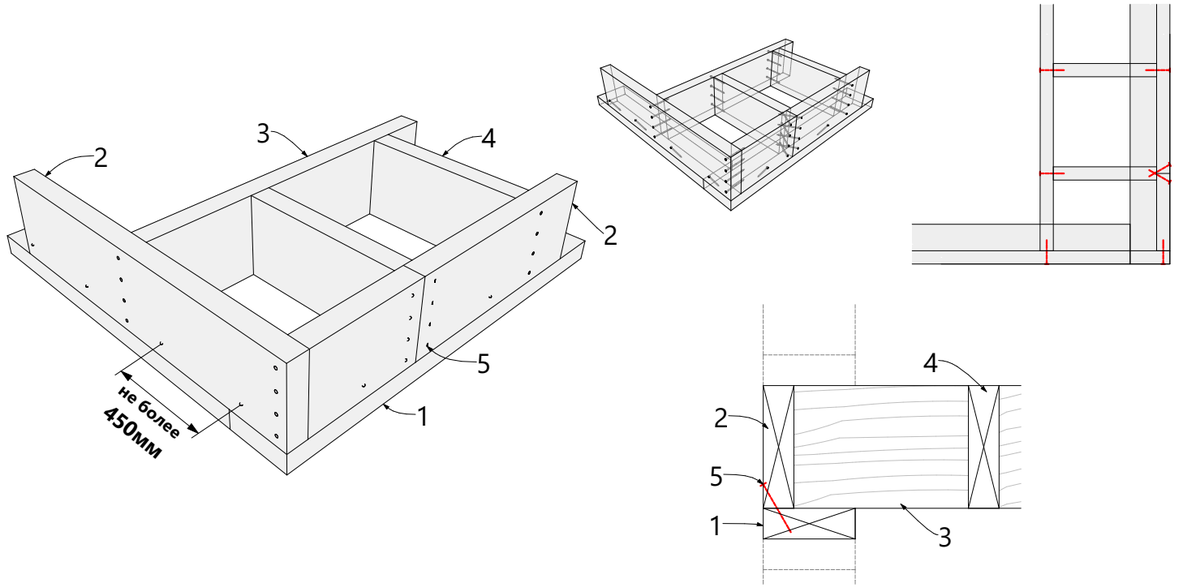


1-опорная доска/вторая верхняя обвязка стены; 2-обвязочная доска перекрытия; 3-балка перекрытия; 4-блок балка (перемычка); 5-гвоздь.

П1.06 Крепление распорок под стеной между балками перекрытия

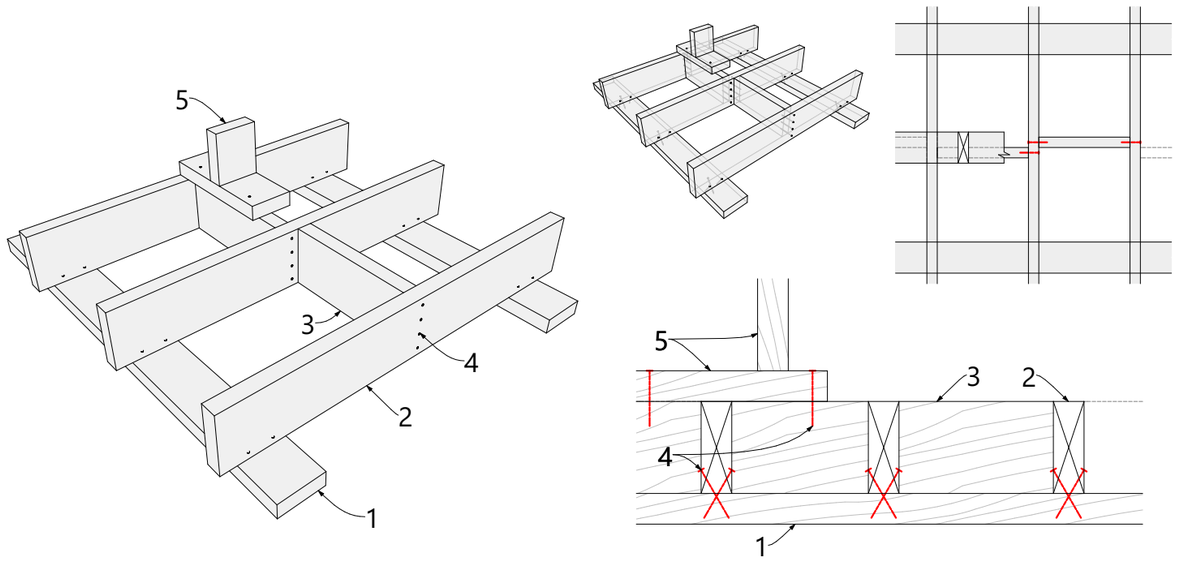


1-опорная доска/вторая верхняя обвязка стены; 2-балка перекрытия; 3-блок балка (перемычка/распорка); 4-гвоздь; 5-каркас стены.

П1.07 Соединение в торец балок перекрытия на опоре

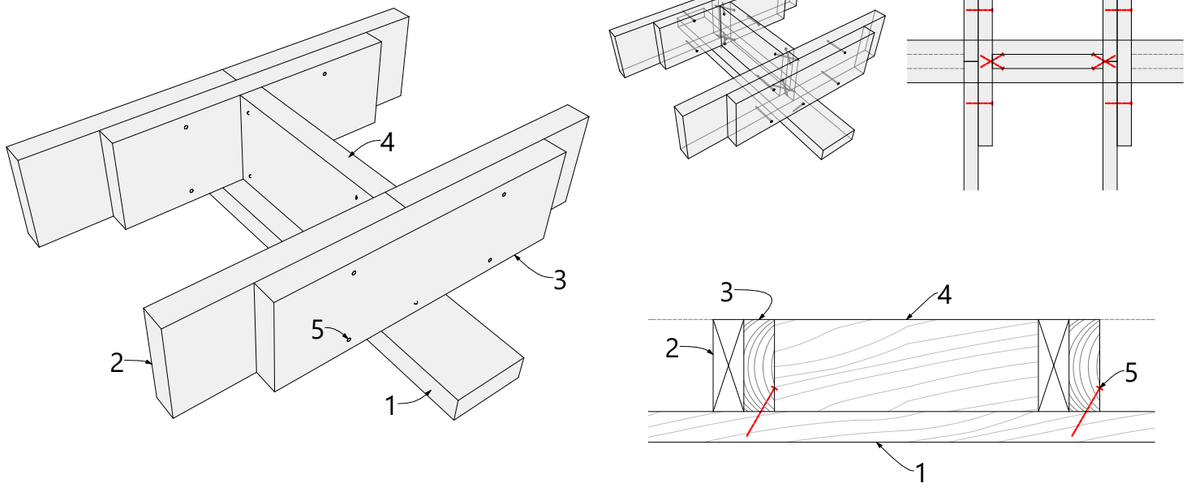

1-опорная доска/вторая верхняя обвязка стены; 2-балка перекрытия; 3-накладная доска; 4-блок балка (перемычка); 5-гвоздь.

Опора перегородки на перемычки перекрытия

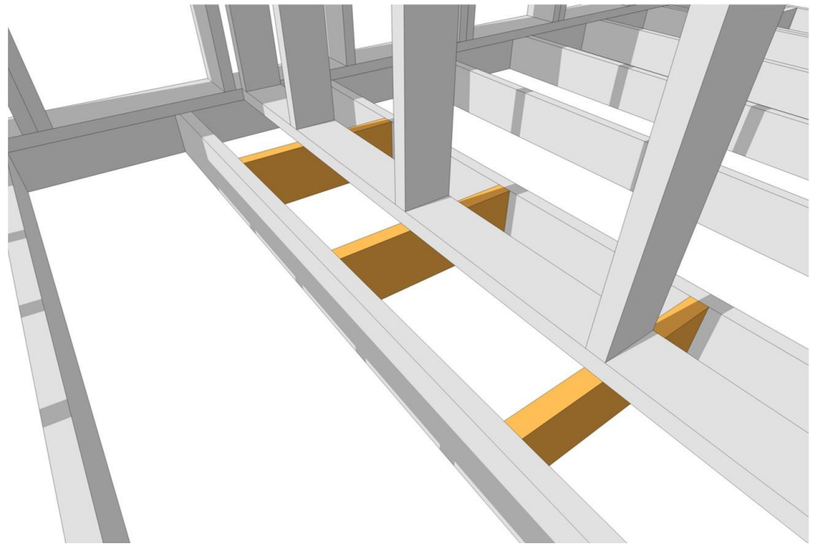


Примечание.


1. Элементы цокольного перекрытия скрепляются между собой оцинкованными гвоздями длиной 100/150 мм. по 4 гвоздя в торец (для доски 200 мм.). Минимальное расстояние от кромки – 25 мм.


					Узлы цокольного перекрытия	Лист
1				03/2026		7
Изм.	Лист	№ докум.	Подпись	Дата		

План стен 1-го этажа

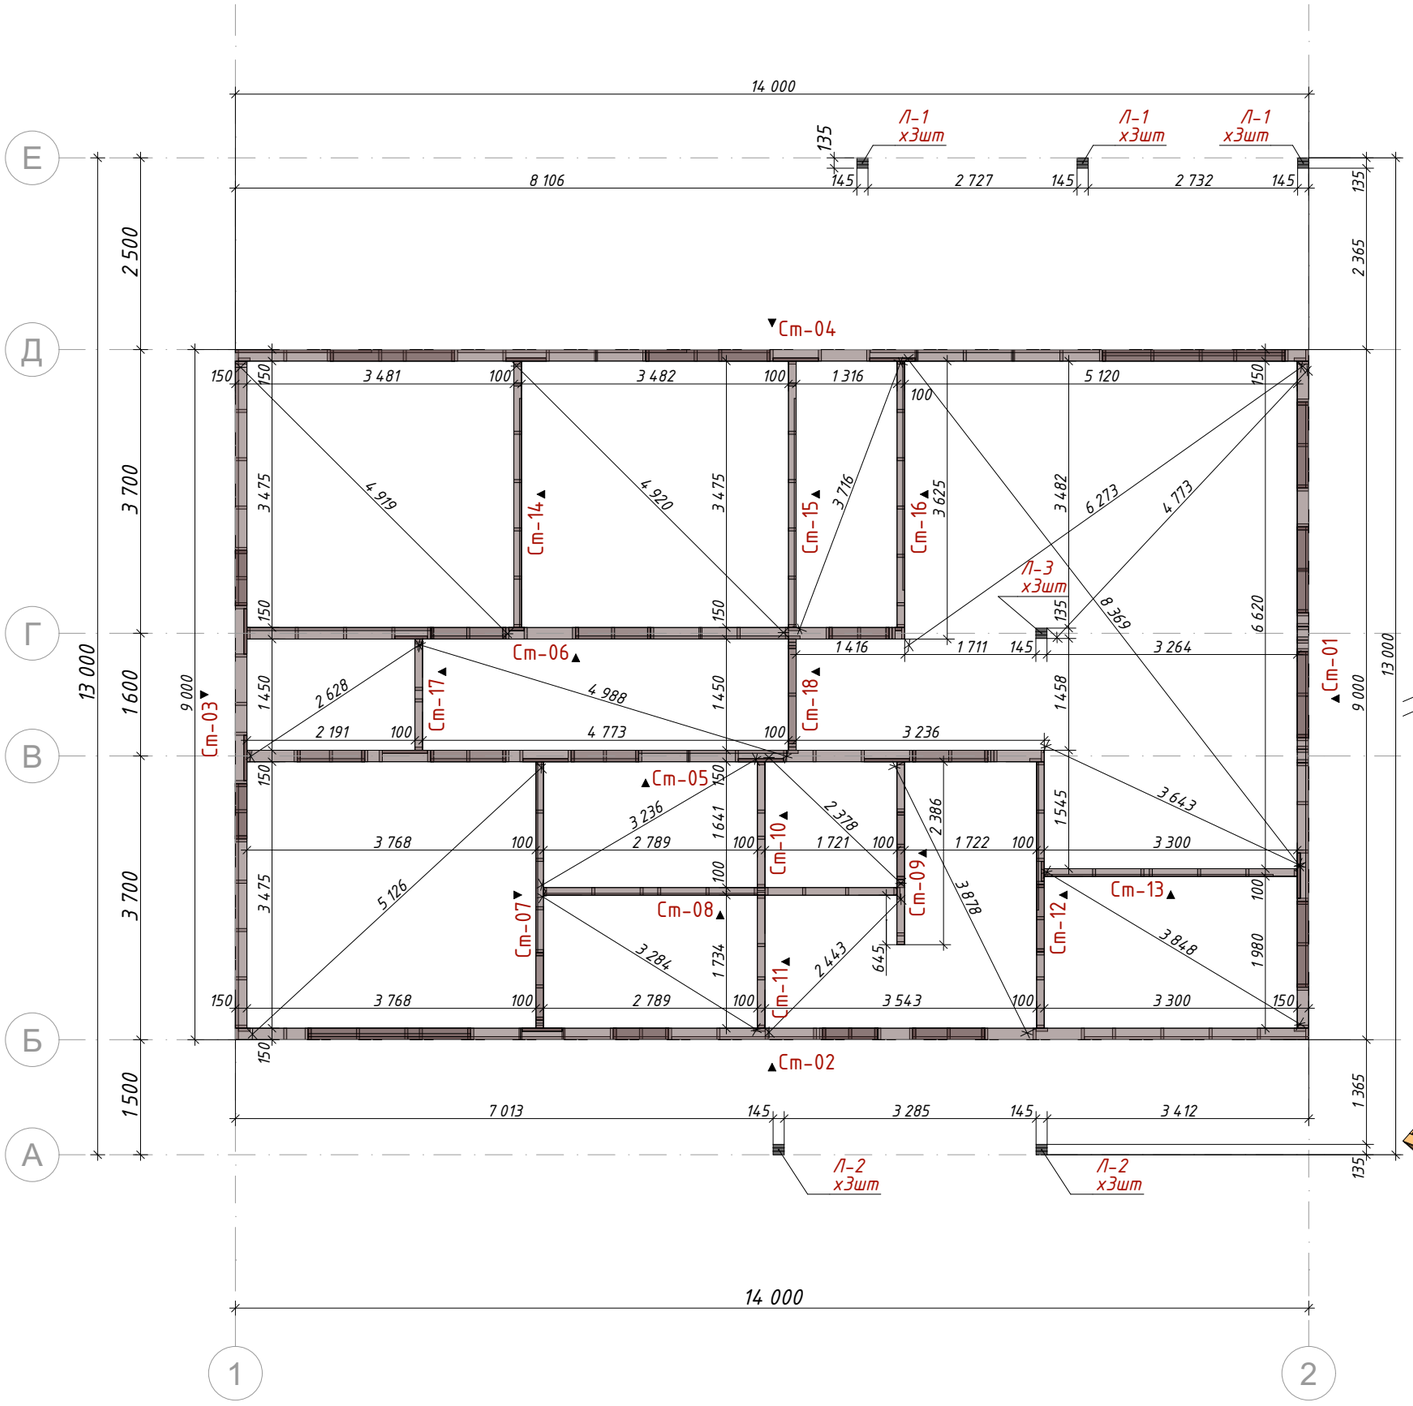

КД Спецификация деревянных элементов опор террасы				
Сечение	Марка	Длина	Кол-во	Объем
45х145				
	Л-1	2 245	9	0,127
	Л-2	2 610	6	0,098
	Л-3	2 725	3	0,053
				0,279 м³

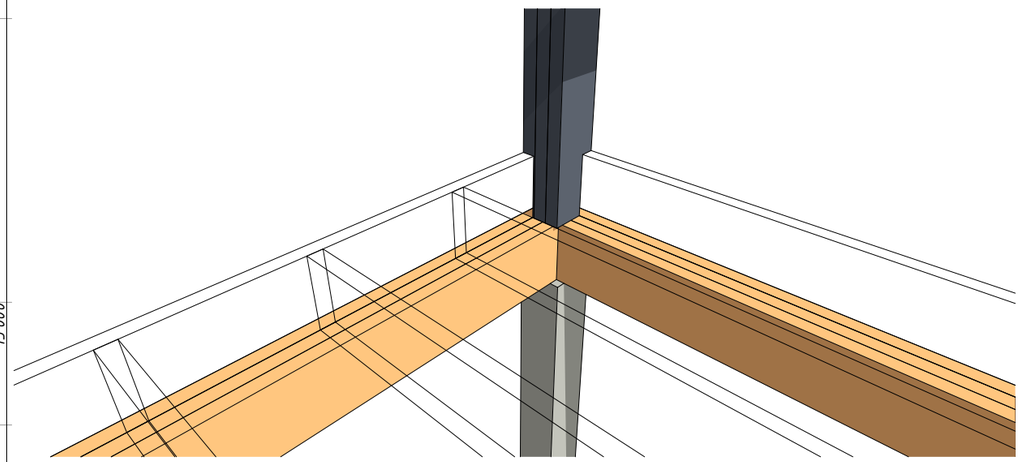

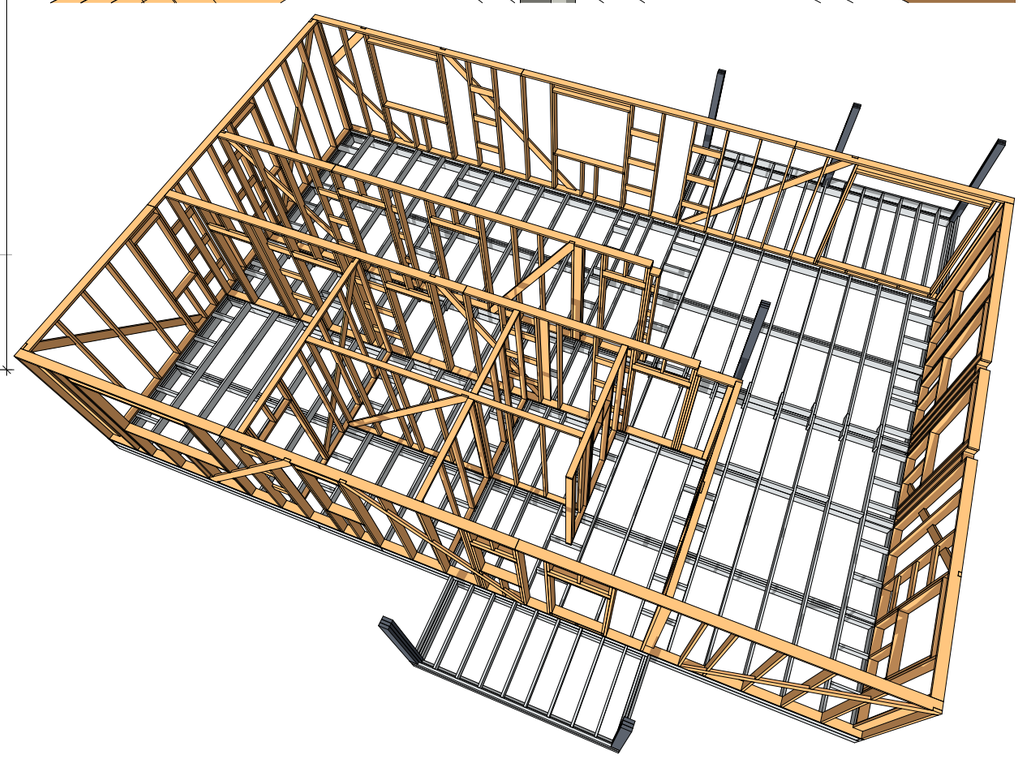

Примечание.


1. Опоры террасы монтируются из пакета строганных досок камерной сушки хвойных пород сечением 45х145 мм. Крепёж – оцинкованные гвозди 100 мм.

2. Опоры террасы устанавливаются на ростверк с запилом под элементы цокольного перекрытия.


1				03/2026	План стен 1-го этажа	Лист 8
Изм.	Лист	№ докум.	Подпись	Дата		

Узлы каркасных стен (1)


Укосины вид 1 (верх)

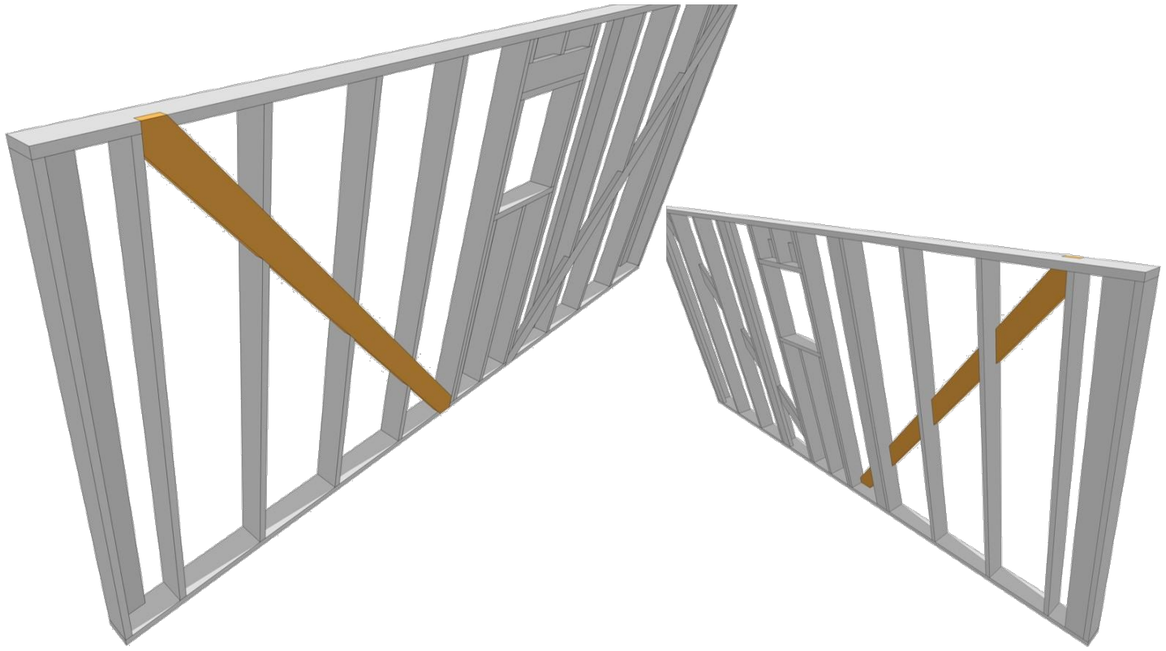


Укосины вид 2 (низ)

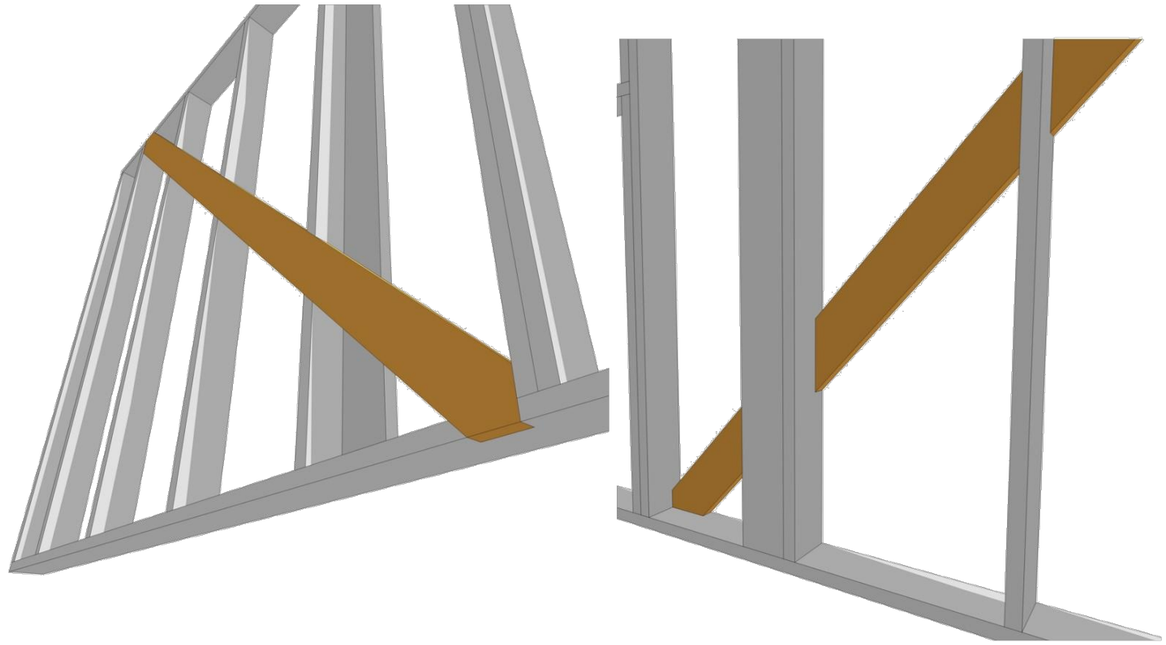

Укосина перегородки

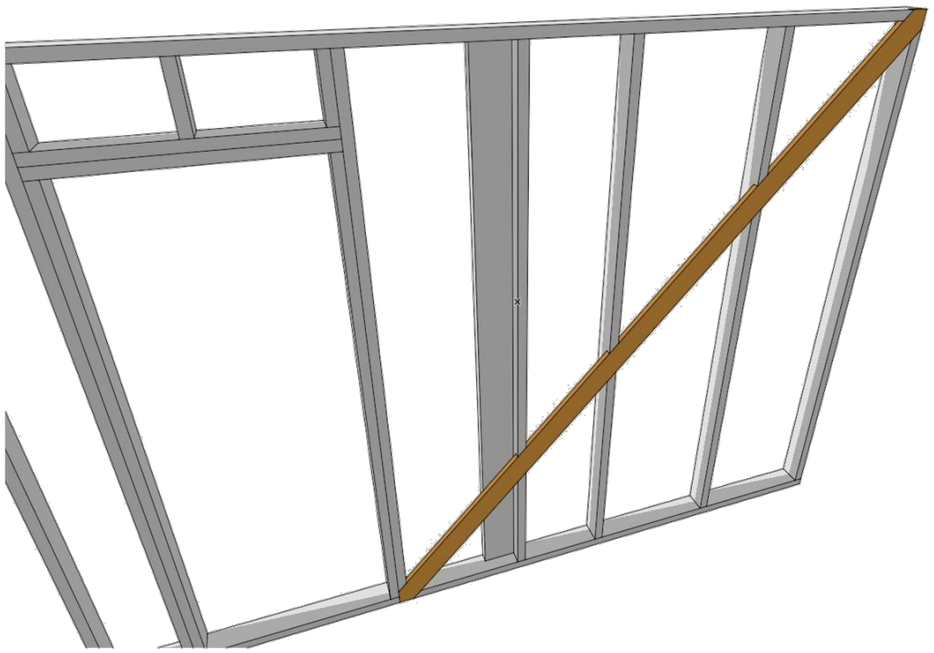


К-образный монтаж укосин

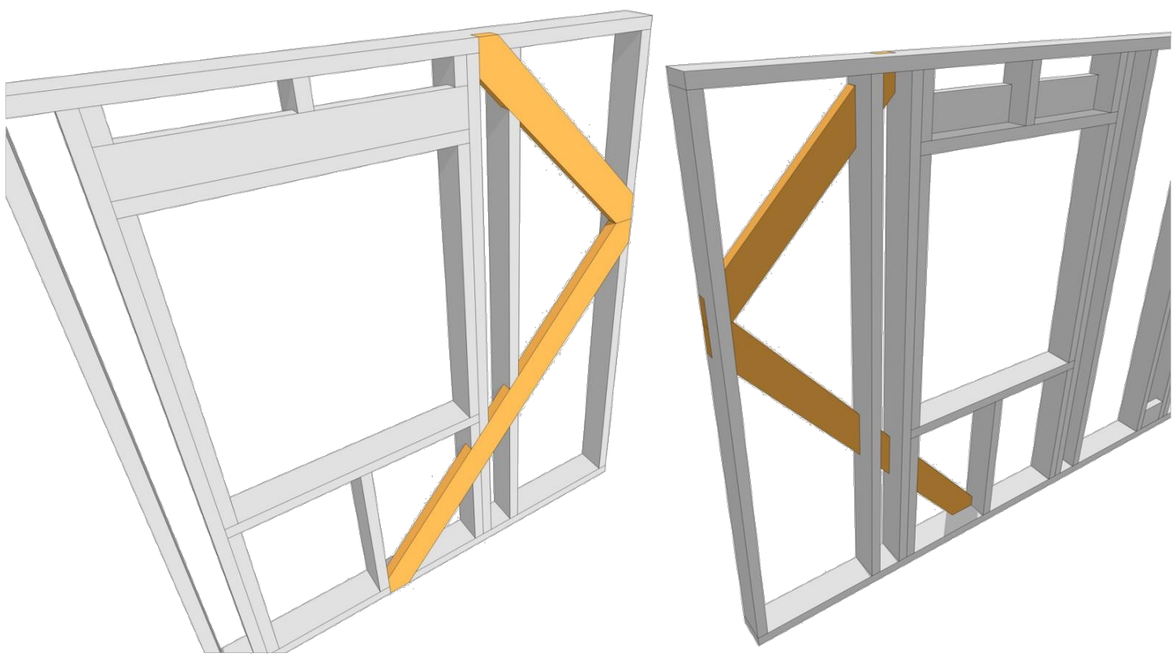


					Узлы каркасных стен (1)	Лист
1				03/2026		9
Изм.	Лист	№ докум.	Подпись	Дата		

Узлы каркасных стен (2)


Г-образное соединение внешних стен (теплый угол)

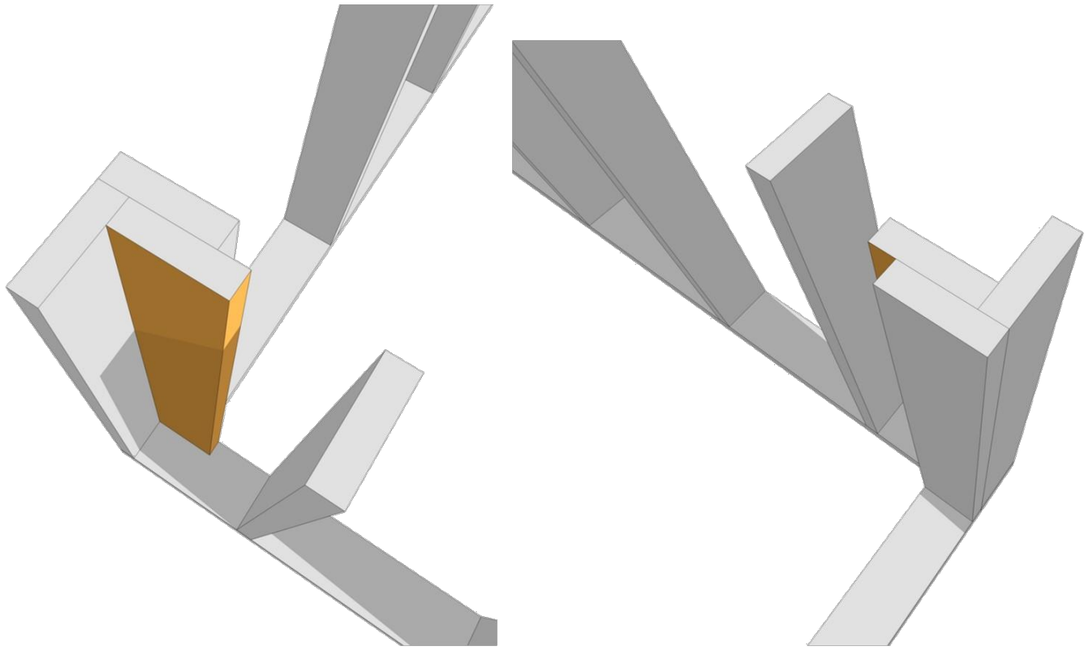


Г-образное примыкание стен/перегородок

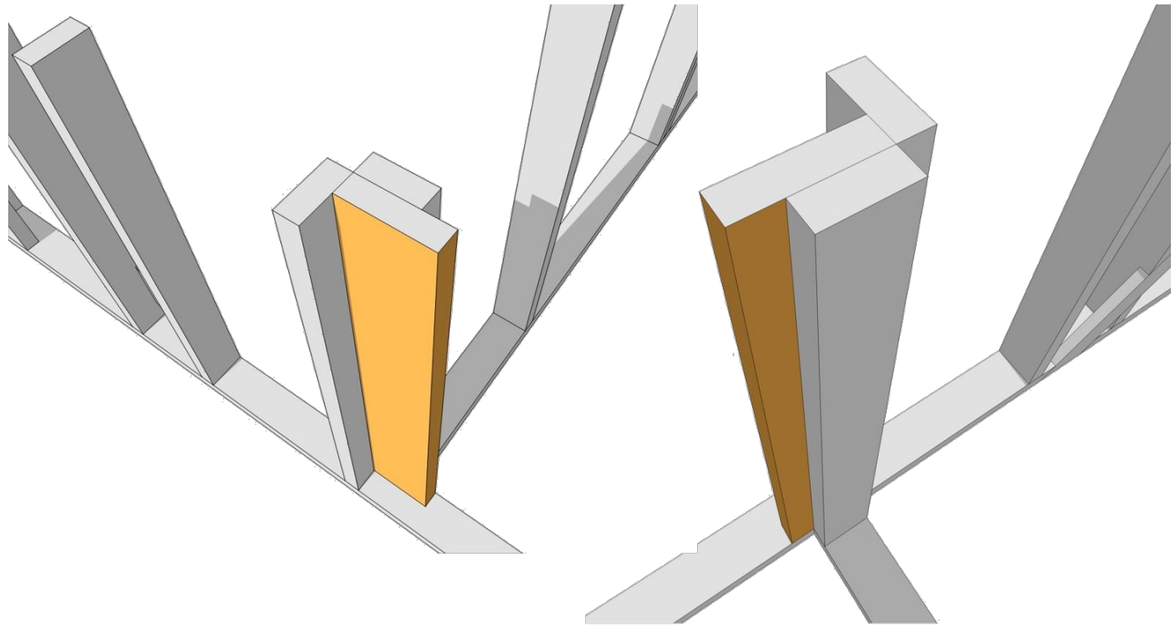

Т-образное примыкание стен/перегородок (перемычки)

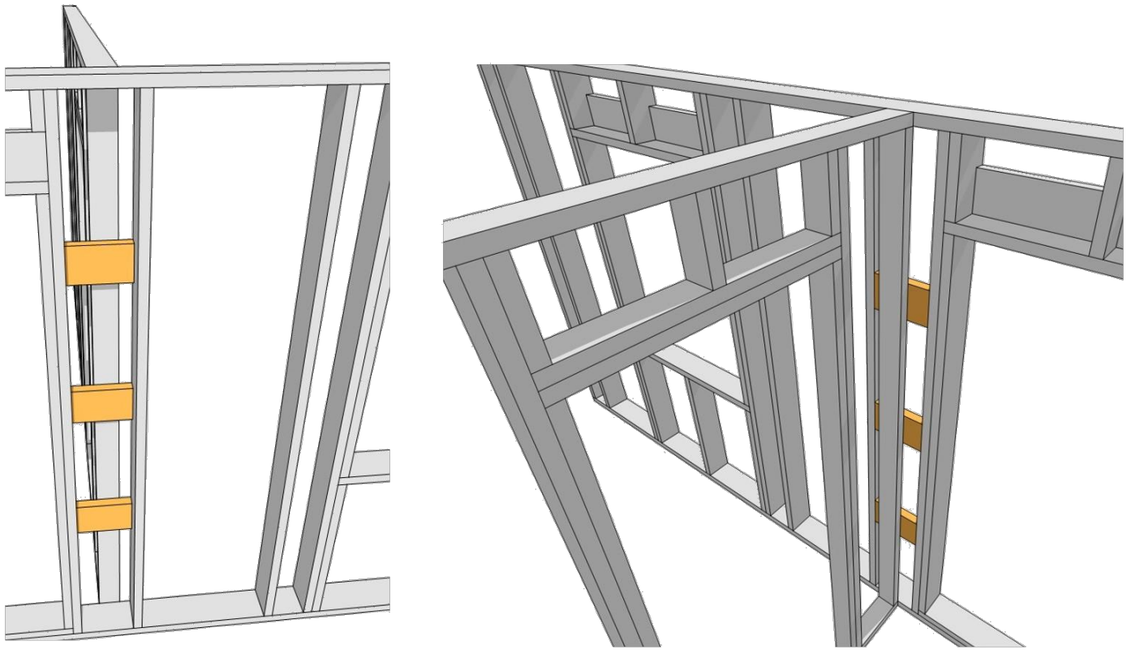

Пароизоляционные закладные перегородок

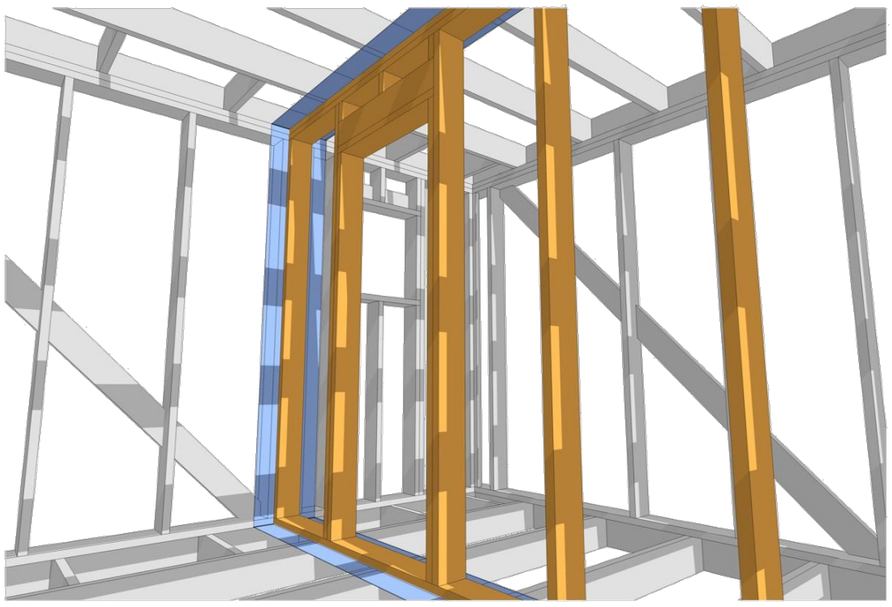


					Узлы каркасных стен (2)	Лист
1				03/2026		10
Изм.	Лист	№ докум.	Подпись	Дата		

Узлы каркасных стен (3)


Проем входной двери




Проем межкомнатной двери перегородки без нагрузки

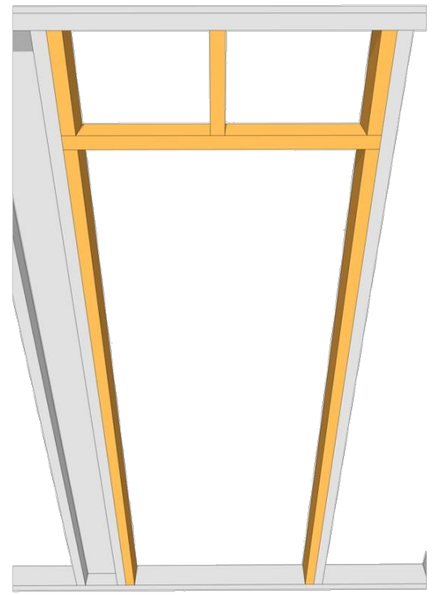

Проем межкомнатной двери несущей перегородки

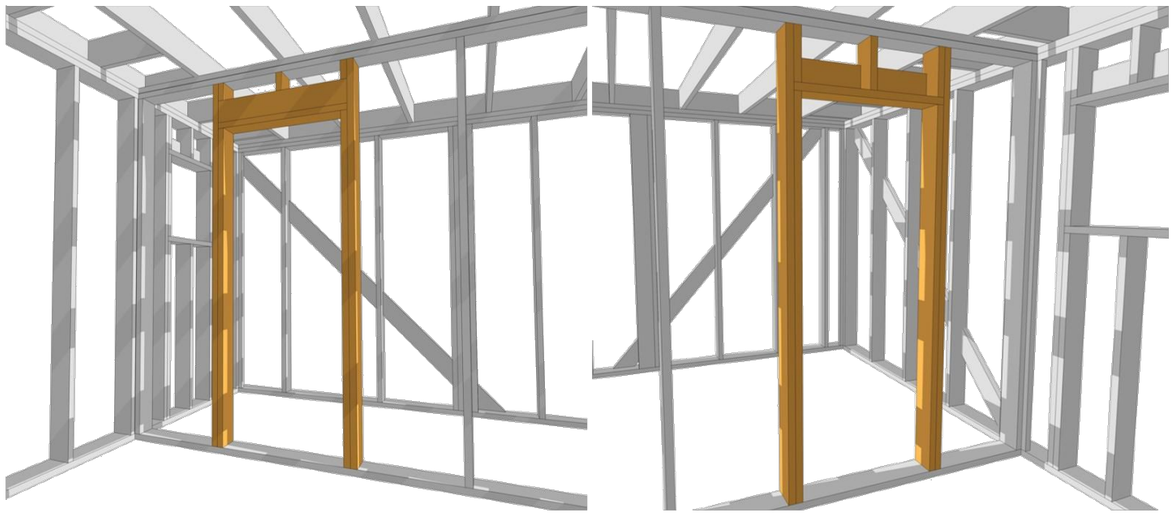


Оконный проем (вар.1)

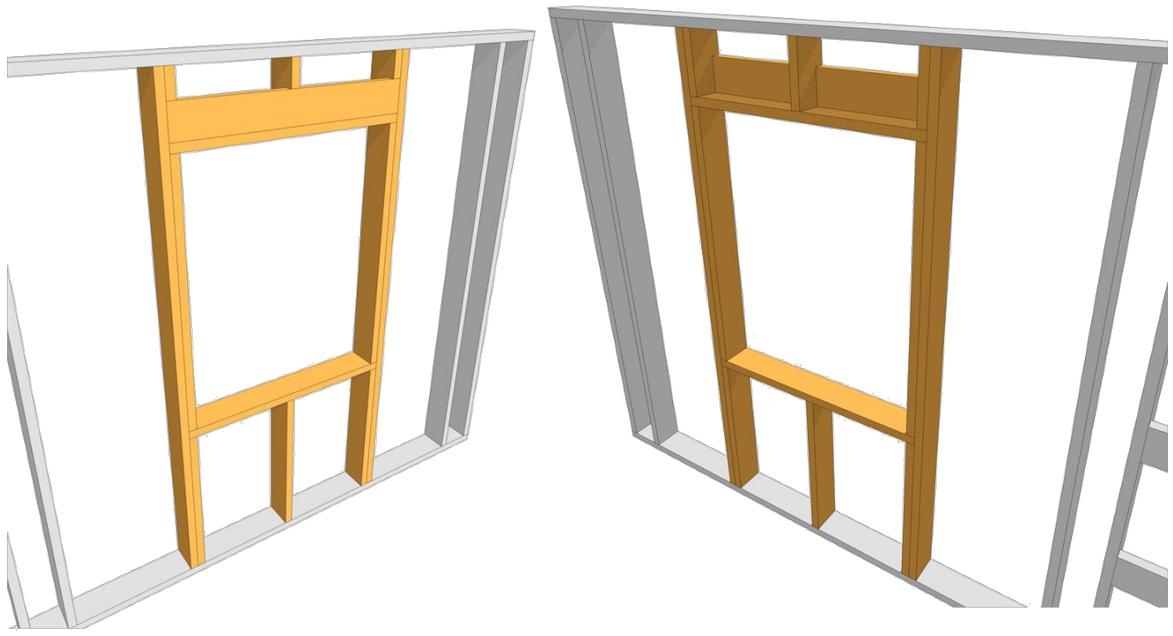

					Узлы каркасных стен (3)	Лист
1				03/2026		11
Изм.	Лист	№ докум.	Подпись	Дата		


Узлы каркасных стен (4)

С2.06 Угловое соединение каркасных стен.

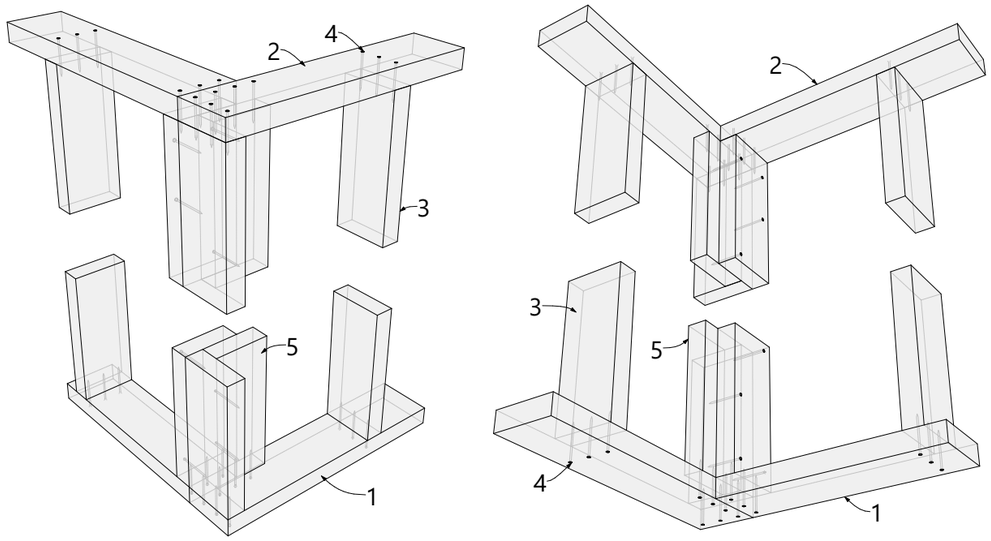


1-нижняя обвязка каркасной стены; 2-верхняя обвязка каркасной стены; 3-стойка каркасной стены; 4-гвоздь; 5-стойка для крепления отделки.

С2.08 Соединения каркасных стены. L-образное примыкание

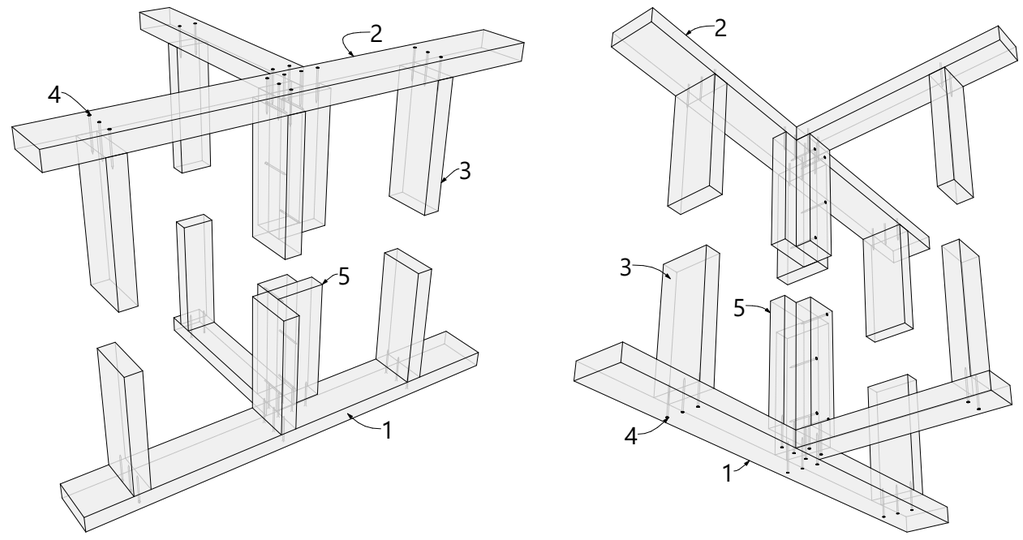


1-нижняя обвязка каркасной стены; 2-верхняя обвязка каркасной стены; 3-стойка каркасной стены; 4-гвоздь; 5-стойка для крепления отделки.

С2.03 Соединения элементов мансардной каркасной стены

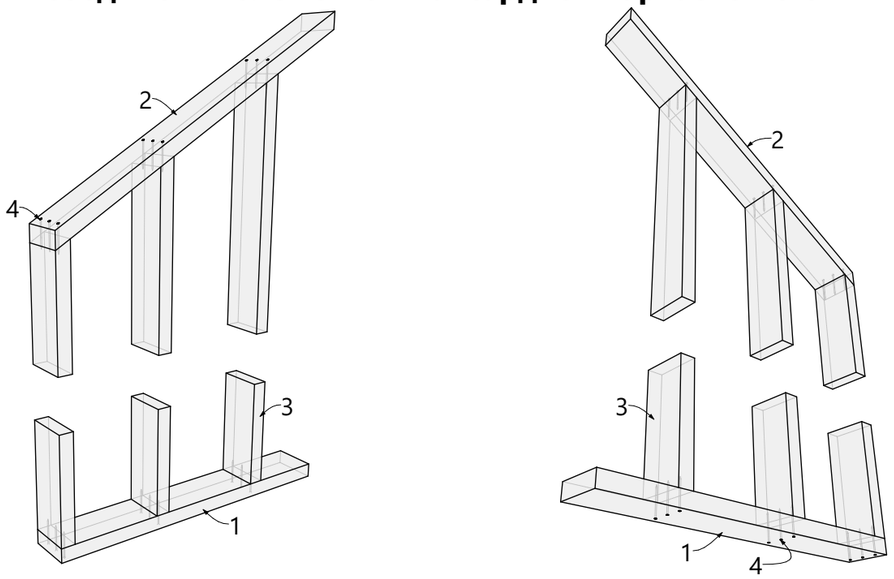

1-нижняя обвязка каркасной стены; 2-верхняя обвязка каркасной стены; 3-стойка каркасной стены; 4-гвоздь.


С2.10 Соединения каркасных стены. Перемычки

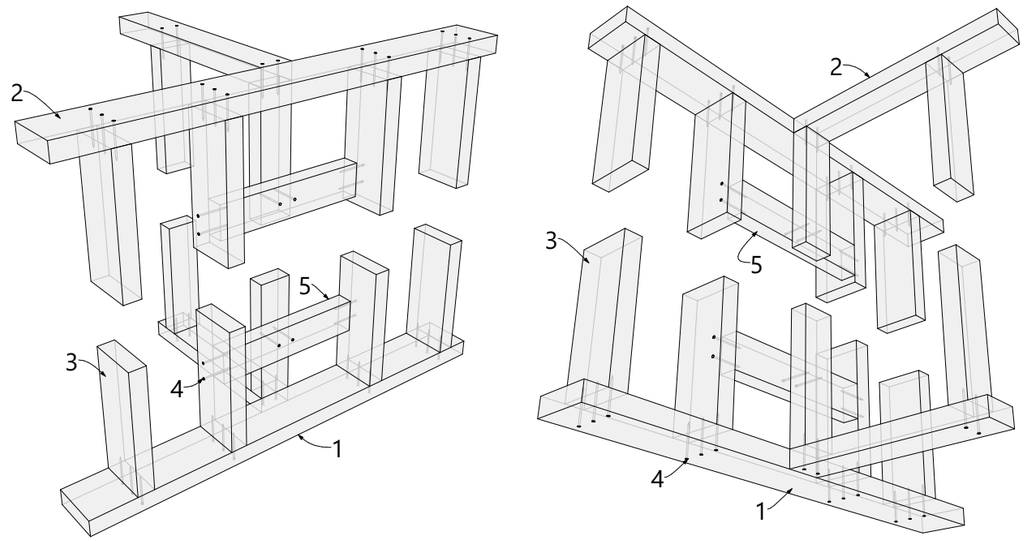

1-нижняя обвязка каркасной стены; 2-верхняя обвязка каркасной стены; 3-стойка каркасной стены; 4-гвоздь; 5-перемычка для соединения стен.

1				03/2026	Узлы каркасных стен (4)	Лист 12
Изм.	Лист	№ докум.	Подпись	Дата		


Стена Ст-01

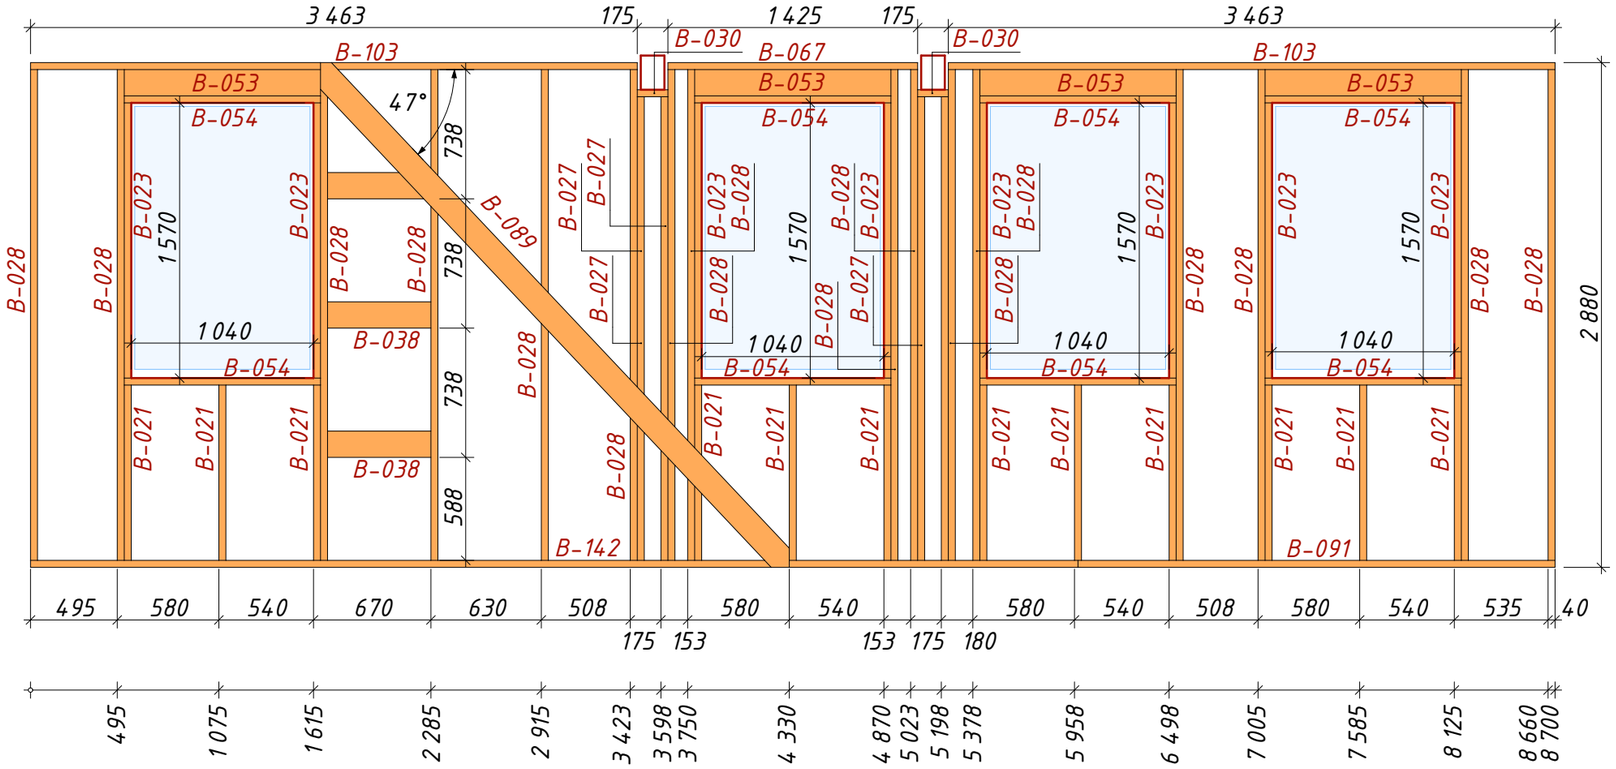


▲ Ст-01

КД Спецификация деревянных элементов стены Ст-01


Сечение	Марка	Длина	Кол-во	Объем
40х150				
	В-030	175	2	0,002
	В-038	590	3	0,011
	В-021	1 000	12	0,072
	В-054	1 120	8	0,054
	В-053	1 120	4	0,027
	В-067	1 425	1	0,009
	В-023	1 570	8	0,075
	В-027	2 645	4	0,063
	В-091	2 723	1	0,016
	В-028	2 800	16	0,267
	В-103	3 463	2	0,041
	В-089	4 058	1	0,023
	В-142	5 978	1	0,036
				0,695 м³

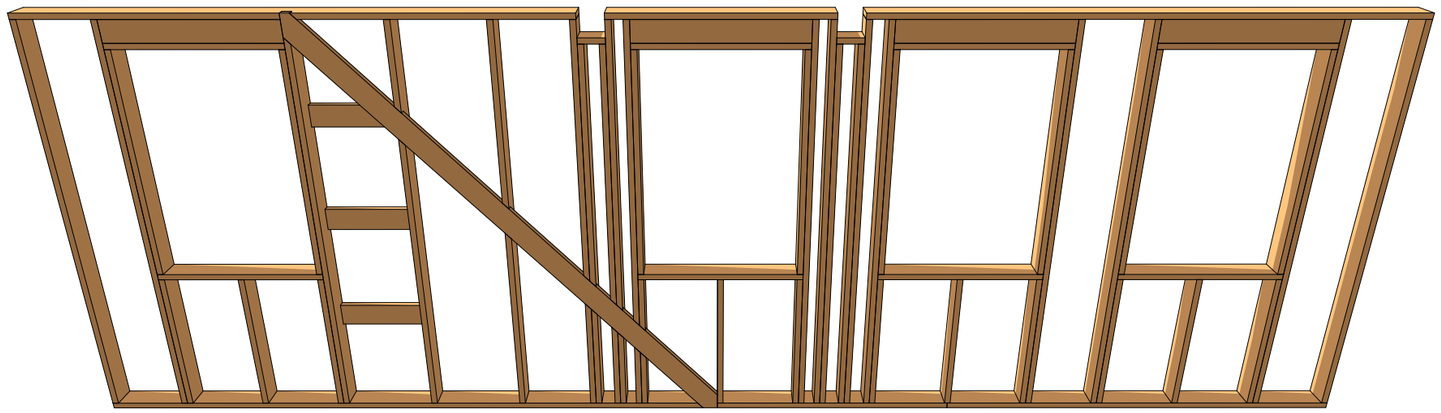

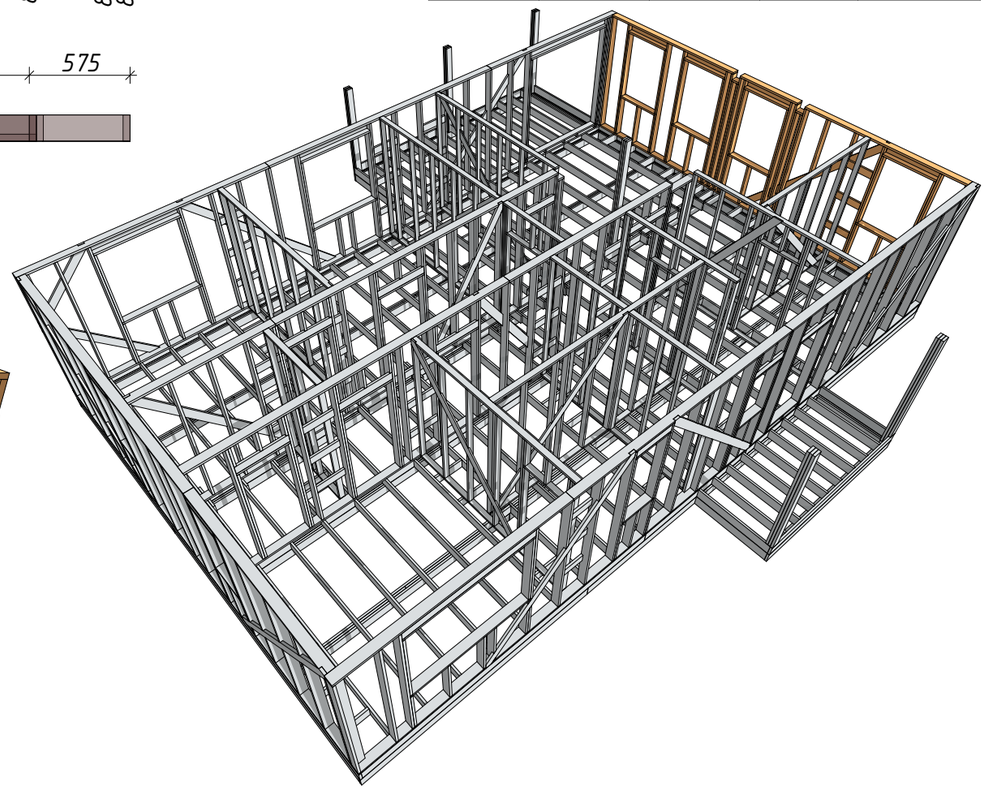


Изм.	Лист	№ докум.	Подпись	Дата		Лист
1				03/2026	Стена Ст-01	13

Стена Ст-02

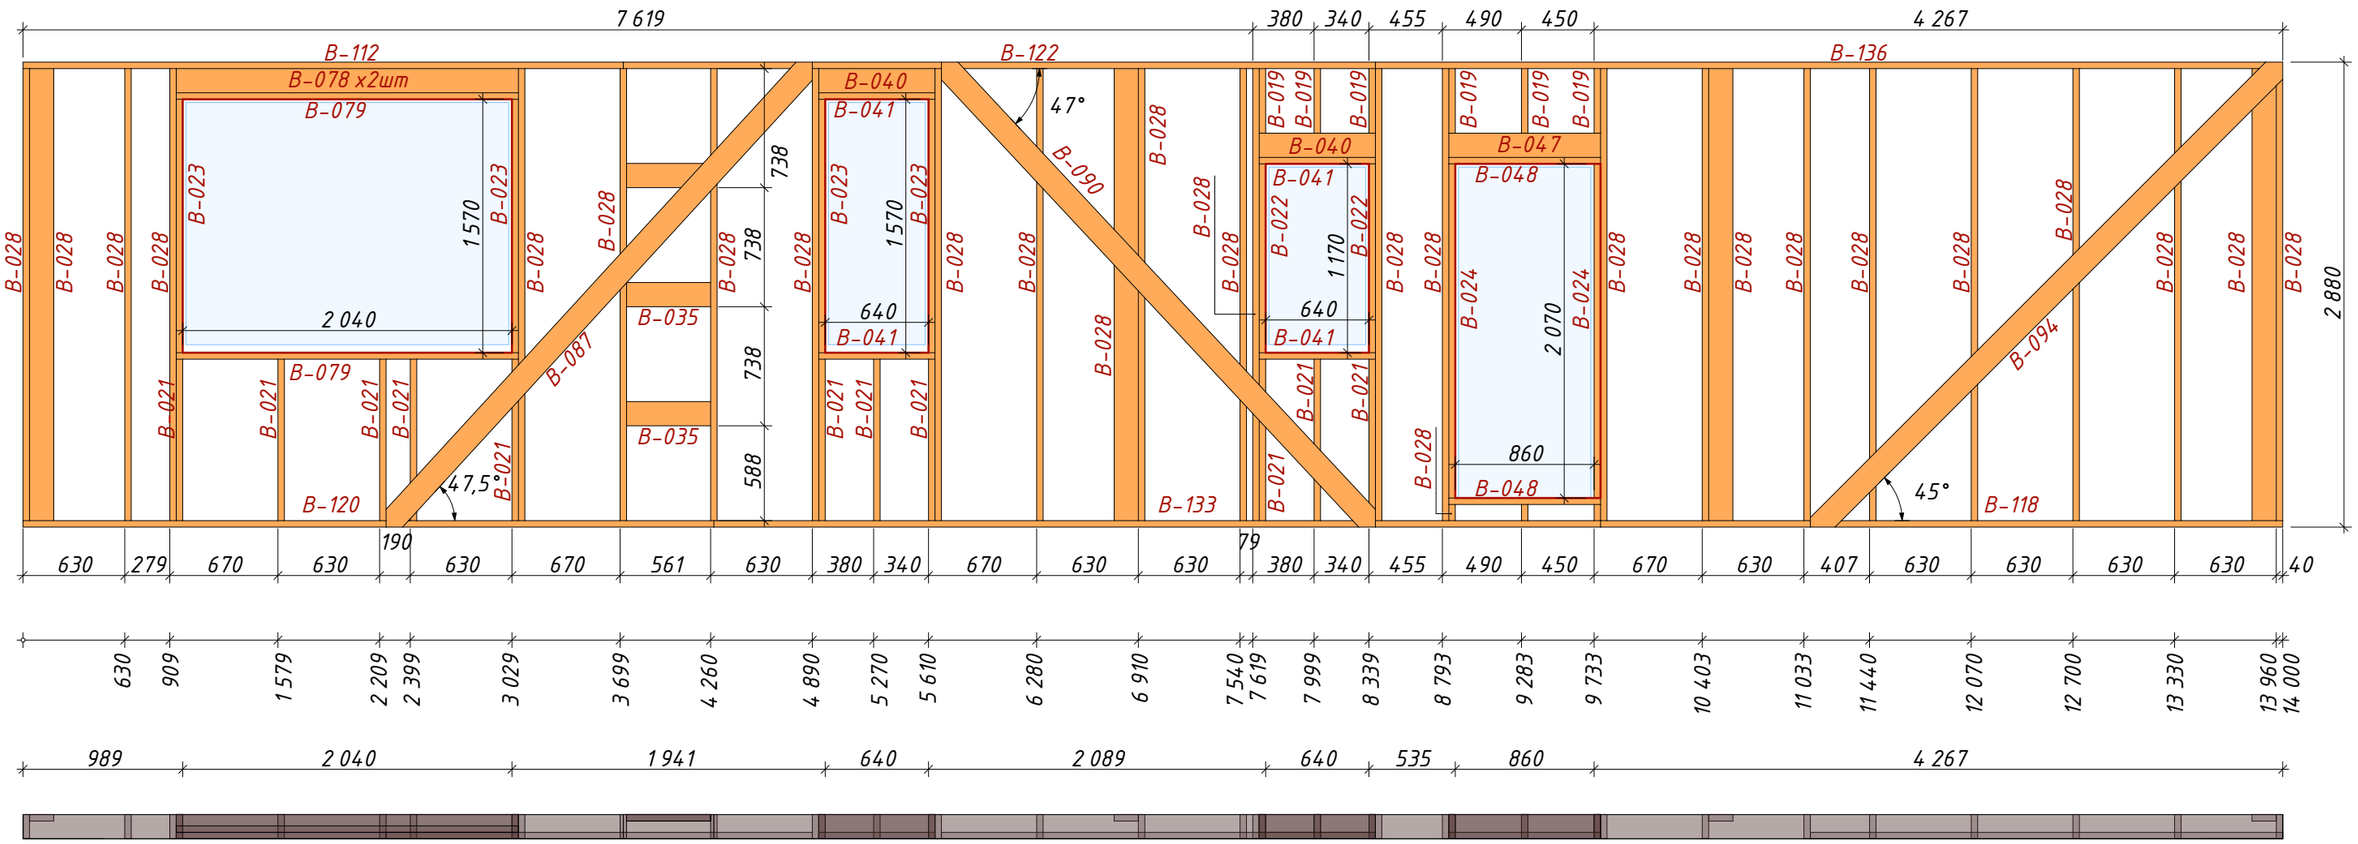


▲ Ст-02

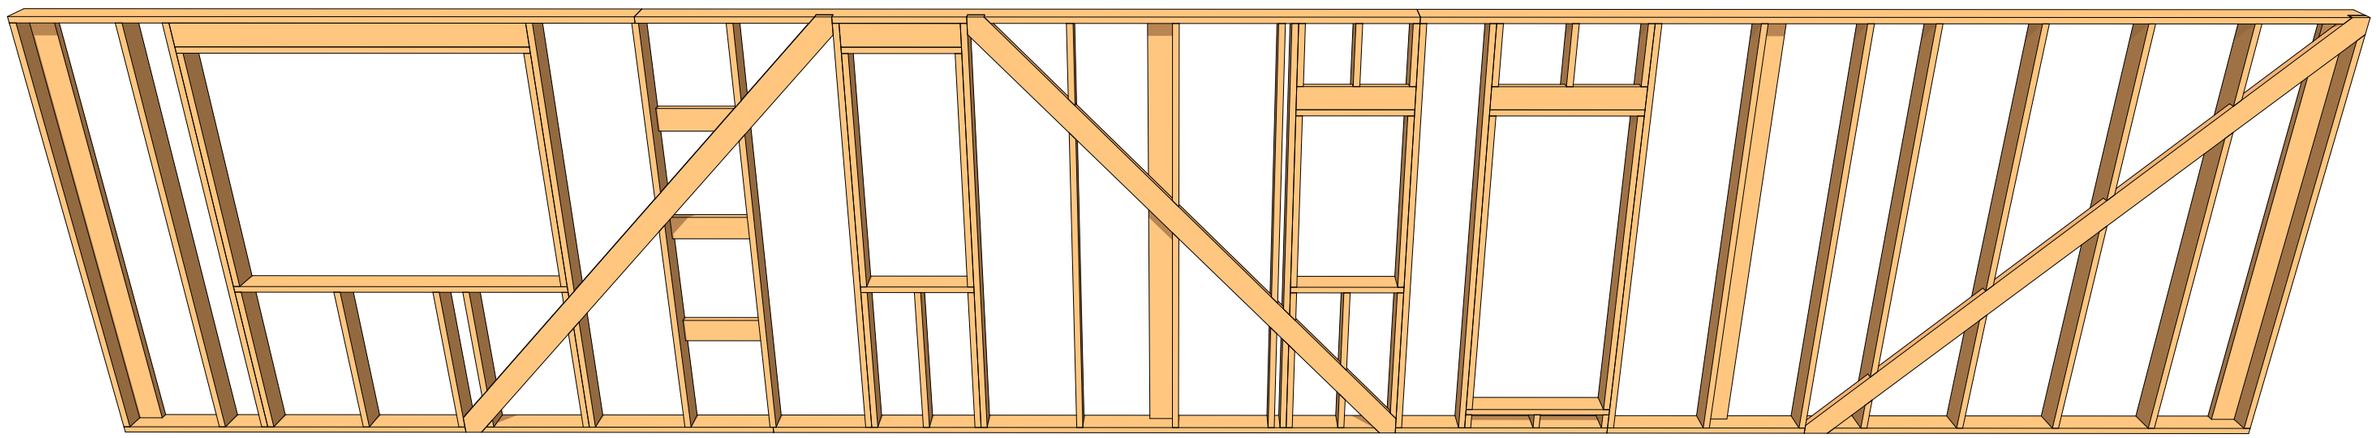


					Стена Ст-02	Лист
1				03/2026		14
Изм.	Лист	№ докум.	Подпись	Дата		

Стена Ст-02: спецификация

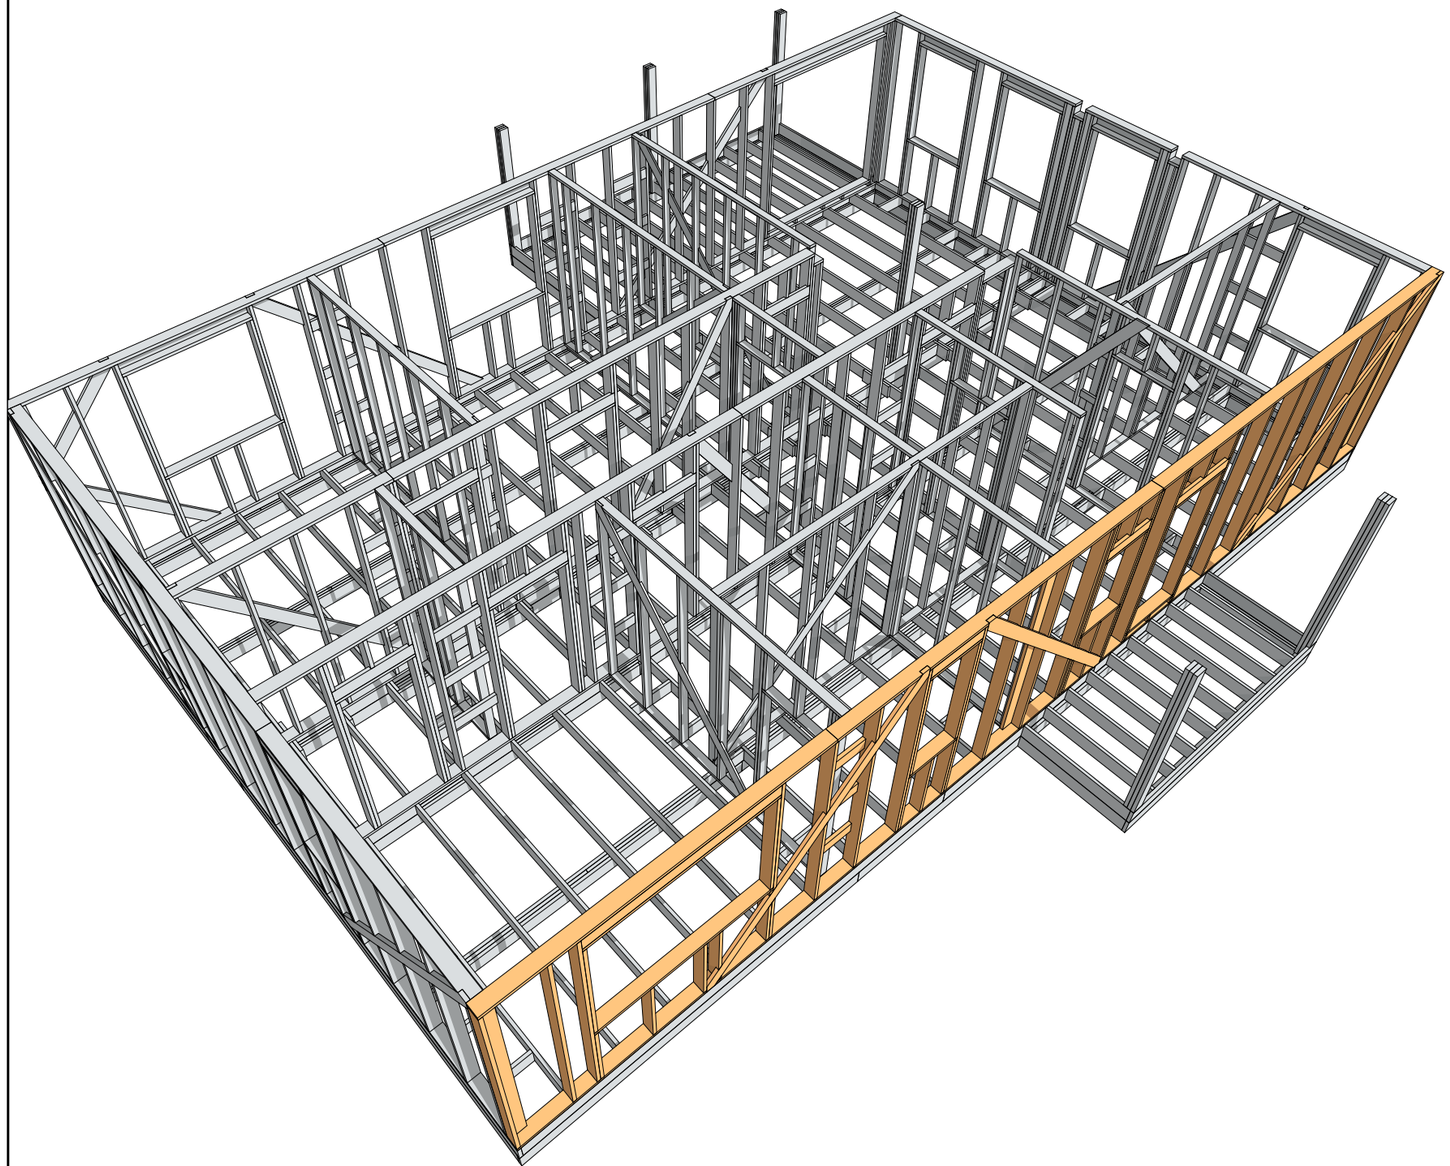

КД Спецификация деревянных элементов стены Ст-02				
Сечение	Марка	Длина	Кол-во	Объем
40х150				
	В-018	100	3	0,002
	В-035	521	3	0,009
	В-019	550	6	0,018
	В-041	720	4	0,017
	В-040	720	2	0,009
	В-048	940	2	0,011
	В-047	940	1	0,006
	В-021	1 000	11	0,064
	В-022	1 170	2	0,014
	В-023	1 570	4	0,038
	В-024	2 070	2	0,025
	В-079	2 120	2	0,025
	В-078	2 120	2	0,025
	В-028	2 800	26	0,433
	В-112	3 719	1	0,022
	В-087	4 071	1	0,023
	В-090	4 101	1	0,023
	В-118	4 227	1	0,025
	В-120	4 280	1	0,025
	В-094	4 289	1	0,024
	В-122	4 660	1	0,028
	В-133	5 494	1	0,033
	В-136	5 621	1	0,034
				0,934 м³


Стена Ст-03

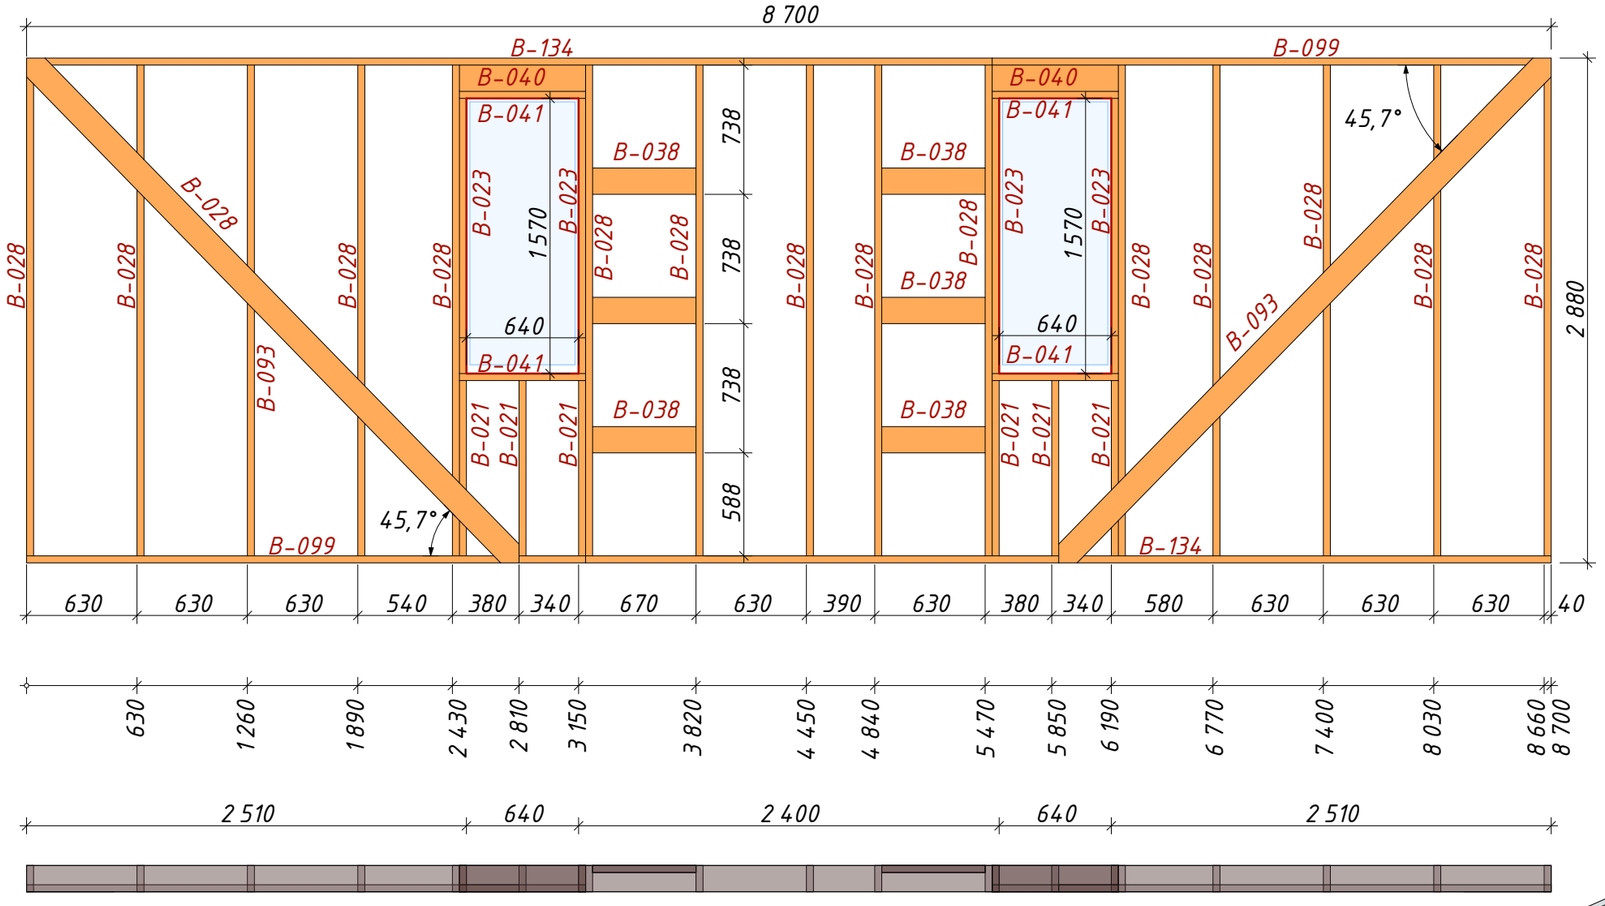


Ст-03

КД Спецификация деревянных элементов стены Ст-03

Сечение	Марка	Длина	Кол-во	Объем
40х150				
	В-038	590	6	0,021
	В-041	720	4	0,017
	В-040	720	2	0,009
	В-021	1 000	6	0,035
	В-023	1 570	4	0,038
	В-028	2 800	15	0,249
	В-099	3 190	2	0,038
	В-093	4 177	2	0,047
	В-134	5 510	2	0,066
				0,520 м³

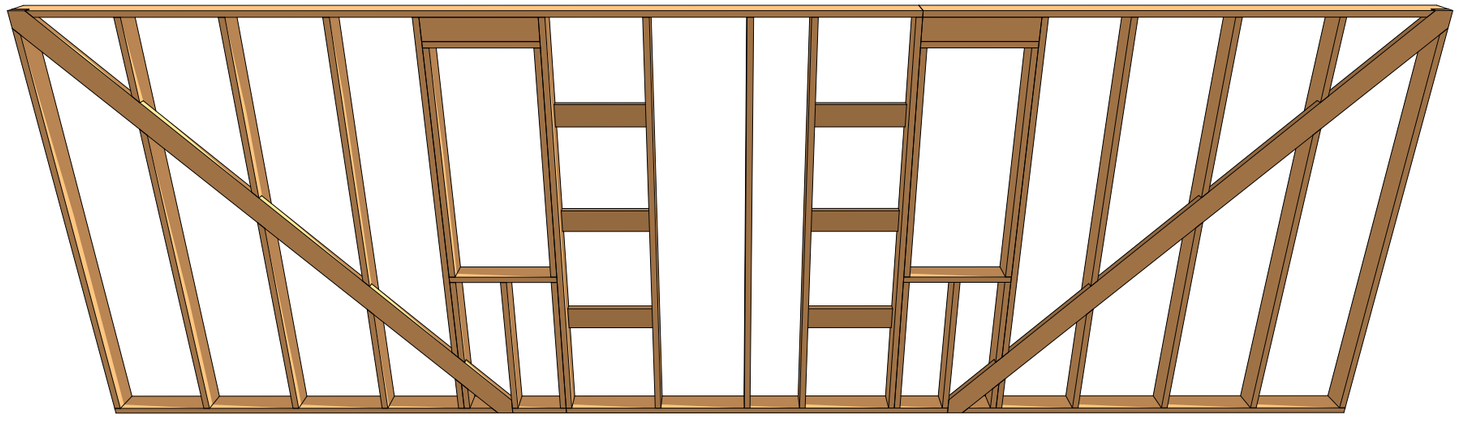

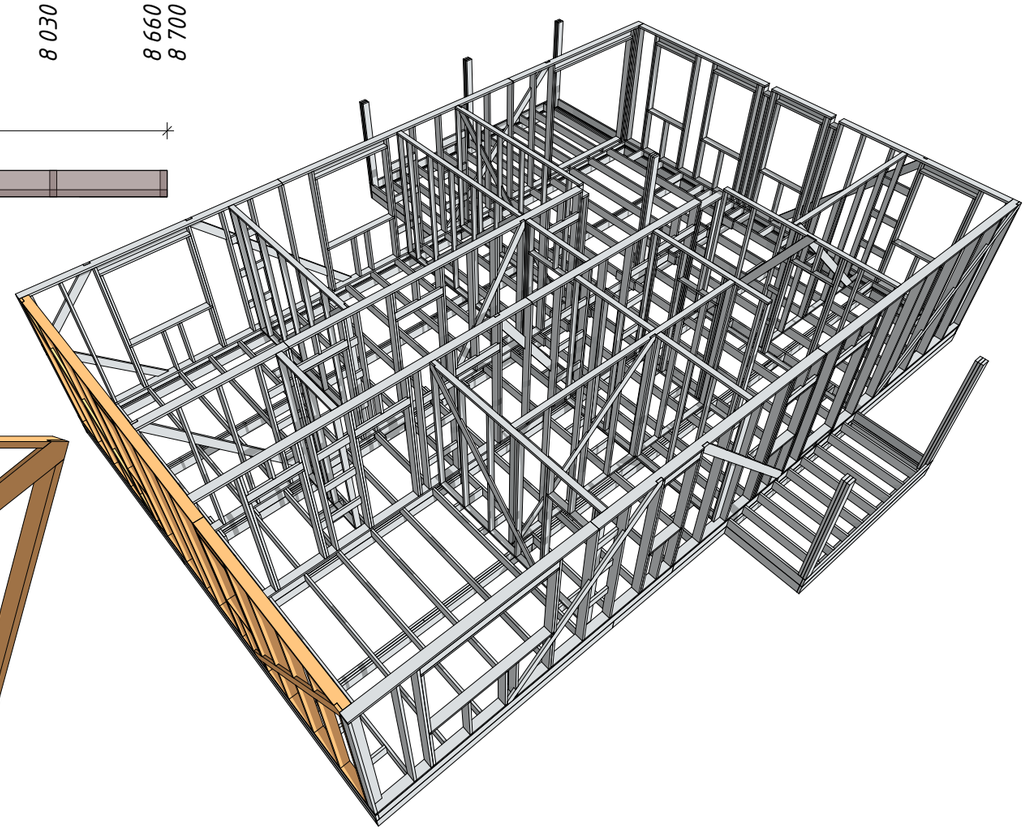


1				03/2026	Стена Ст-03
Изм.	Лист	№ докум.	Подпись	Дата	Лист 16

Стена Ст-04



					Стена Ст-04	Лист
1				03/2026		17
Изм.	Лист	№ докум.	Подпись	Дата		

Стена Ст-04: спецификация

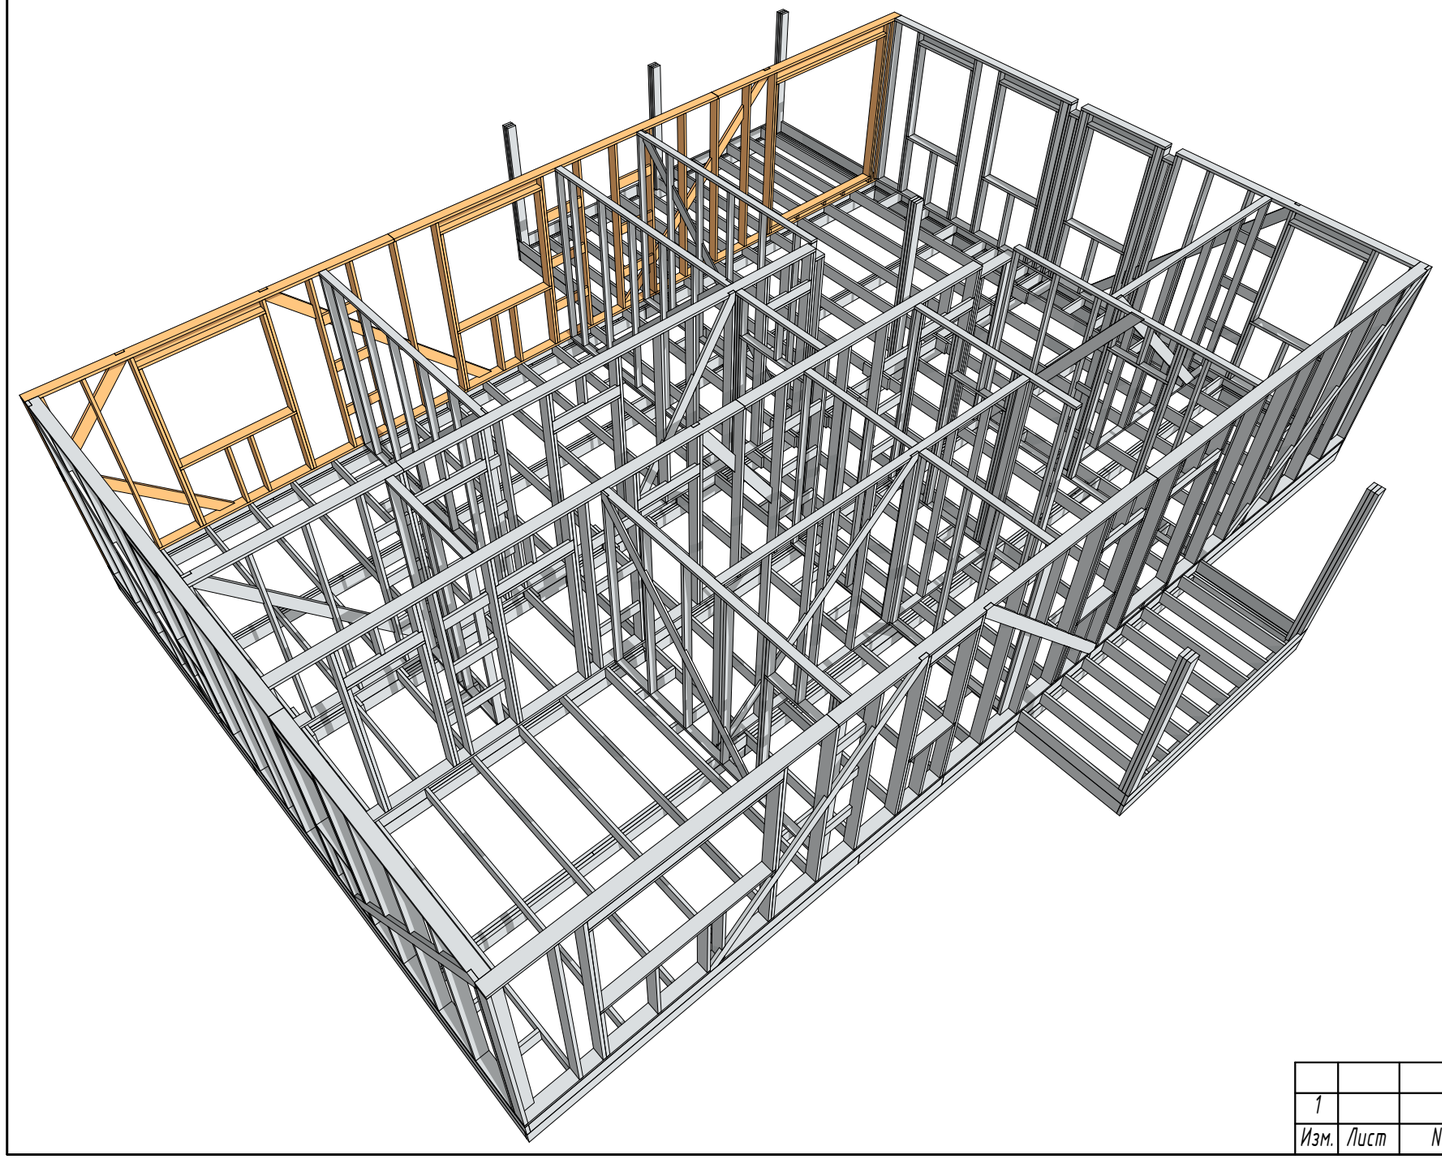


КД Спецификация деревянных элементов стены Ст-04				
Сечение	Марка	Длина	Кол-во	Объем
40х150				
	В-017	70	5	0,002
	В-036	525	3	0,009
	В-038	590	6	0,021
	В-021	1 000	8	0,047
	В-023	1 570	4	0,038
	В-072	1 620	4	0,039
	В-071	1 620	2	0,019
	В-058	1 845	1	0,010
	В-083	2 380	2	0,029
	В-082	2 380	2	0,029
	В-026	2 500	2	0,030
	В-073	2 672	1	0,014
	В-028	2 800	20	0,332
	В-107	3 530	1	0,021
	В-114	3 856	1	0,023
	В-095	4 376	2	0,048
	В-123	4 704	1	0,028
	В-126	5 116	1	0,031
	В-131	5 354	1	0,032
	В-132	5 440	1	0,033
				0,834 м³

Стена Ст-05




▲Ст-05

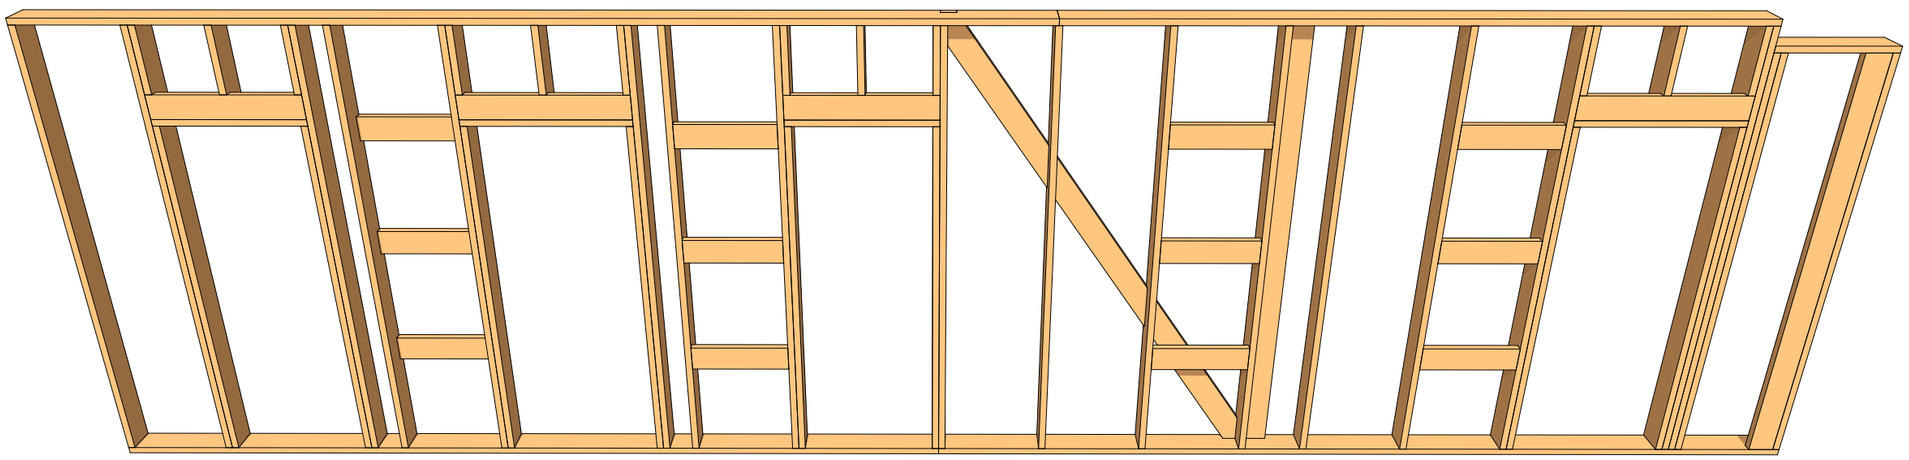


1				03/2026	Стена Ст-05	Лист 19
Изм.	Лист	№ докум.	Подпись	Дата		


Стена Ст-05: спецификация

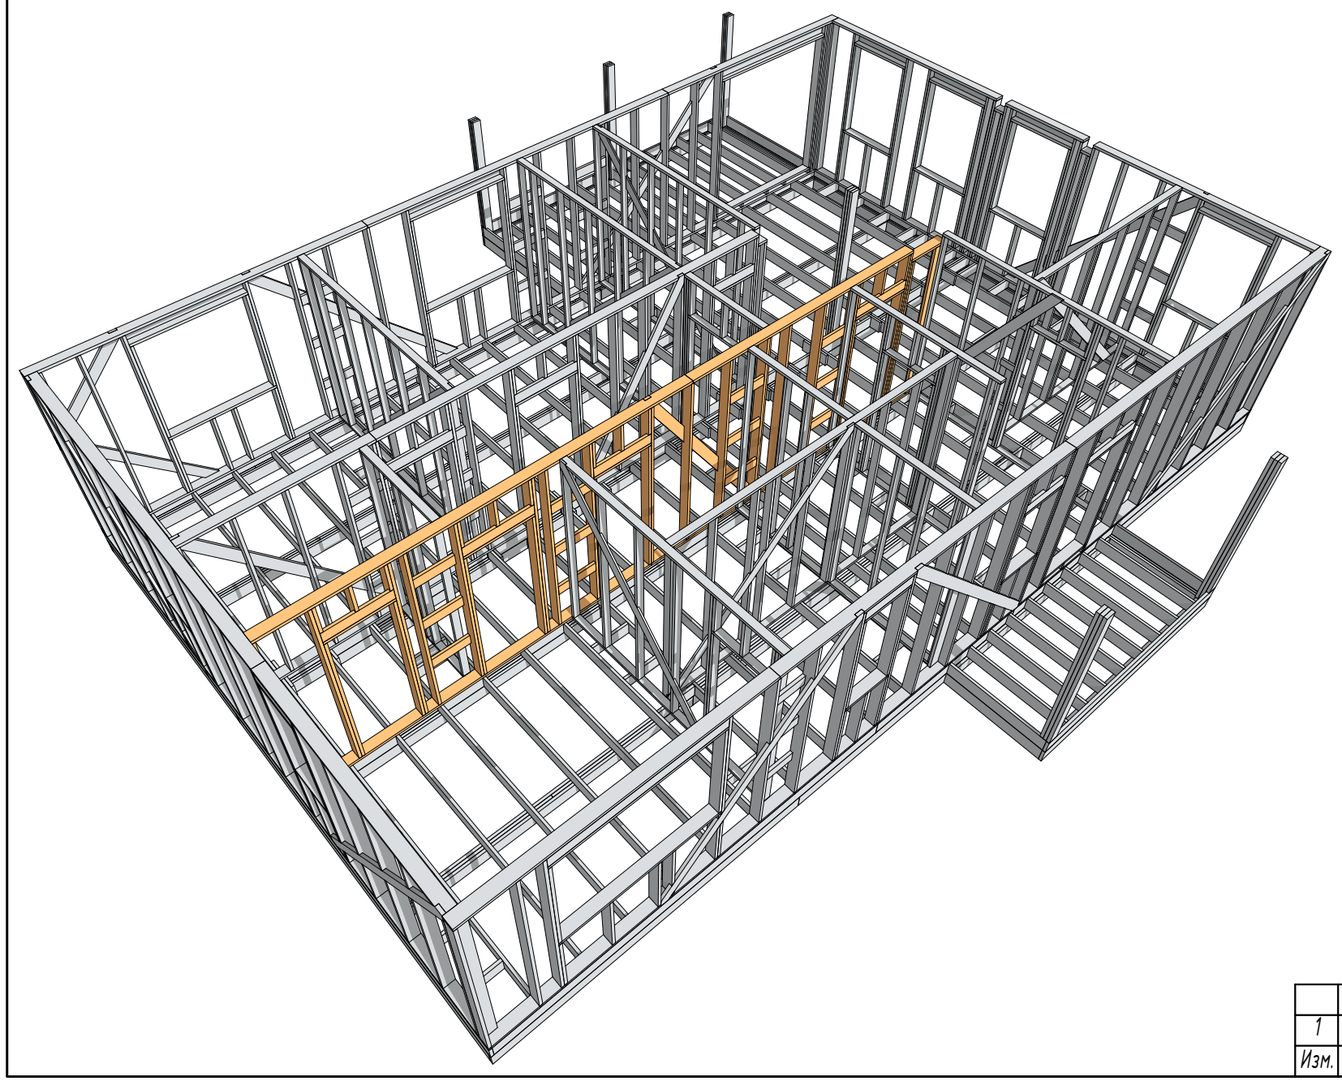


КД Спецификация деревянных элементов стены Ст-05				
Сечение	Марка	Длина	Кол-во	Объем
40x150				
	В-020	560	12	0,037
	В-038	590	12	0,042
	В-039	697	1	0,004
	В-046	880	2	0,011
	В-045	880	2	0,011
	В-050	980	2	0,012
	В-049	980	2	0,012
	В-025	2 200	8	0,106
	В-027	2 645	4	0,063
	В-028	2 800	17	0,284
	В-077	3 692	1	0,020
	В-116	3 943	1	0,024
	В-125	5 110	1	0,031
	В-130	5 290	1	0,032
	В-139	5 760	1	0,034
				0,723 м³

Стена Ст-06

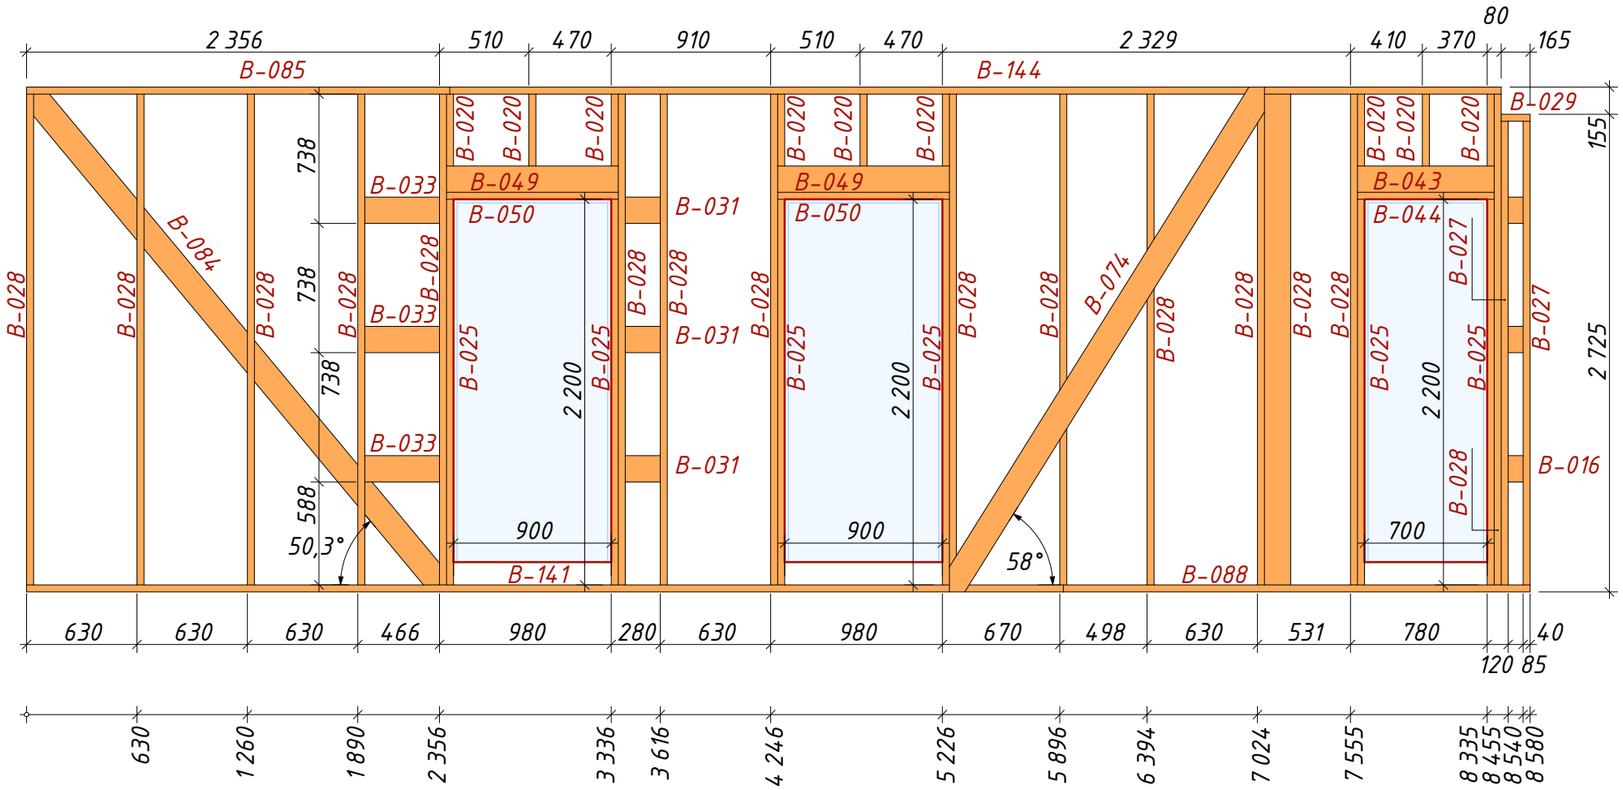


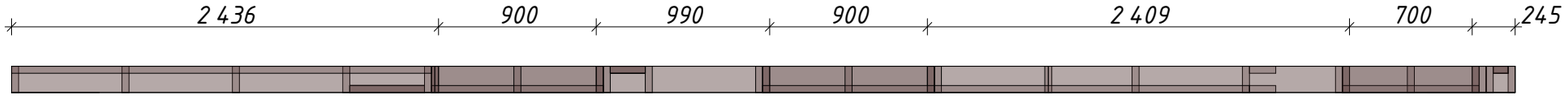

Ст-06▲

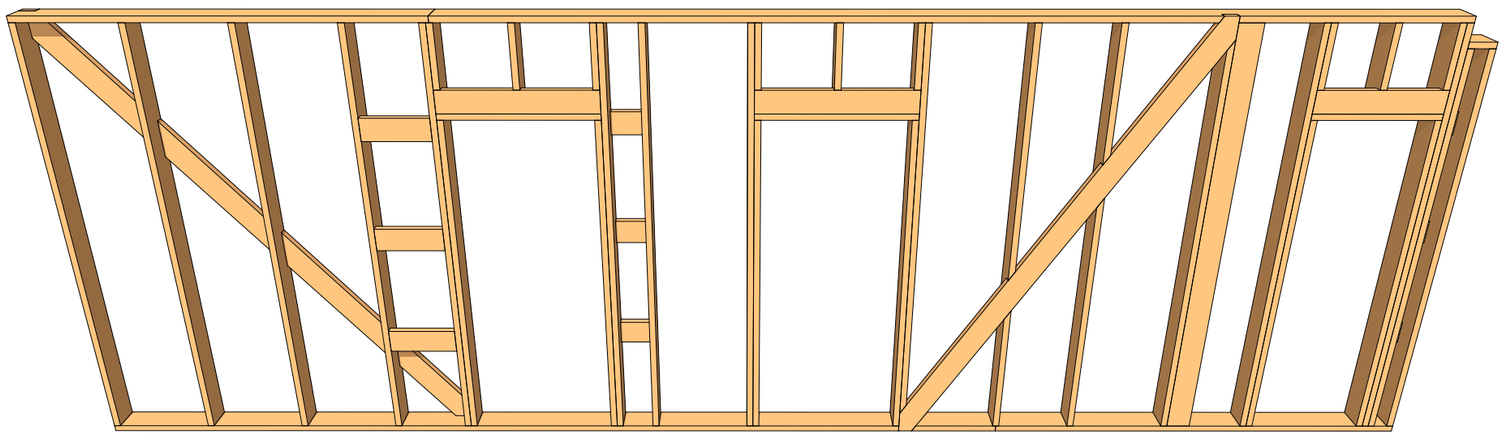



КД Спецификация деревянных элементов стены Ст-06				
Сечение	Марка	Длина	Кол-во	Объем
40x150				
	В-016	85	3	0,002
	В-029	165	1	0,001
	В-031	200	3	0,004
	В-033	426	3	0,008
	В-020	560	9	0,028
	В-044	780	1	0,005
	В-043	780	1	0,005
	В-050	980	2	0,012
	В-049	980	2	0,012
	В-025	2 200	6	0,079
	В-085	2 415	1	0,014
	В-027	2 645	2	0,032
	В-088	2 664	1	0,016
	В-028	2 800	16	0,266
	В-074	3 635	1	0,020
	В-084	3 928	1	0,022
	В-141	5 916	1	0,035
	В-144	6 000	1	0,036
				0,595 м³

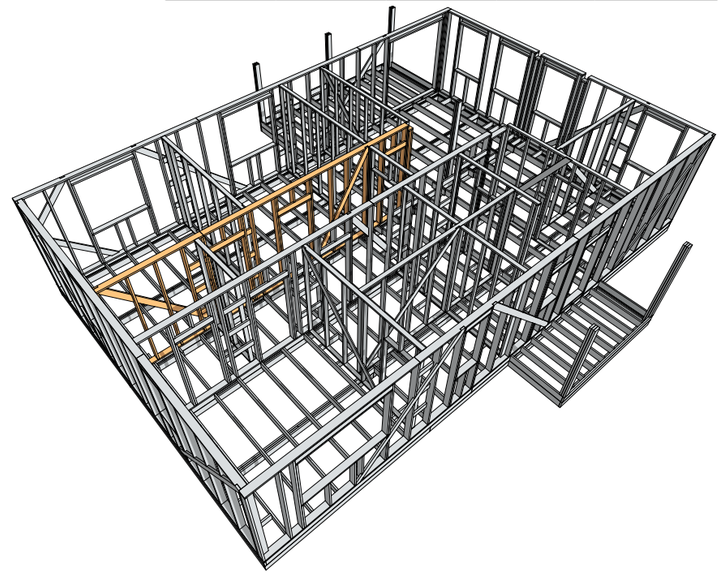


Изм.	Лист	№ докум.	Подпись	Дата	Стена Ст-06	Лист
1				03/2026		21

Стена Ст-07

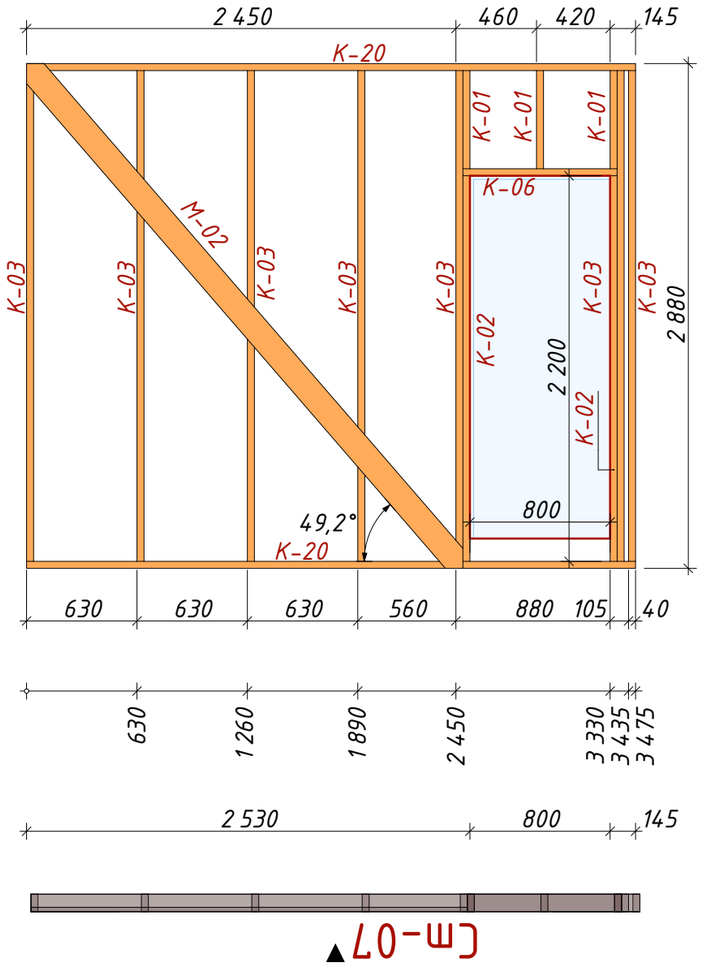

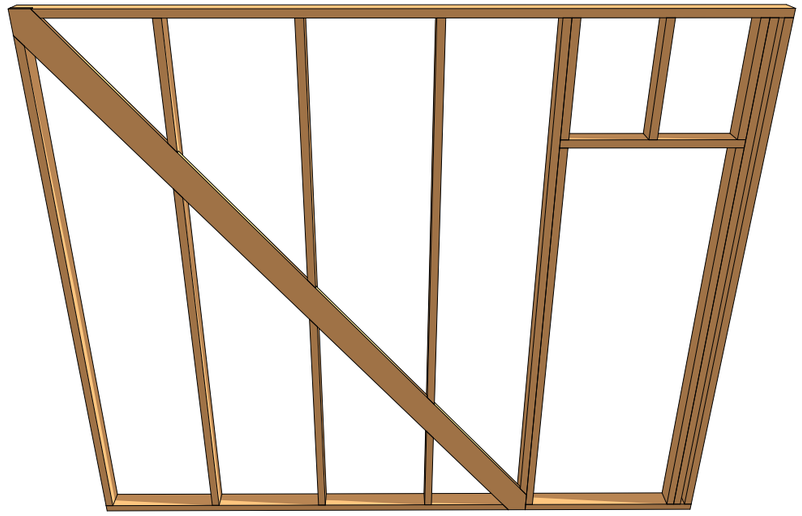


КД Спецификация деревянных элементов стены Ст-07				
Сечение	Марка	Длина	Кол-во	Объем
25х150				
	М-02	3 981	1	0,014
				0,014 м³
40х100				
	К-01	560	3	0,007
	К-06	880	1	0,004
	К-02	2 200	2	0,018
	К-03	2 800	7	0,078
	К-20	3 475	2	0,028
				0,133 м³
				0,147 м³

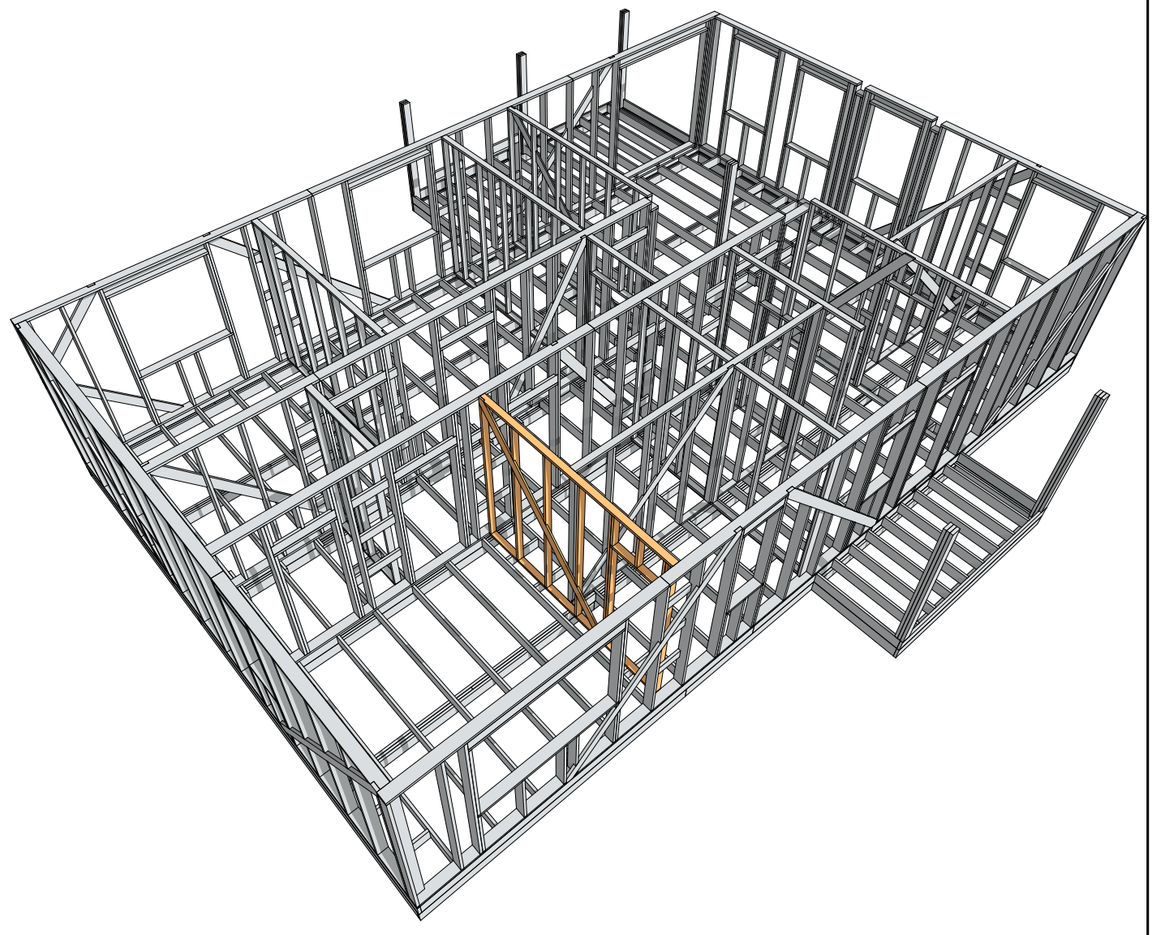


						Лист
1				03/2026	Стена Ст-07	22
Изм.	Лист	№ докум.	Подпись	Дата		

Стена Ст-08

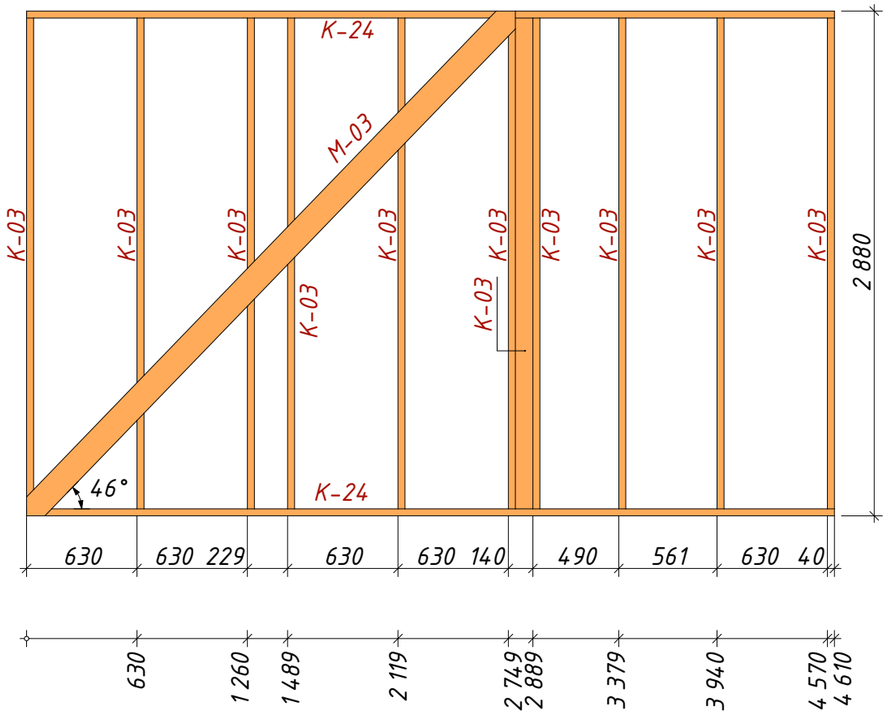




Ст-08

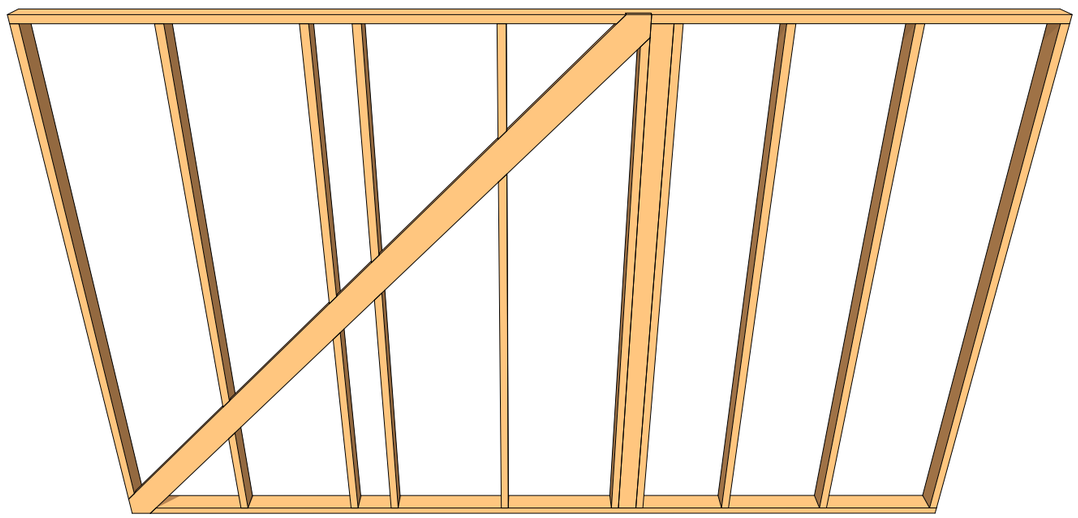


КД Спецификация деревянных элементов стены Ст-08


Сечение	Марка	Длина	Кол-во	Объем
25х150				
	М-03	4 169	1	0,015
				0,015 м³
40х100				
	К-03	2 800	12	0,133
	К-24	4 610	2	0,037
				0,170 м³
				0,185 м³

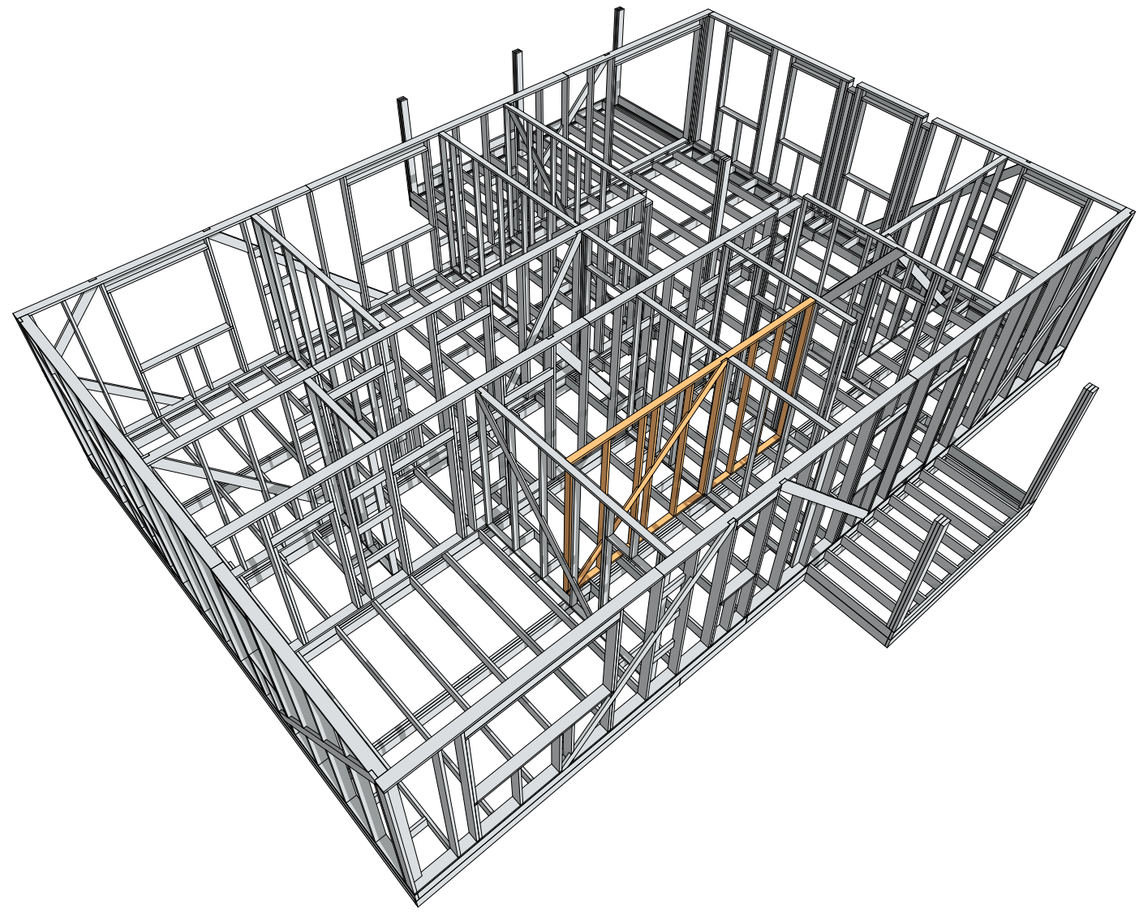

1				03/2026	Стена Ст-08	Лист 23
Изм.	Лист	№ докум.	Подпись	Дата		


Стена Ст-09

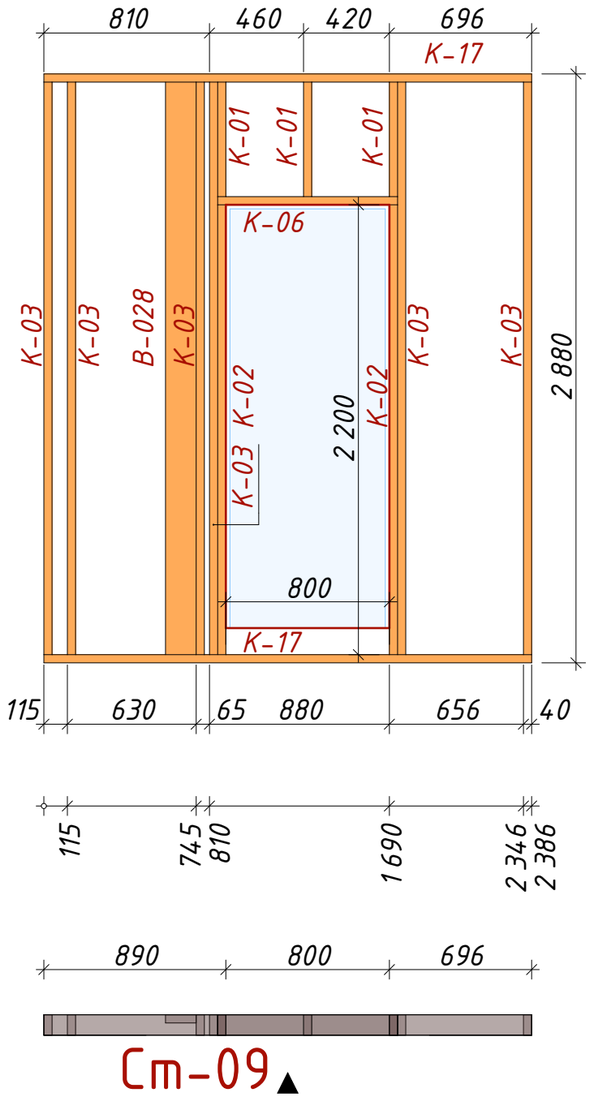

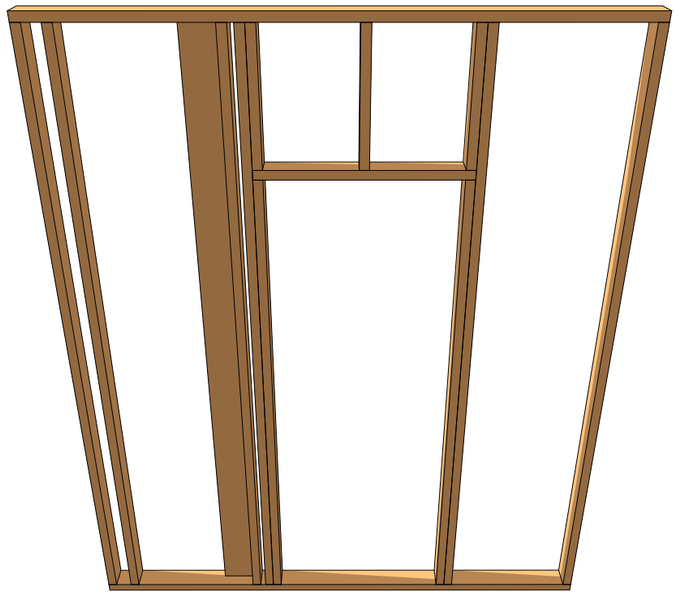


КД Спецификация деревянных элементов стены Ст-09


Сечение	Марка	Длина	Кол-во	Объем
40х100				
	К-01	560	3	0,007
	К-06	880	1	0,004
	К-02	2 200	2	0,018
	К-17	2 386	2	0,019
	К-03	2 800	6	0,067
				0,114 м³
40х150				
	В-028	2 800	1	0,017
				0,017 м³
				0,131 м³

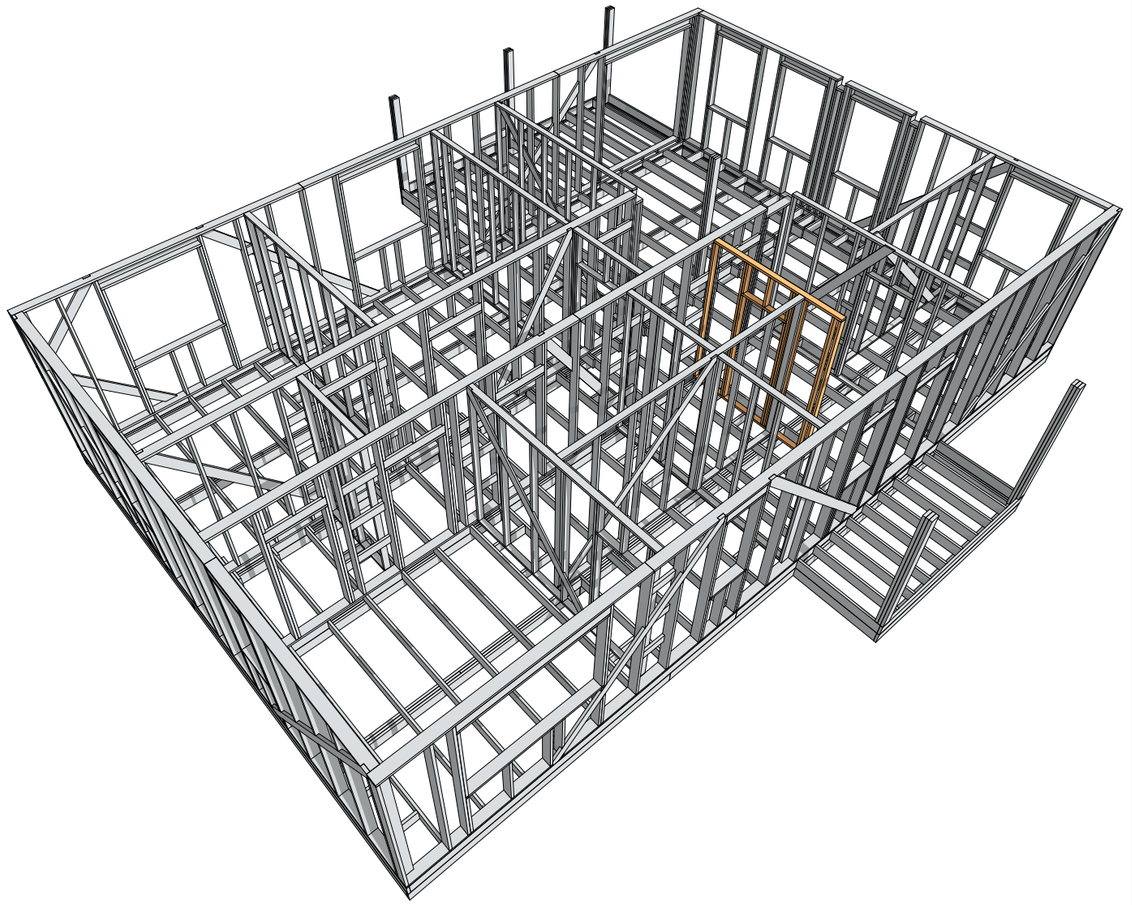


						Лист
1				03/2026	Стена Ст-09	24
Изм.	Лист	№ докум.	Подпись	Дата		

Стена Ст-10

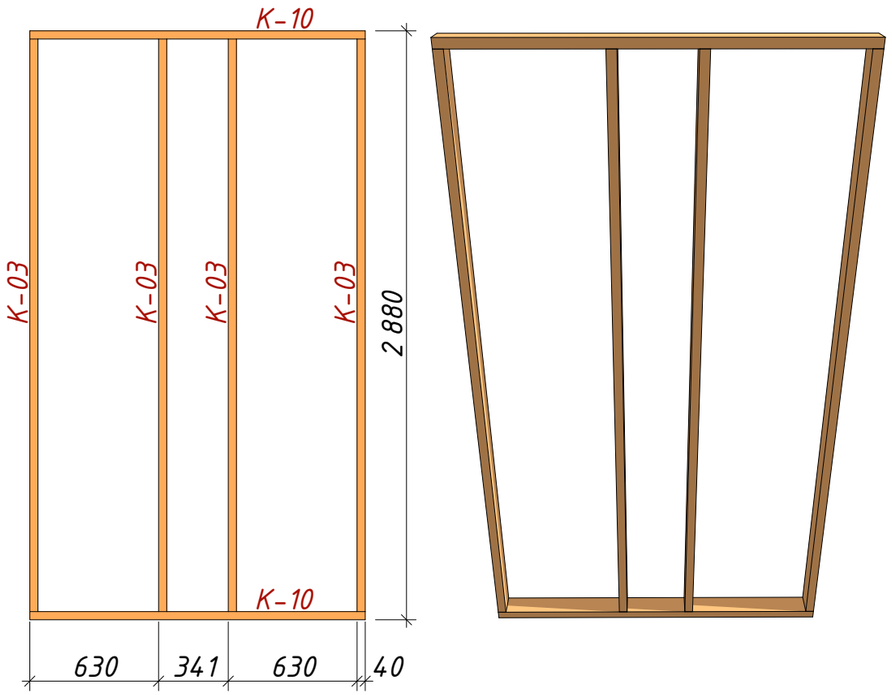

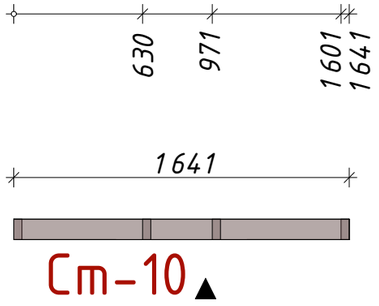


КД Спецификация деревянных элементов стены Ст-10				
Сечение	Марка	Длина	Кол-во	Объем
40х100				
	К-10	1 641	2	0,013
	К-03	2 800	4	0,045
				0,058 м³

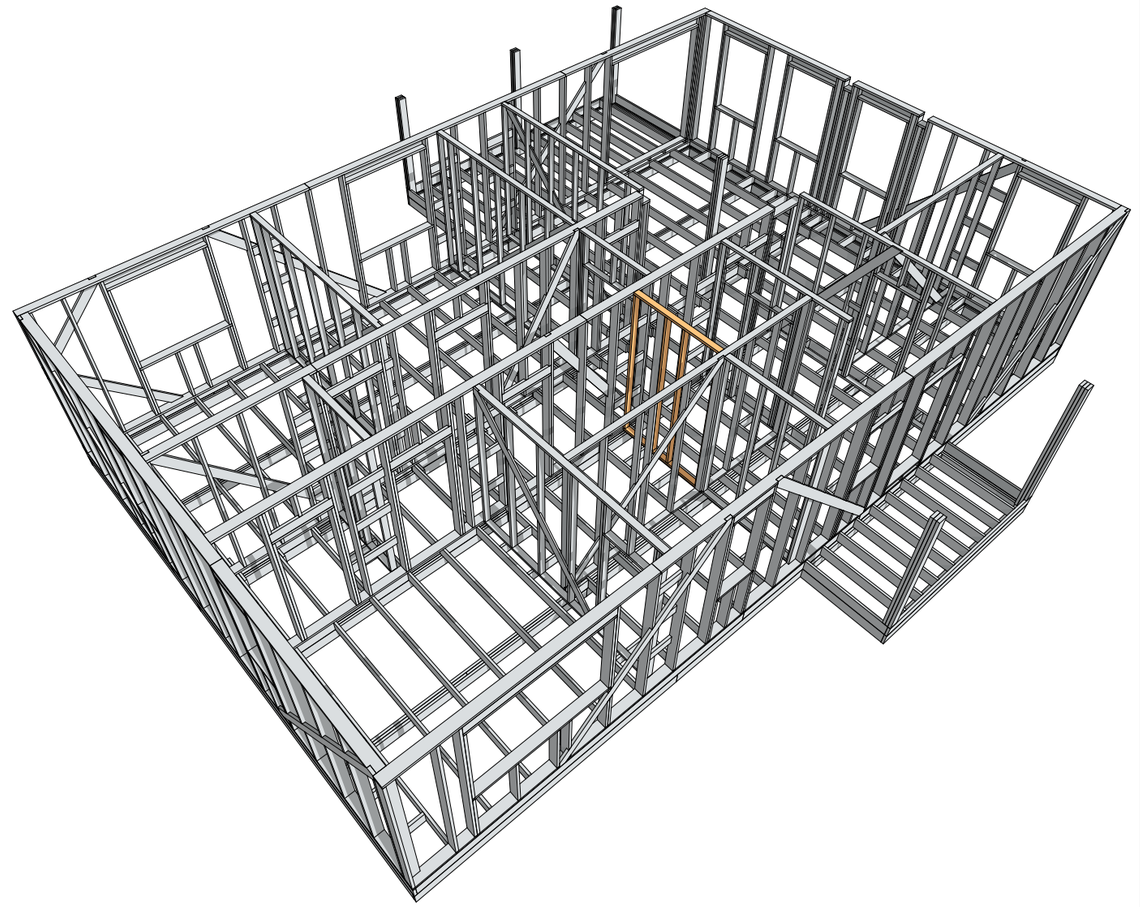


						Лист
1				03/2026	Стена Ст-10	25
Изм.	Лист	№ докум.	Подпись	Дата		

Стена Ст-11

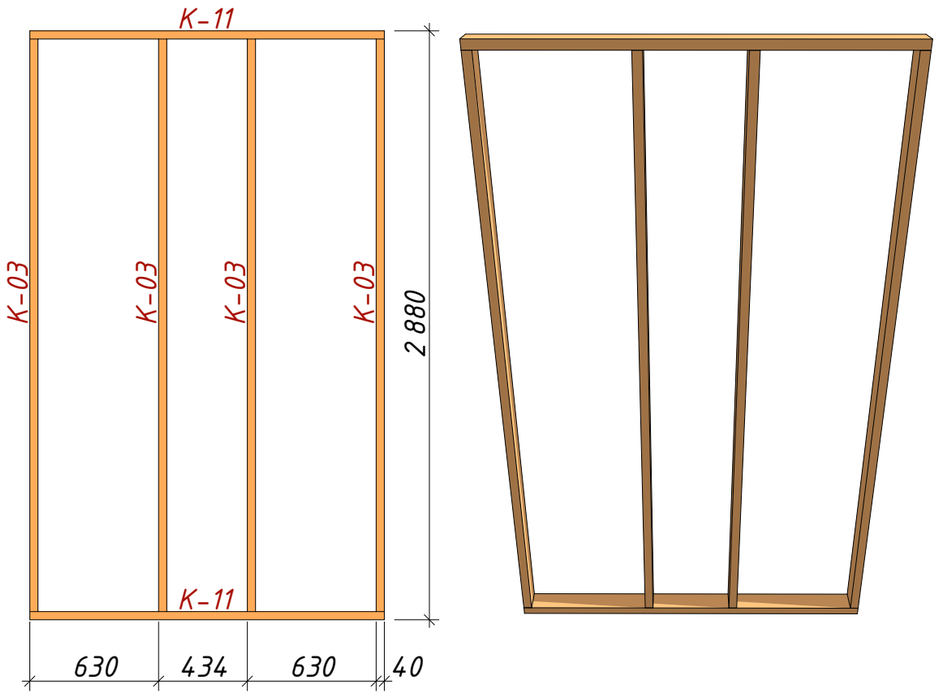



КД Спецификация деревянных элементов стены Ст-11				
Сечение	Марка	Длина	Кол-во	Объем
40х100				
	К-11	1 734	2	0,014
	К-03	2 800	4	0,045
				0,059 м³

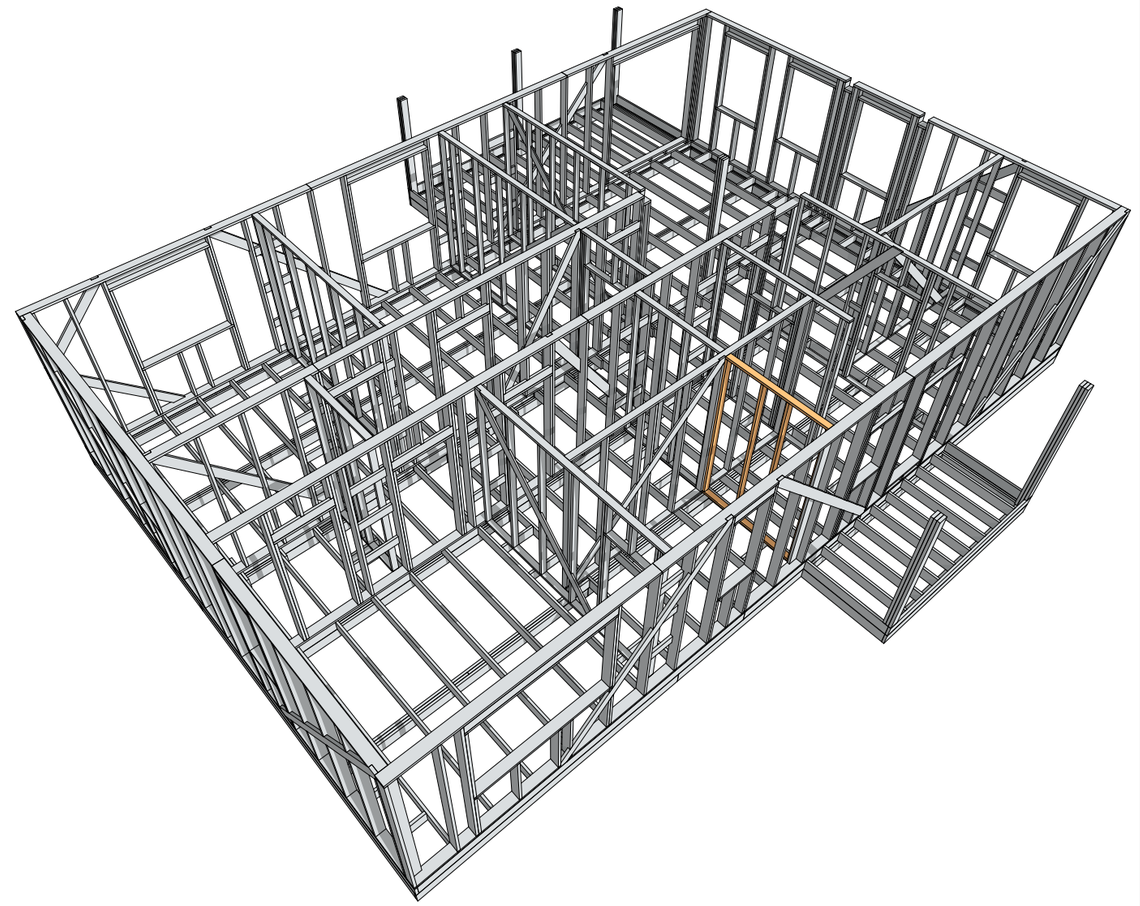

						Лист
1				03/2026	Стена Ст-11	26
Изм.	Лист	№ докум.	Подпись	Дата		


Стена Ст-12

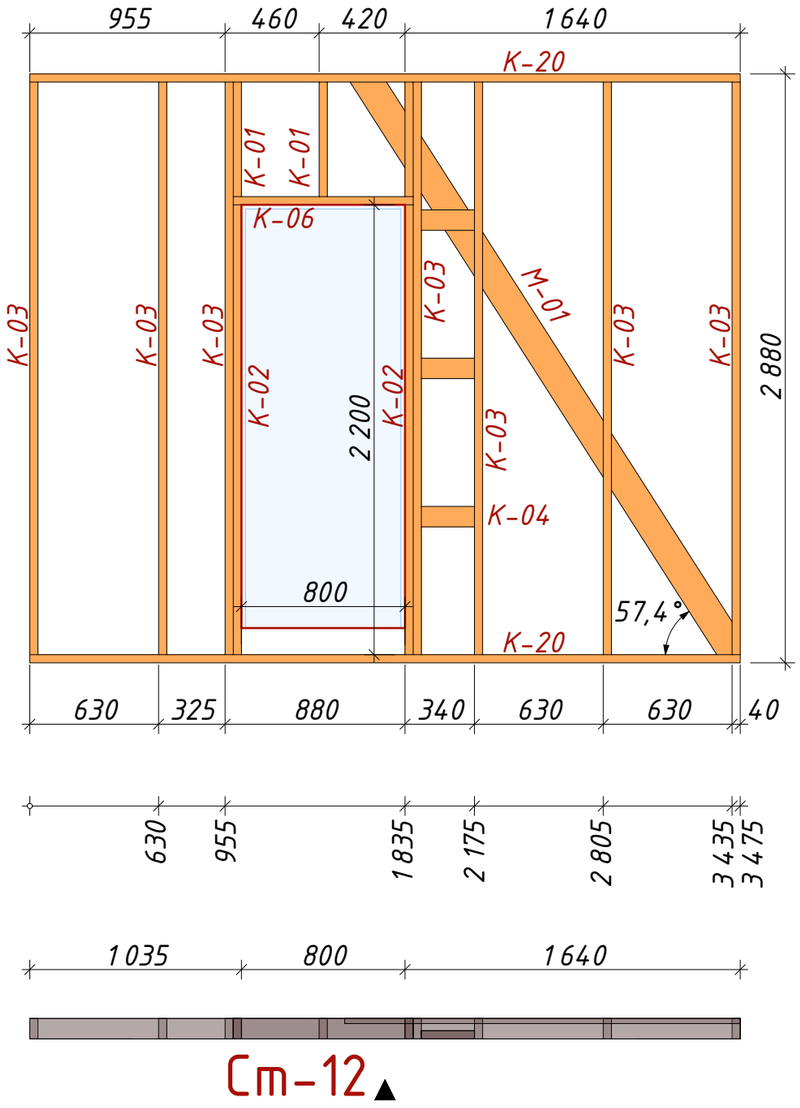

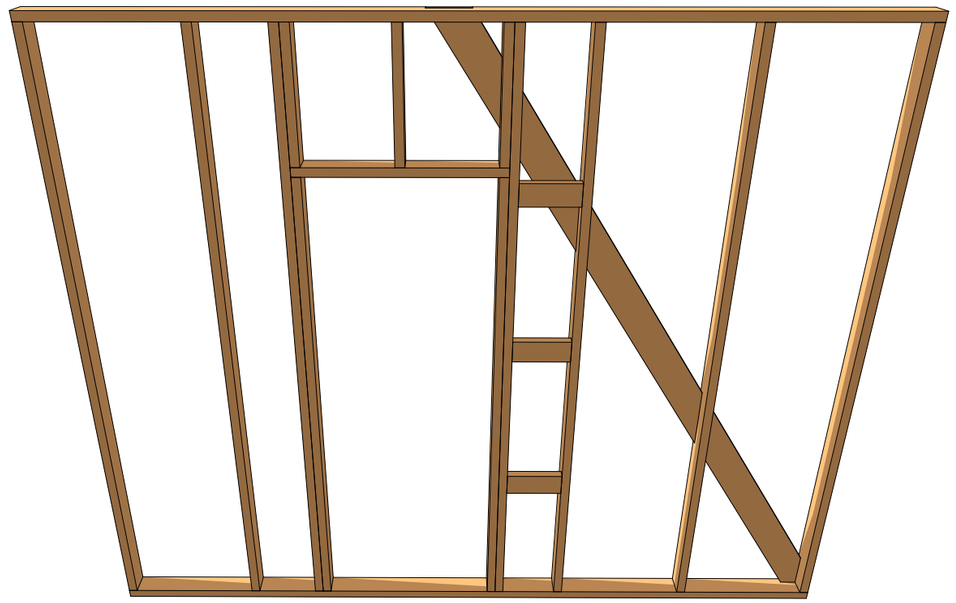


КД Спецификация деревянных элементов стены Ст-12


Сечение	Марка	Длина	Кол-во	Объем
25х150				
	М-01	3 821	1	0,013
				0,013 м³
40х100				
	К-04	260	3	0,003
	К-01	560	3	0,006
	К-06	880	1	0,004
	К-02	2 200	2	0,018
	К-03	2 800	7	0,077
	К-20	3 475	2	0,028
				0,136 м³
				0,148 м³

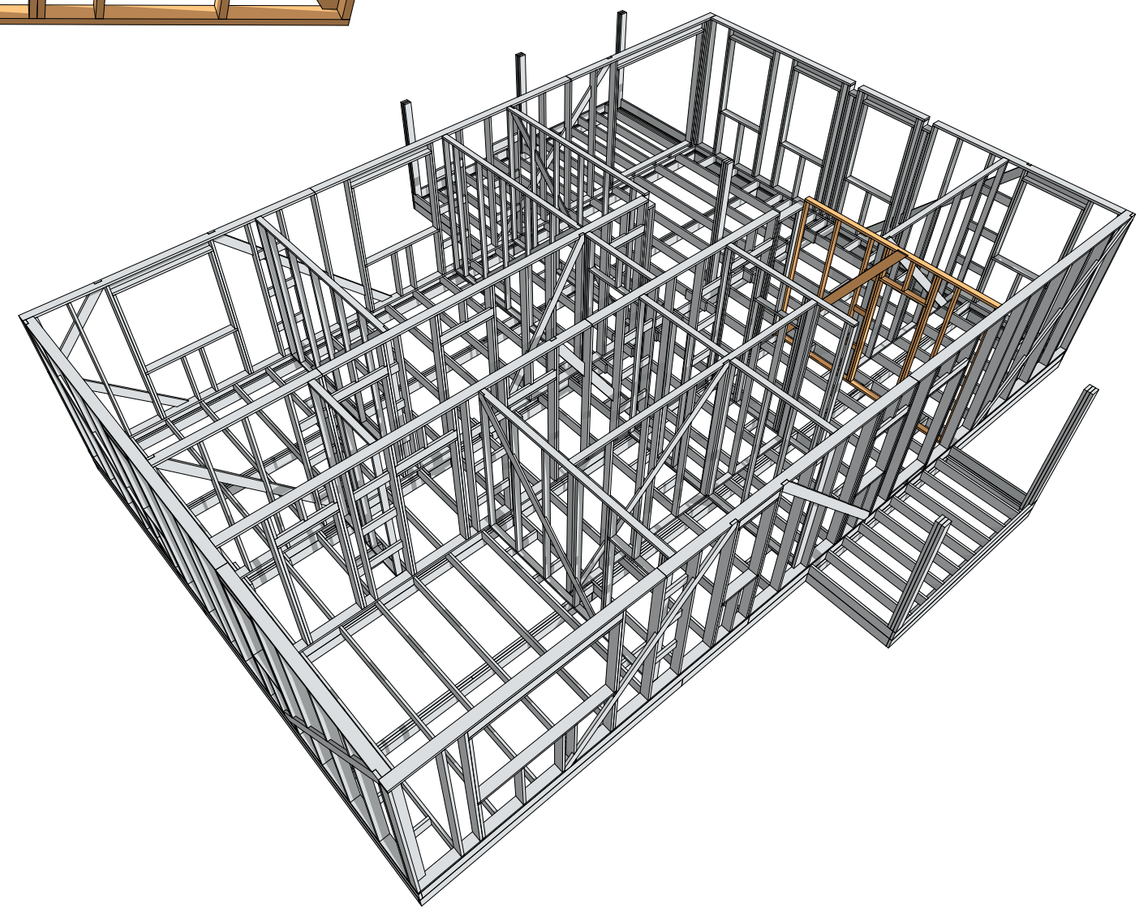

						Лист
1				03/2026	Стена Ст-12	27
Изм.	Лист	№ докум.	Подпись	Дата		


Стена Ст-13

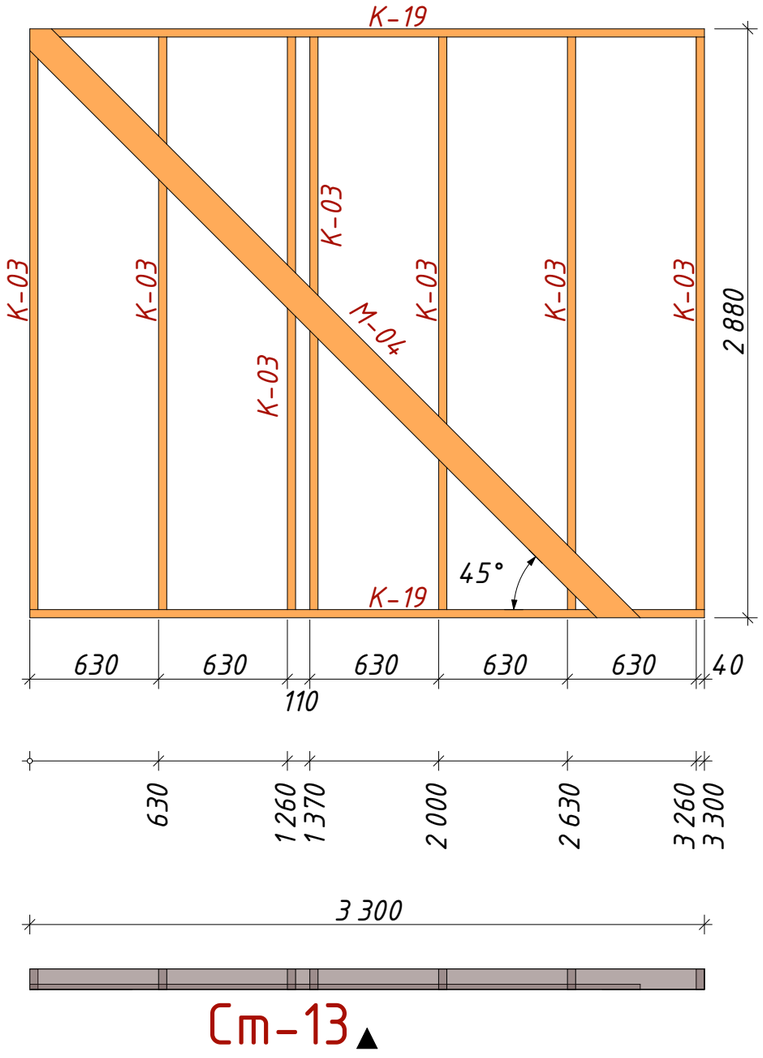

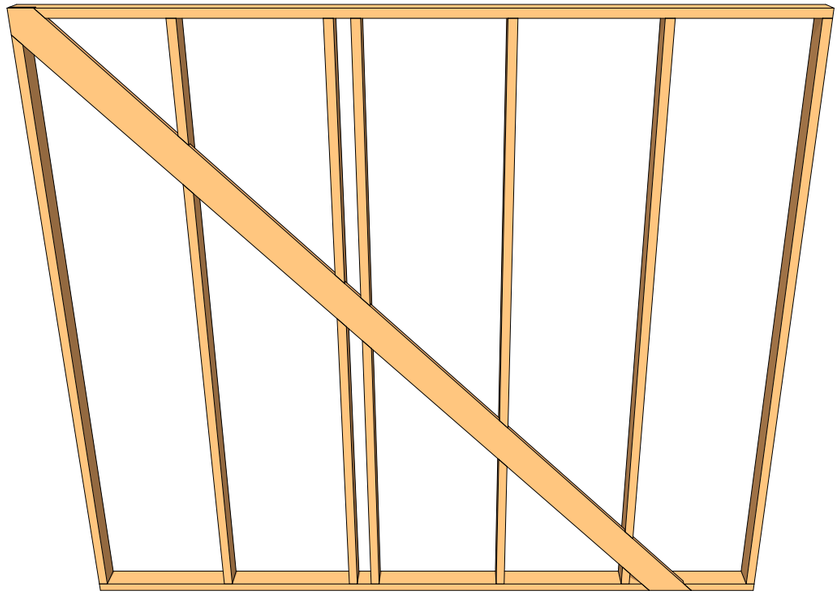


КД Спецификация деревянных элементов стены Ст-13

Сечение	Марка	Длина	Кол-во	Объем
25х150				
	М-04	4 373	1	0,015
				0,015 м³
40х100				
	К-03	2 800	7	0,077
	К-19	3 300	2	0,026
				0,103 м³
				0,118 м³

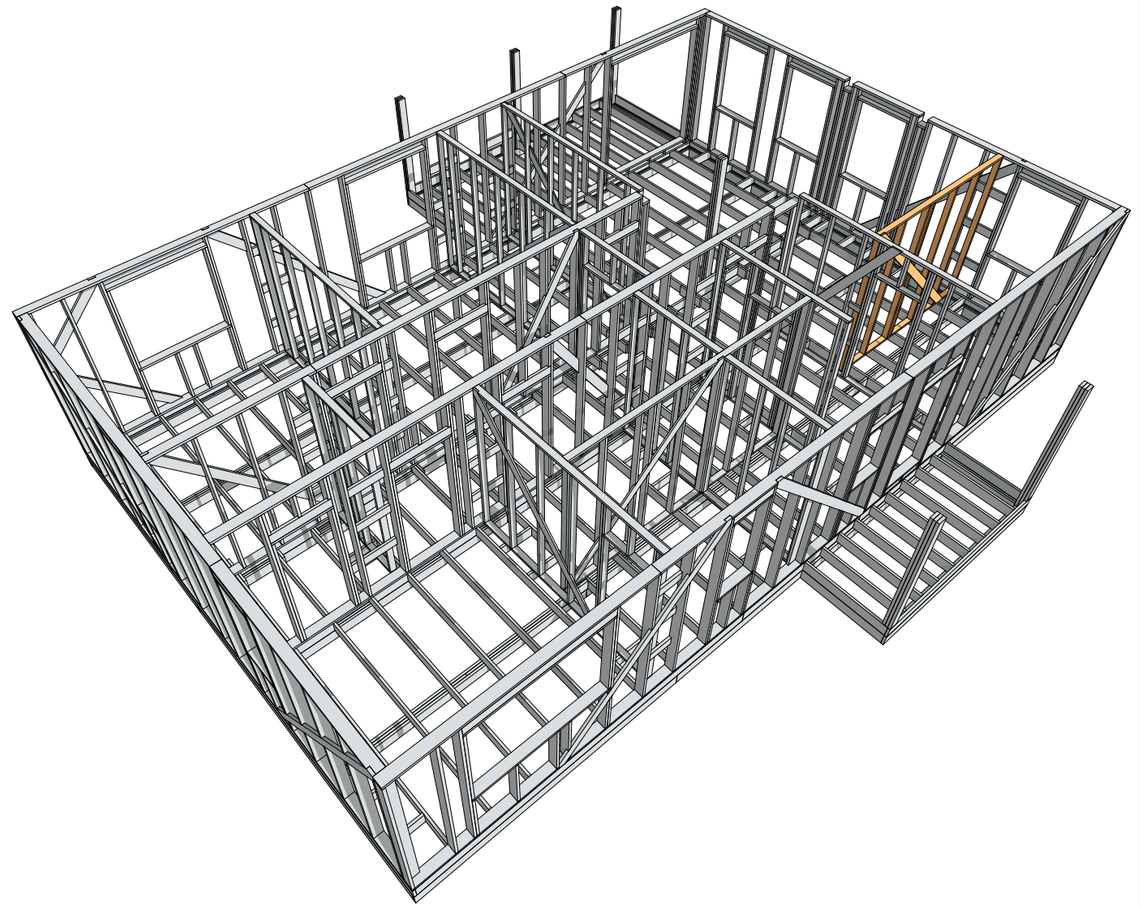

					Стена Ст-13	Лист
1				03/2026		28
Изм.	Лист	№ докум.	Подпись	Дата		

Стена Ст-14

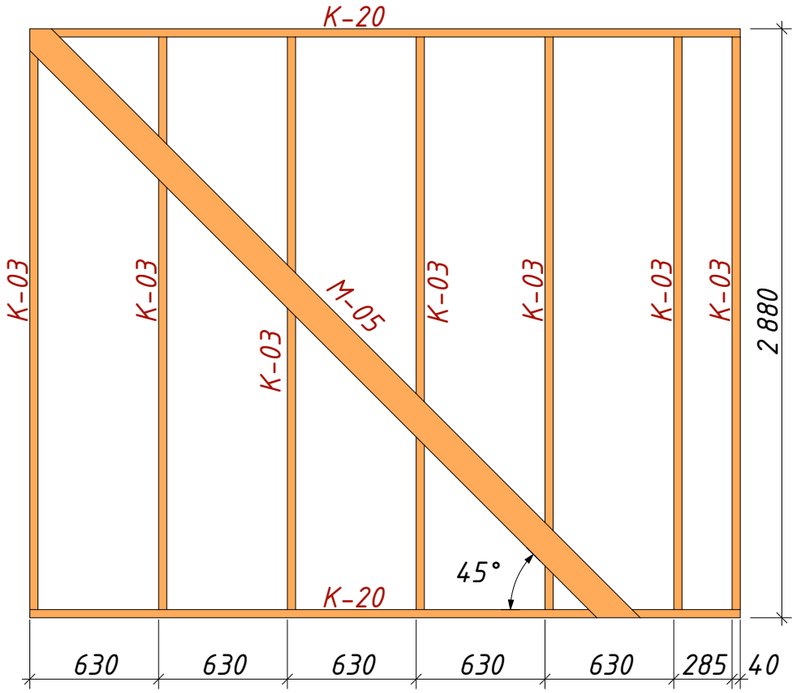


Ст-14




КД Спецификация деревянных элементов стены Ст-14

Сечение	Марка	Длина	Кол-во	Объем
25х150				
	М-05	4 374	1	0,015
				0,015 м³
40х100				
	К-03	2 800	7	0,077
	К-20	3 475	2	0,027
				0,105 м³
				0,120 м³

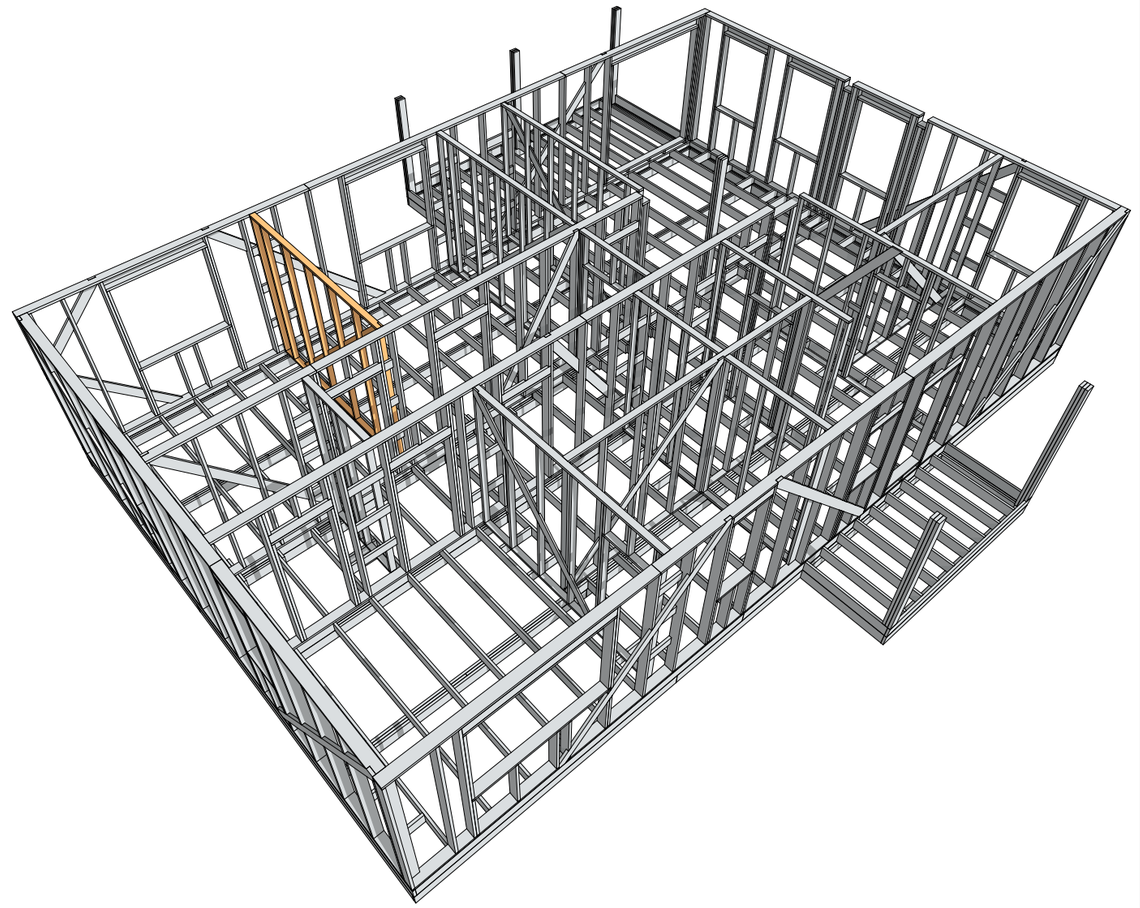


						Лист
1				03/2026	Стена Ст-14	29
Изм.	Лист	№ докум.	Подпись	Дата		

Стена Ст-15

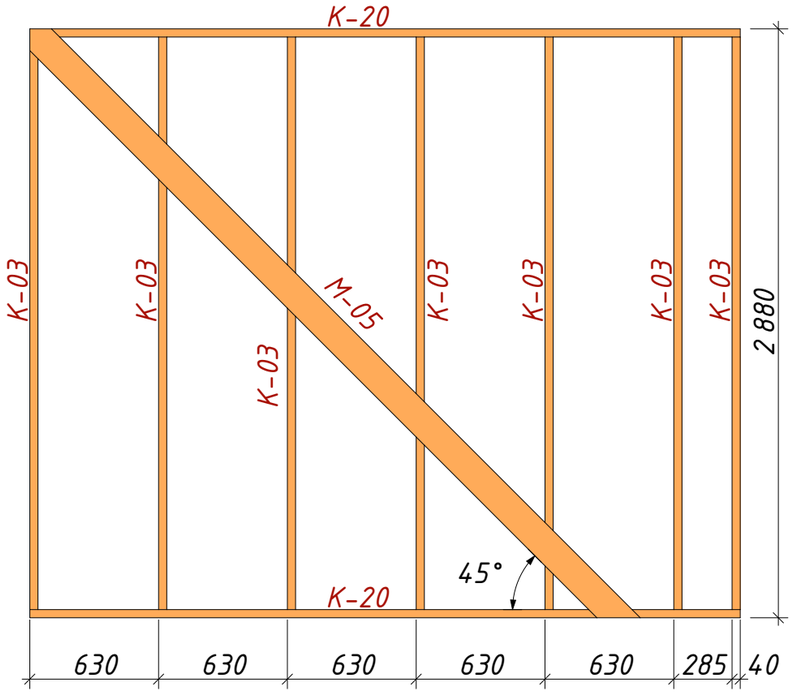


Ст-15

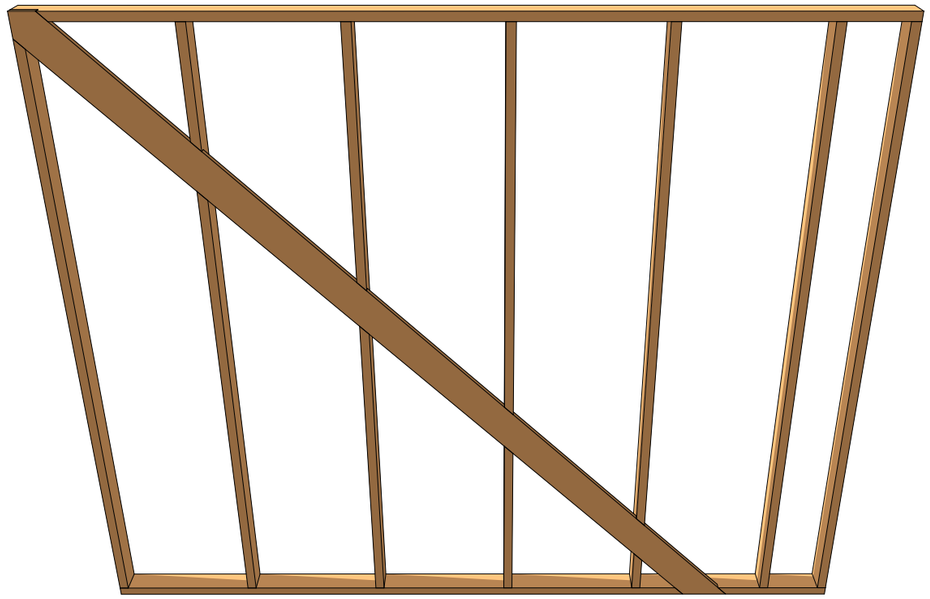


КД Спецификация деревянных элементов стены Ст-15

Сечение	Марка	Длина	Кол-во	Объем
25х150				
	М-05	4 374	1	0,015
				0,015 м³
40х100				
	К-03	2 800	7	0,077
	К-20	3 475	2	0,027
				0,105 м³
				0,120 м³

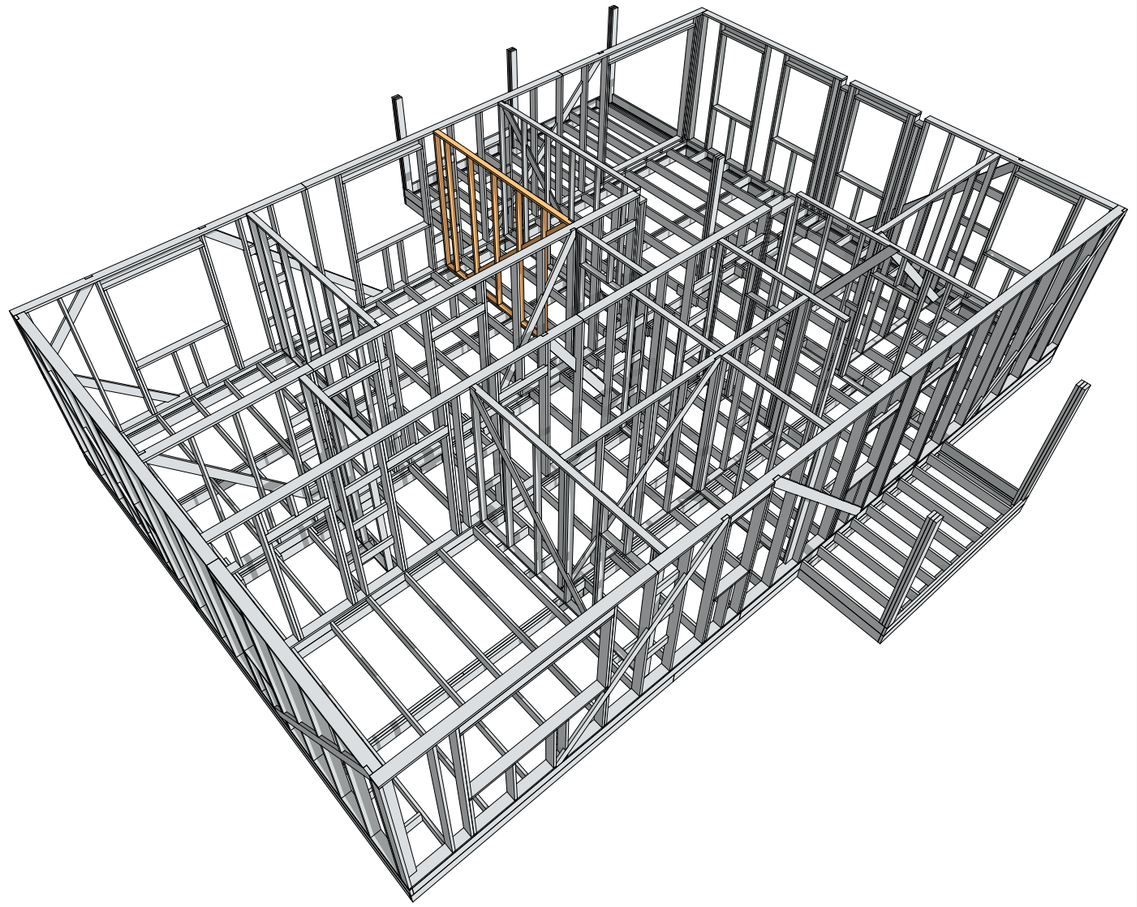

						Лист
1				03/2026	Стена Ст-15	30
Изм.	Лист	№ докум.	Подпись	Дата		

Стена Ст-16

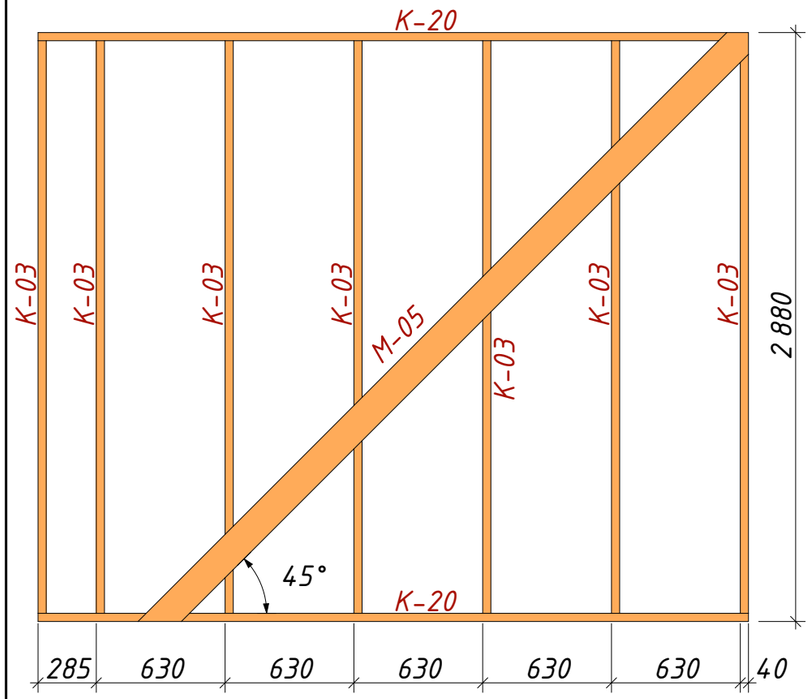


Ст-16




КД Спецификация деревянных элементов стены Ст-16

Сечение	Марка	Длина	Кол-во	Объем
25х150				
	М-05	4 374	1	0,015
				0,015 м³
40х100				
	К-03	2 800	7	0,077
	К-20	3 475	2	0,027
				0,105 м³
				0,120 м³

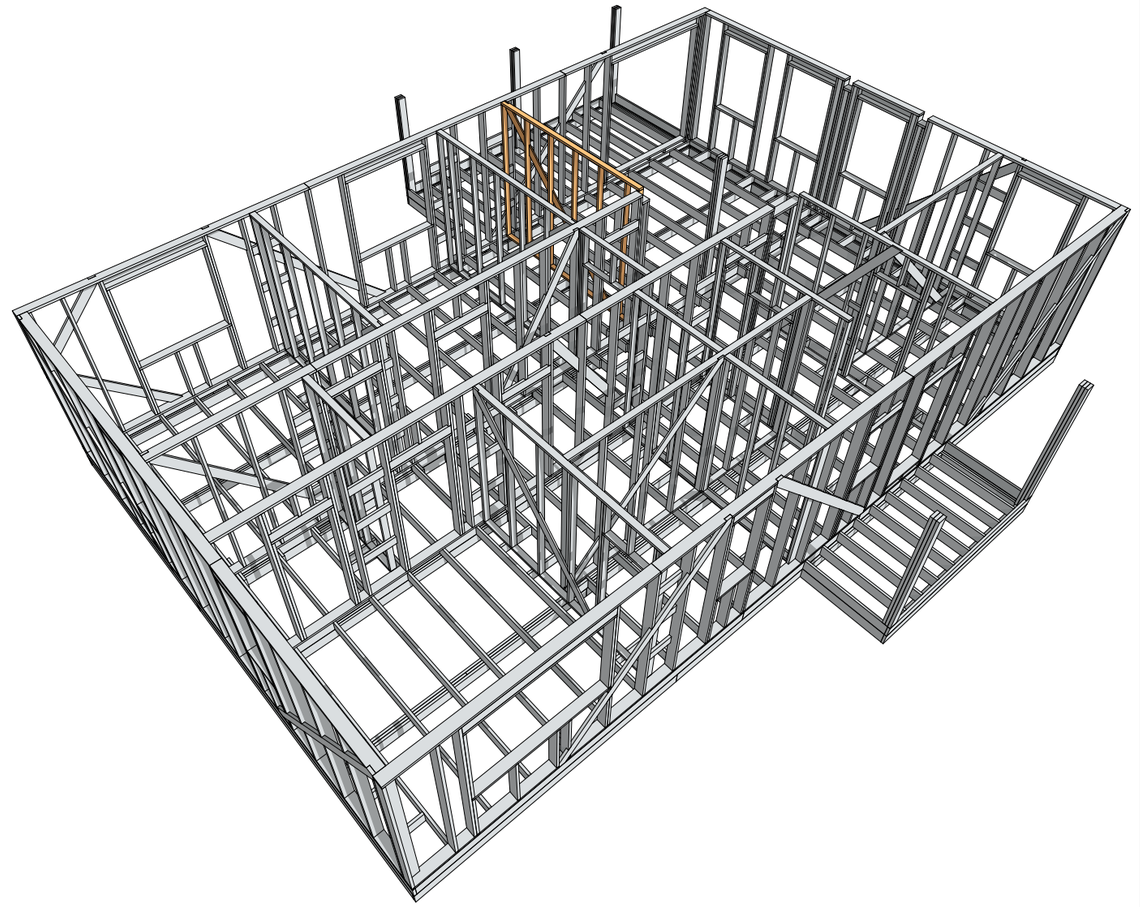


						Лист
1				03/2026	Стена Ст-16	31
Изм.	Лист	№ докум.	Подпись	Дата		

Стена Ст-17

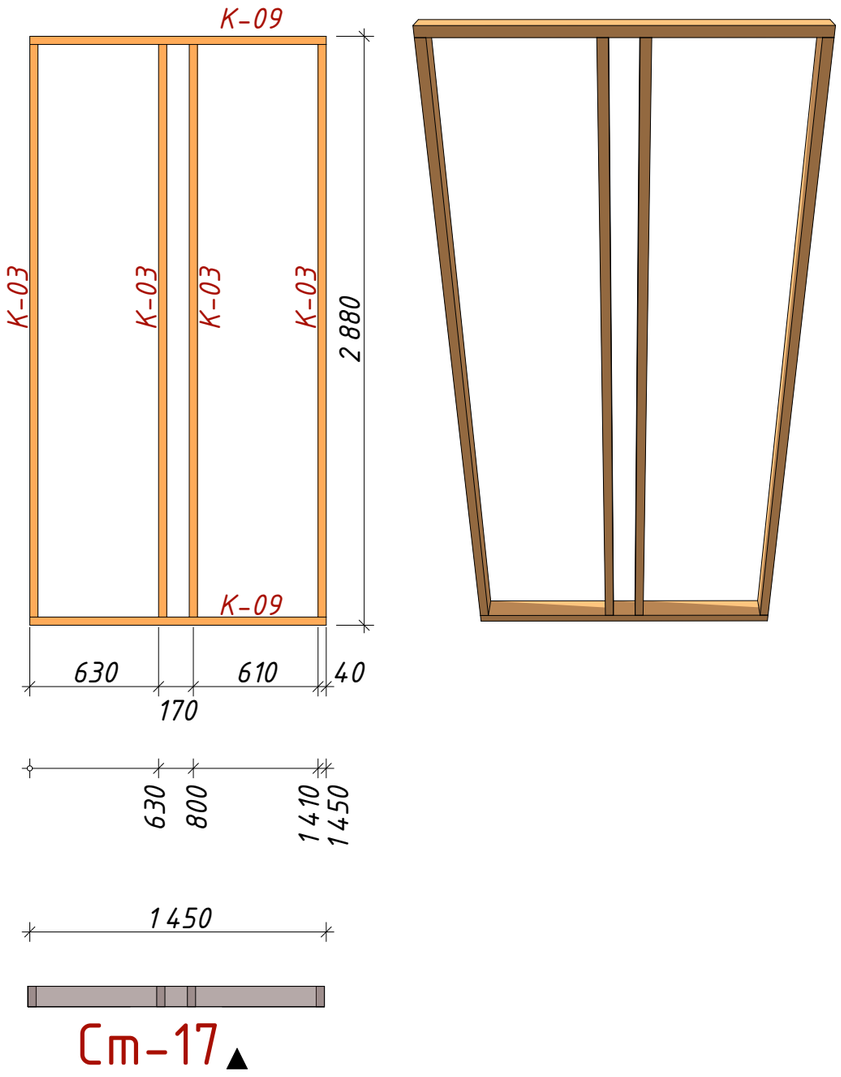



КД Спецификация деревянных элементов стены Ст-17				
Сечение	Марка	Длина	Кол-во	Объем
40х100				
	К-09	1 450	2	0,012
	К-03	2 800	4	0,045
				0,056 м³

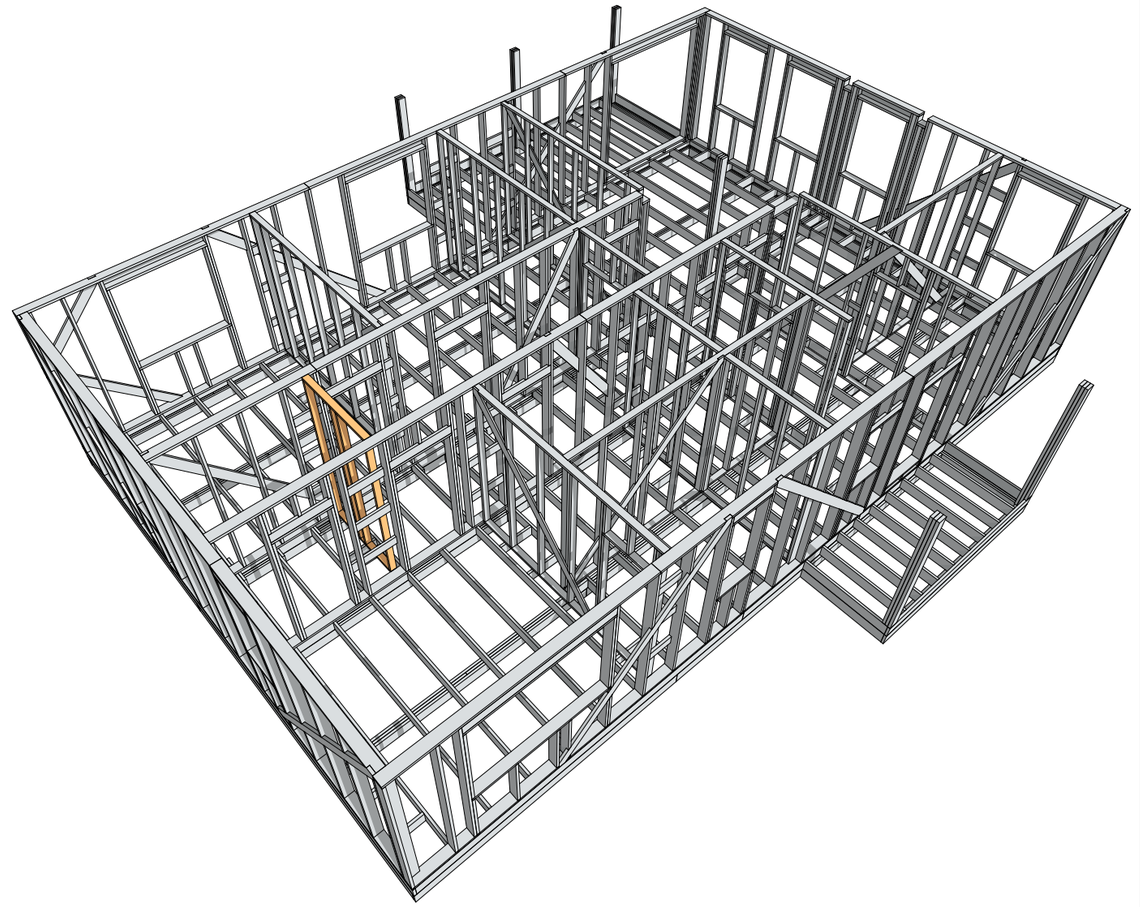

					Стена Ст-17	Лист
1				03/2026		32
Изм.	Лист	№ докум.	Подпись	Дата		

Стена Ст-18

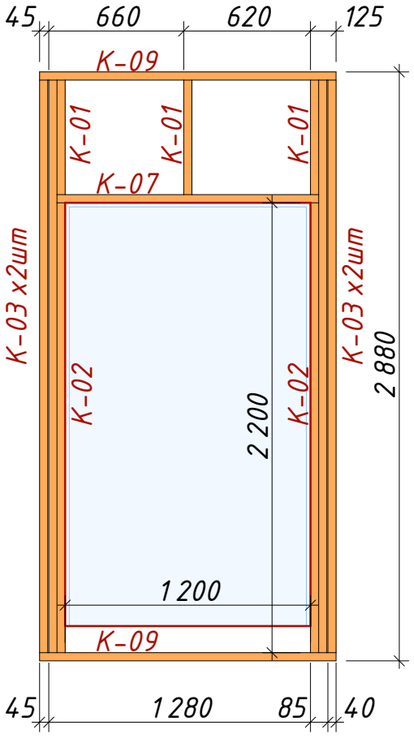

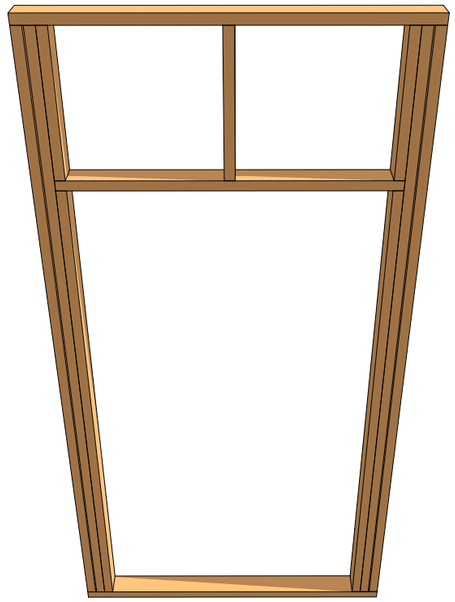







Ст-18

КД Спецификация деревянных элементов стены Ст-18				
Сечение	Марка	Длина	Кол-во	Объем
40х100				
	К-01	560	3	0,007
	К-07	1 280	1	0,005
	К-09	1 450	2	0,012
	К-02	2 200	2	0,018
	К-03	2 800	4	0,045
				0,086 м³

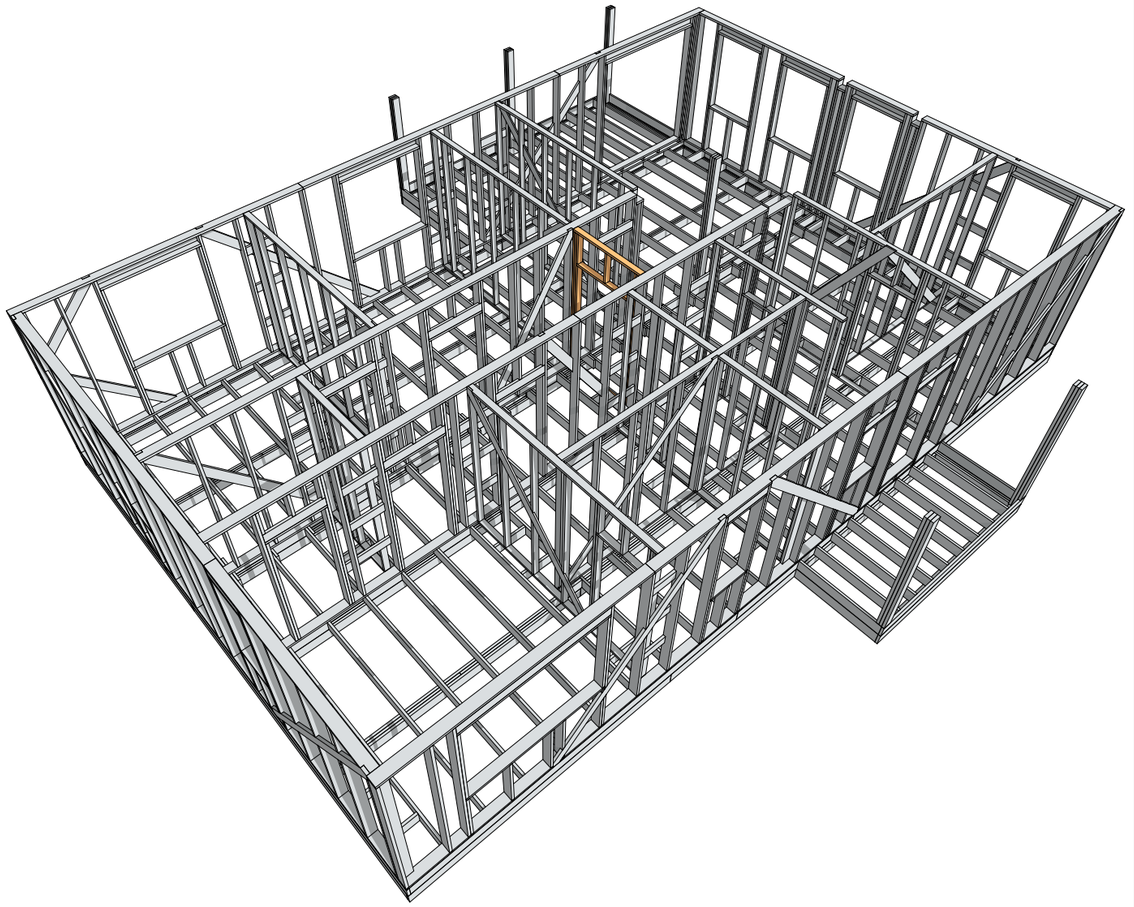

						Лист
1				03/2026	Стена Ст-18	33
Изм.	Лист	№ докум.	Подпись	Дата		

Обвязка стен 1-го этажа

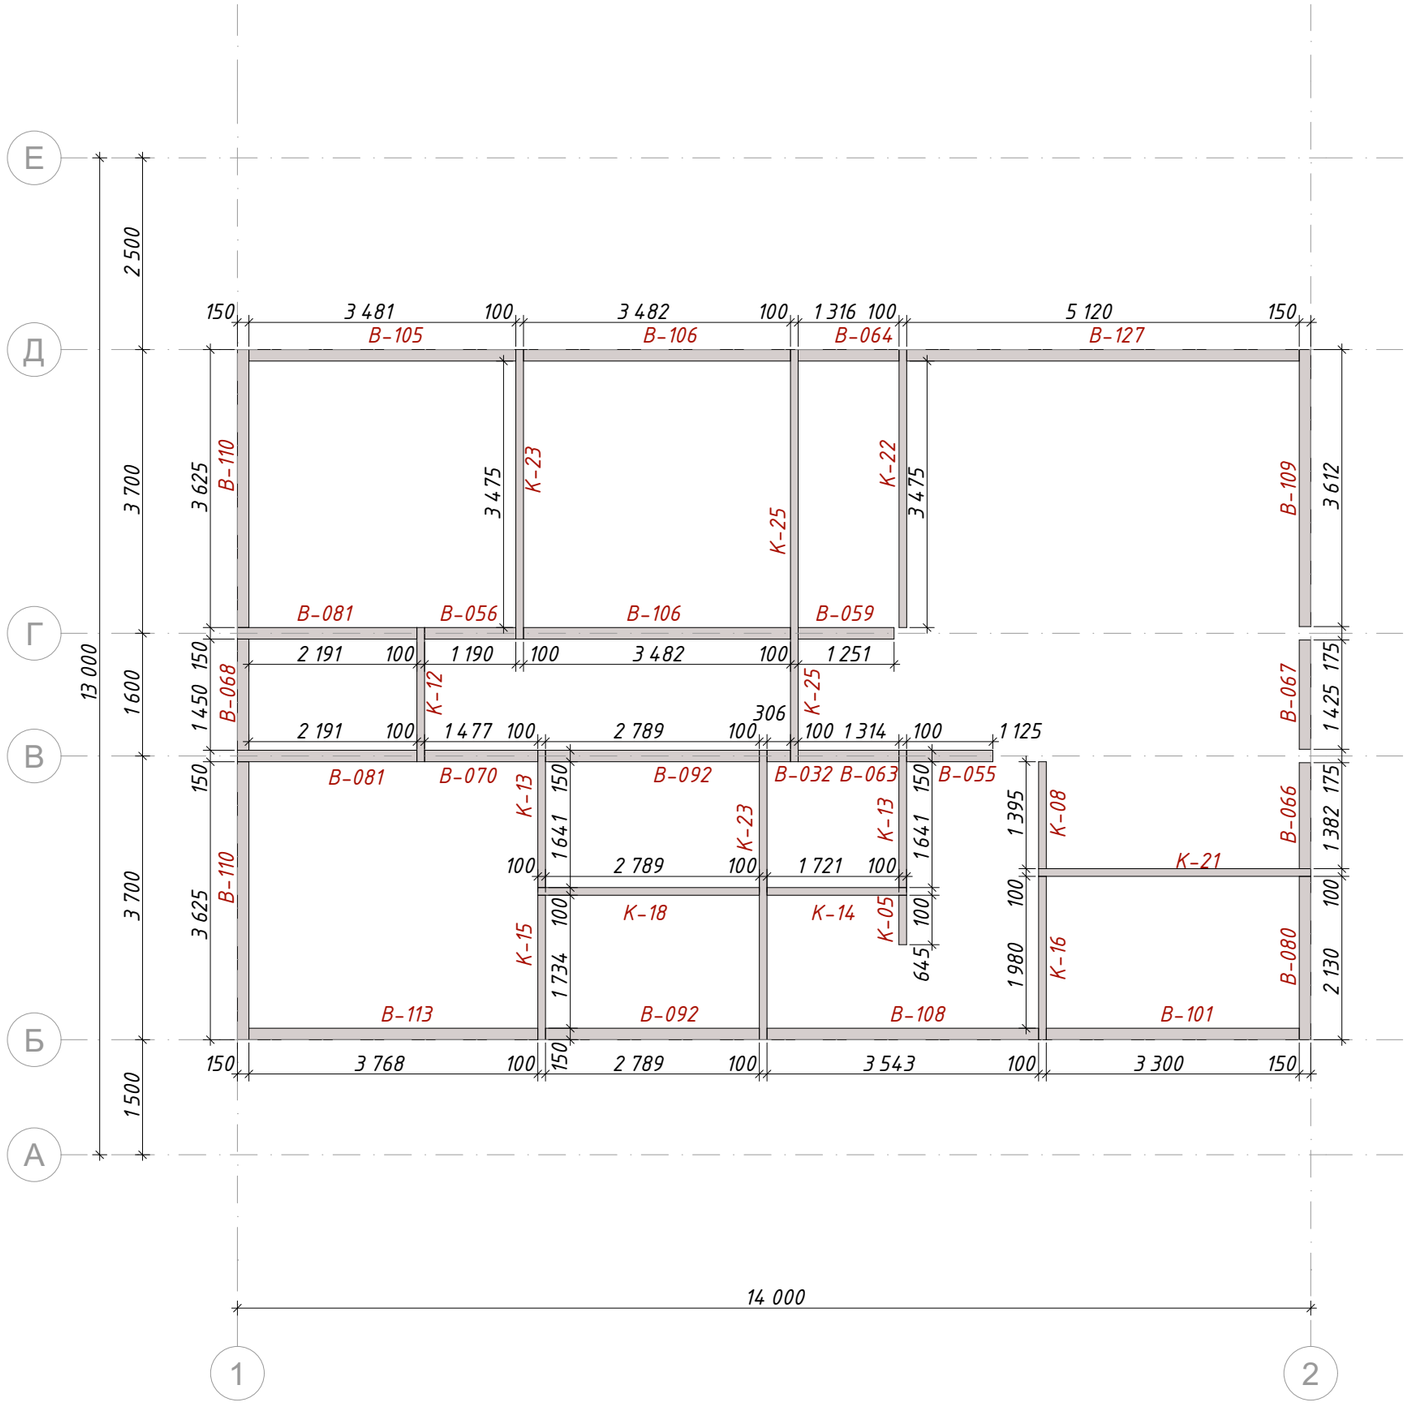


КД Спецификация деревянных элементов обвязки стен 1-го этажа


Сечение	Марка	Длина	Кол-во	Объем
40x100				
	К-05	645	1	0,003
	К-08	1 395	1	0,006
	К-12	1 750	1	0,007
	К-13	1 791	2	0,014
	К-14	1 821	1	0,007
	К-15	1 884	1	0,008
	К-16	2 130	1	0,009
	К-18	2 889	1	0,012
	К-21	3 550	1	0,014
	К-22	3 625	1	0,015
	К-23	3 775	2	0,030
	К-25	5 375	1	0,021
				0,145 м³
40x150				
	В-032	306	1	0,002
	В-055	1 125	1	0,007
	В-056	1 190	1	0,007
	В-059	1 251	1	0,008
	В-063	1 314	1	0,008
	В-064	1 316	1	0,008
	В-066	1 382	1	0,008
	В-067	1 425	1	0,009
	В-068	1 450	1	0,009
	В-070	1 477	1	0,009
	В-080	2 130	1	0,013
	В-081	2 341	2	0,028
	В-092	2 789	2	0,033
	В-101	3 300	1	0,020
	В-105	3 481	1	0,021
	В-106	3 482	2	0,042
	В-108	3 543	1	0,021
	В-109	3 612	1	0,022
	В-110	3 625	2	0,043
	В-113	3 768	1	0,023
	В-127	5 120	1	0,031
				0,370 м³
				0,515 м³

Изм.	Лист	№ докум.	Подпись	Дата	Обвязка стен 1-го этажа	Лист
1				03/2026		34


Обвязка стен: 3D-вид

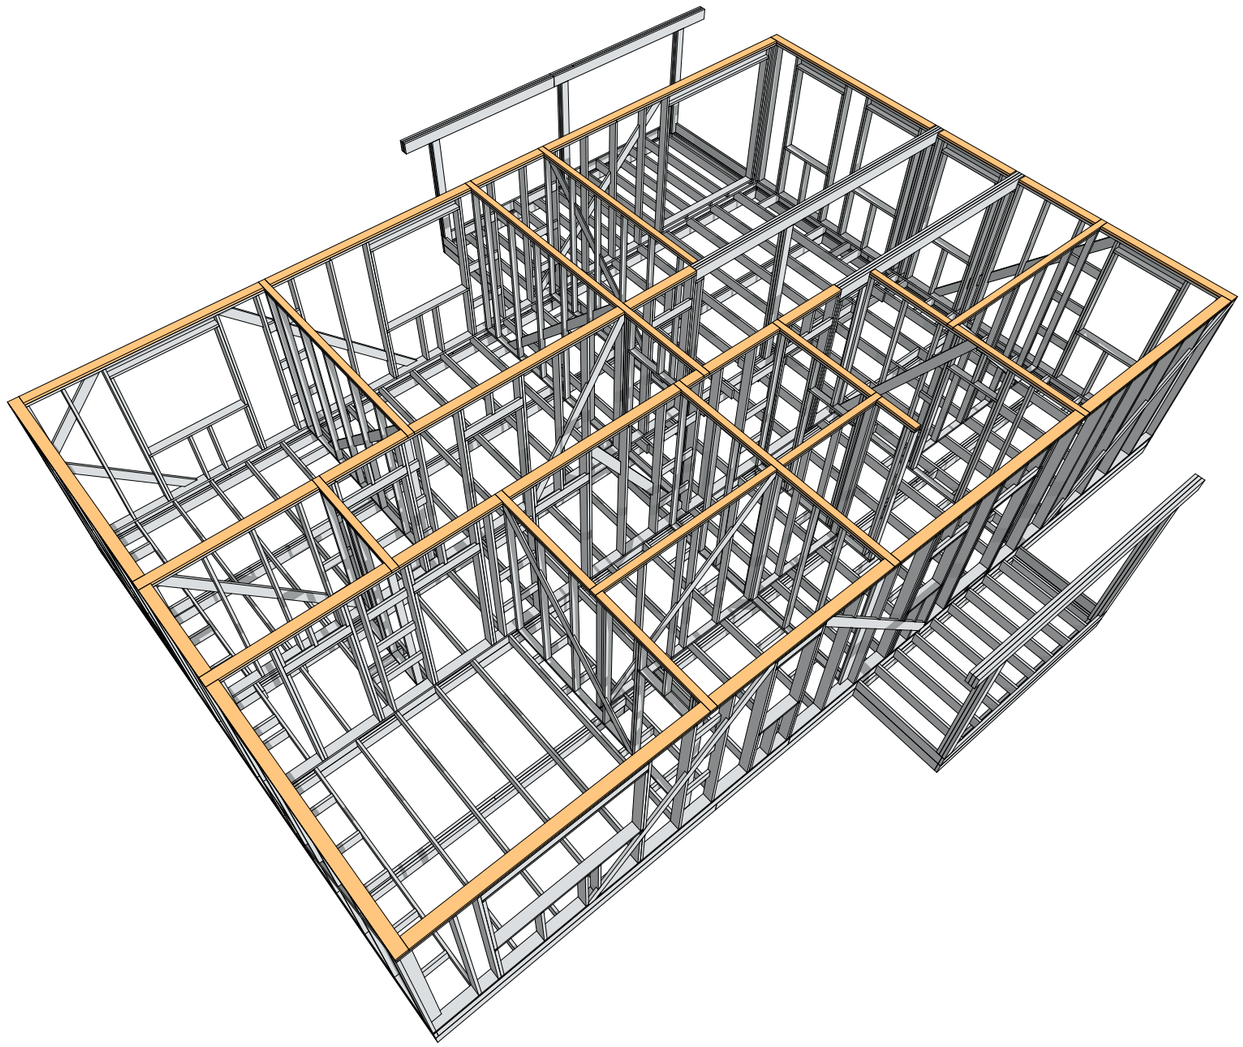


Верхняя обвязка стен (Т-образное соединение)

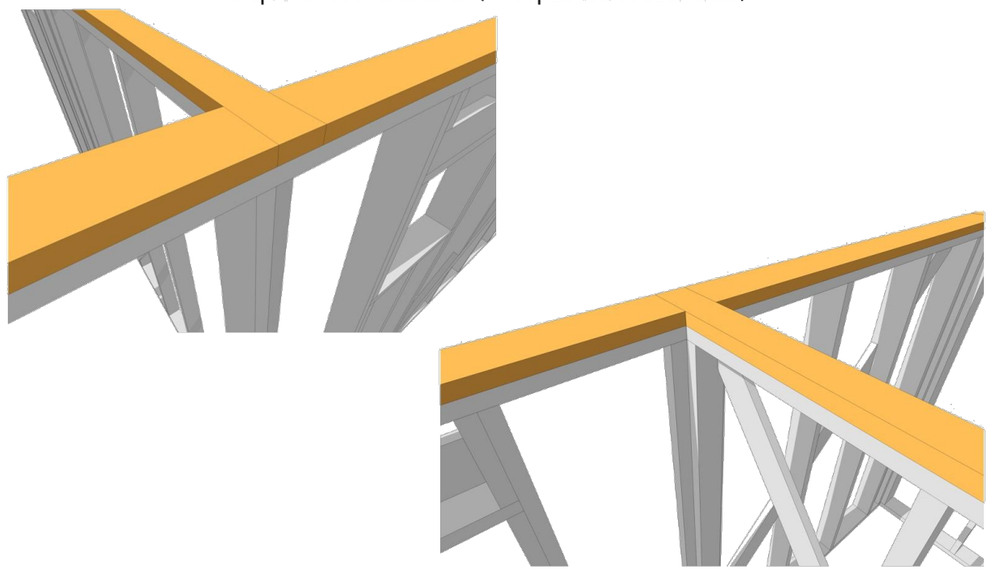

Верхняя обвязка стен (угловое соединение)

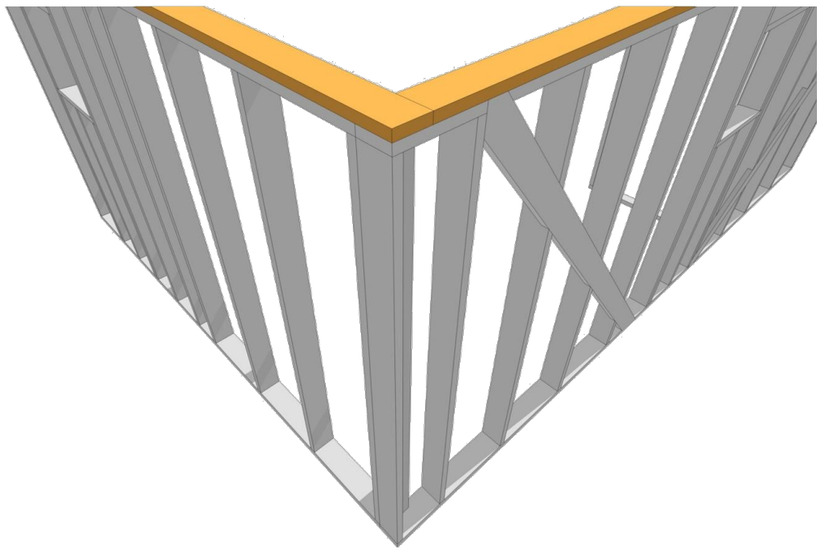


С2.15 Крепление второй верхней обвязки. Т-образное примыкание

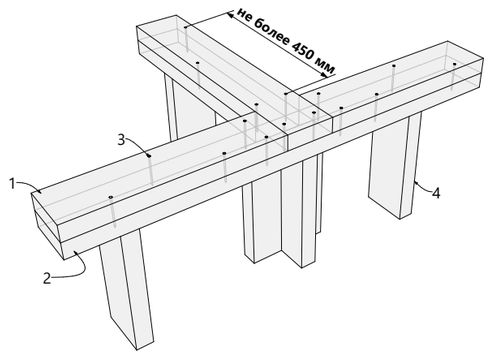

1-вторая верхняя обвязка; 2-верхняя обвязка каркасной стены; 3-гвоздь;
4-стойка каркасной стены.


С2.14 Крепление второй верхней обвязки. Г-образное примыкание

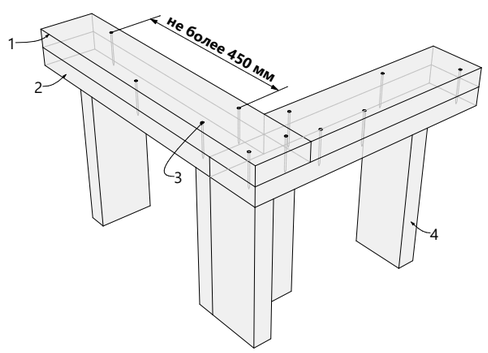

1-вторая верхняя обвязка; 2-верхняя обвязка каркасной стены; 3-гвоздь;
4-стойка каркасной стены.


					Обвязка стен: 3D-вид	Лист
1				03/2026		35
Изм.	Лист	№ докум.	Подпись	Дата		

Балки 1-го этажа

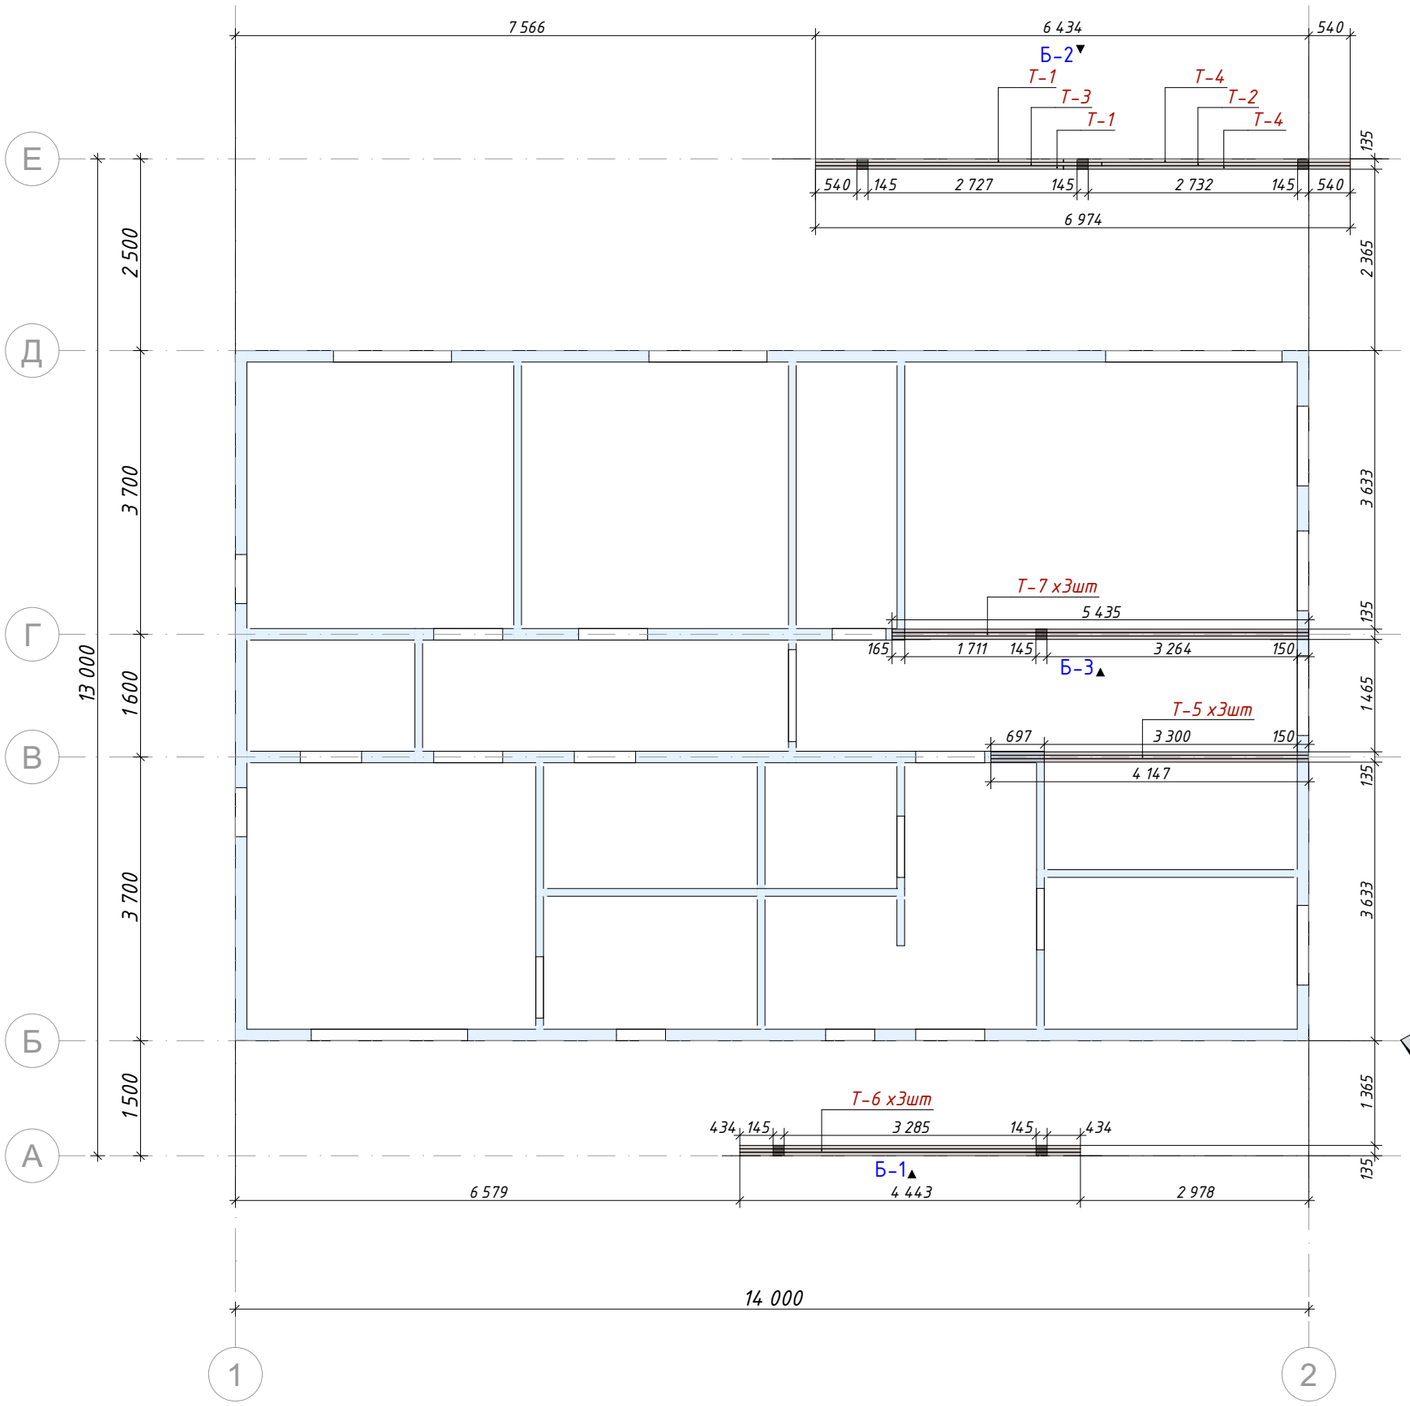

КД Спецификация деревянных элементов балок 1-го этажа


Сечение	Марка	Длина	Кол-во	Объем
45х195				
	Т-1	3 234	2	0,057
	Т-2	3 240	1	0,028
	Т-3	3 734	1	0,033
	Т-4	3 740	2	0,066
	Т-5	4 147	3	0,109
	Т-6	4 443	3	0,117
	Т-7	5 435	3	0,143
				0,553 м³

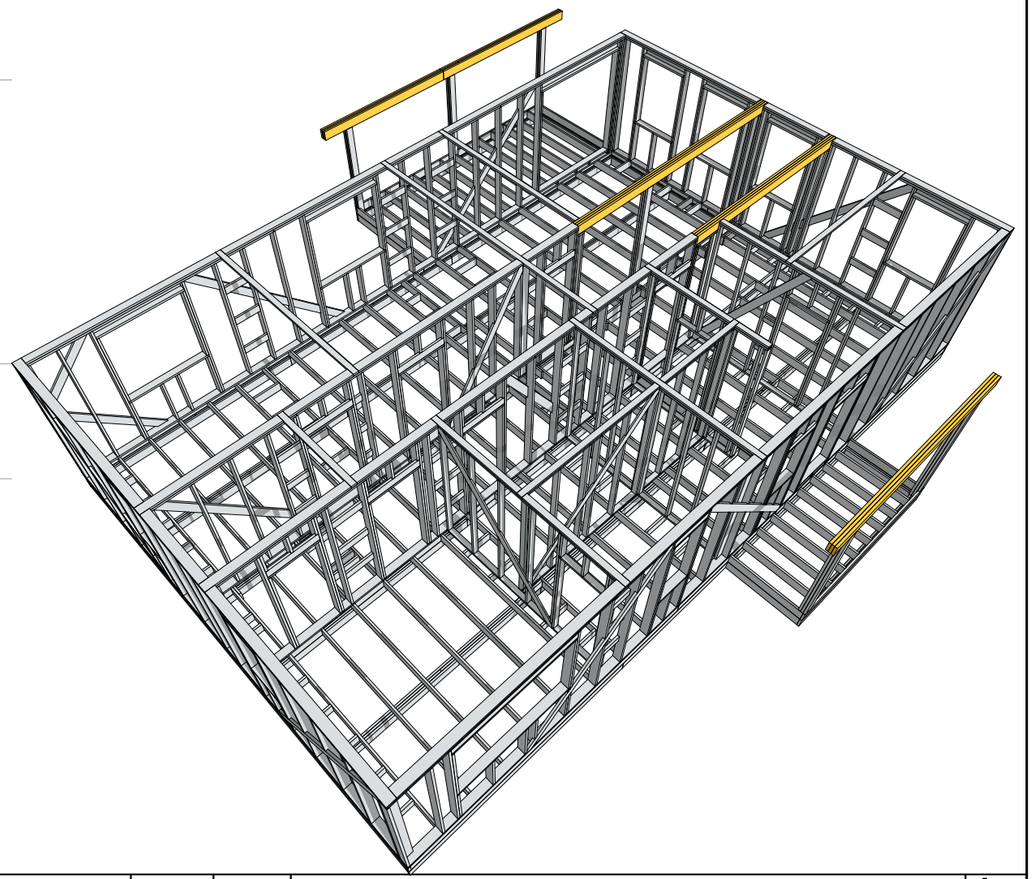


					Балки 1-го этажа	Лист
1				03/2026		36
Изм.	Лист	№ докум.	Подпись	Дата		

Балки 1-го этажа: сечения


Б-1 Сечение балок 1

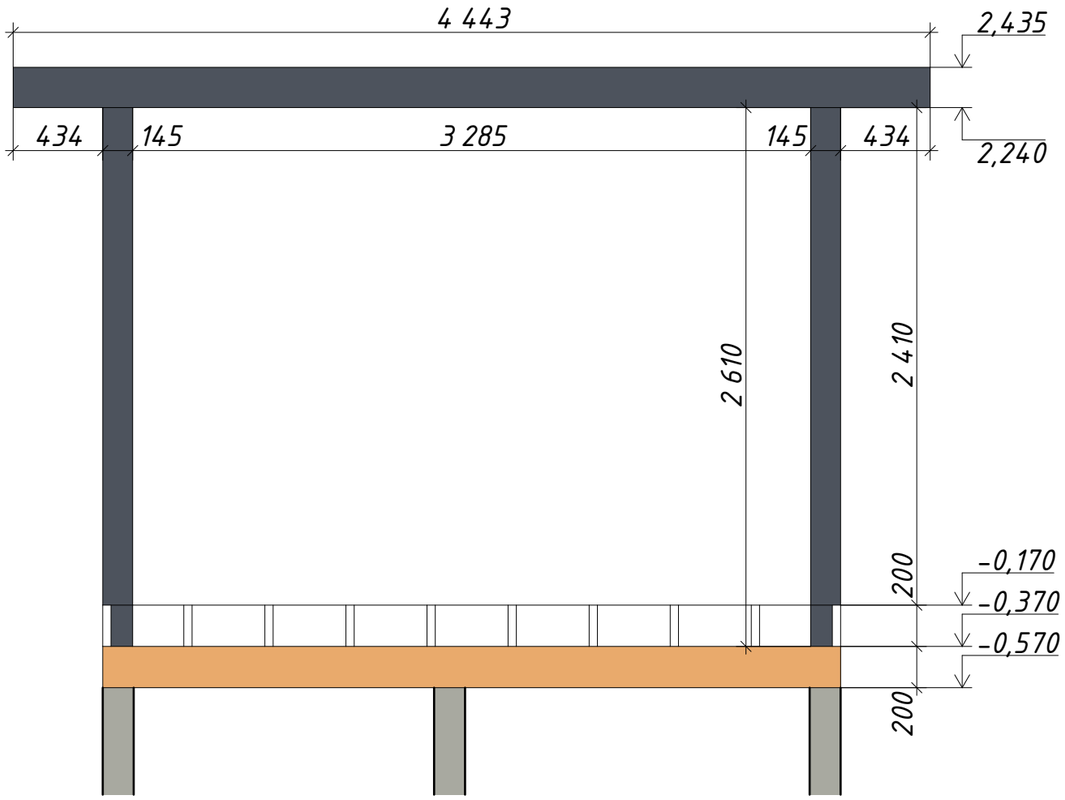

Б-3 Сечение балок 3

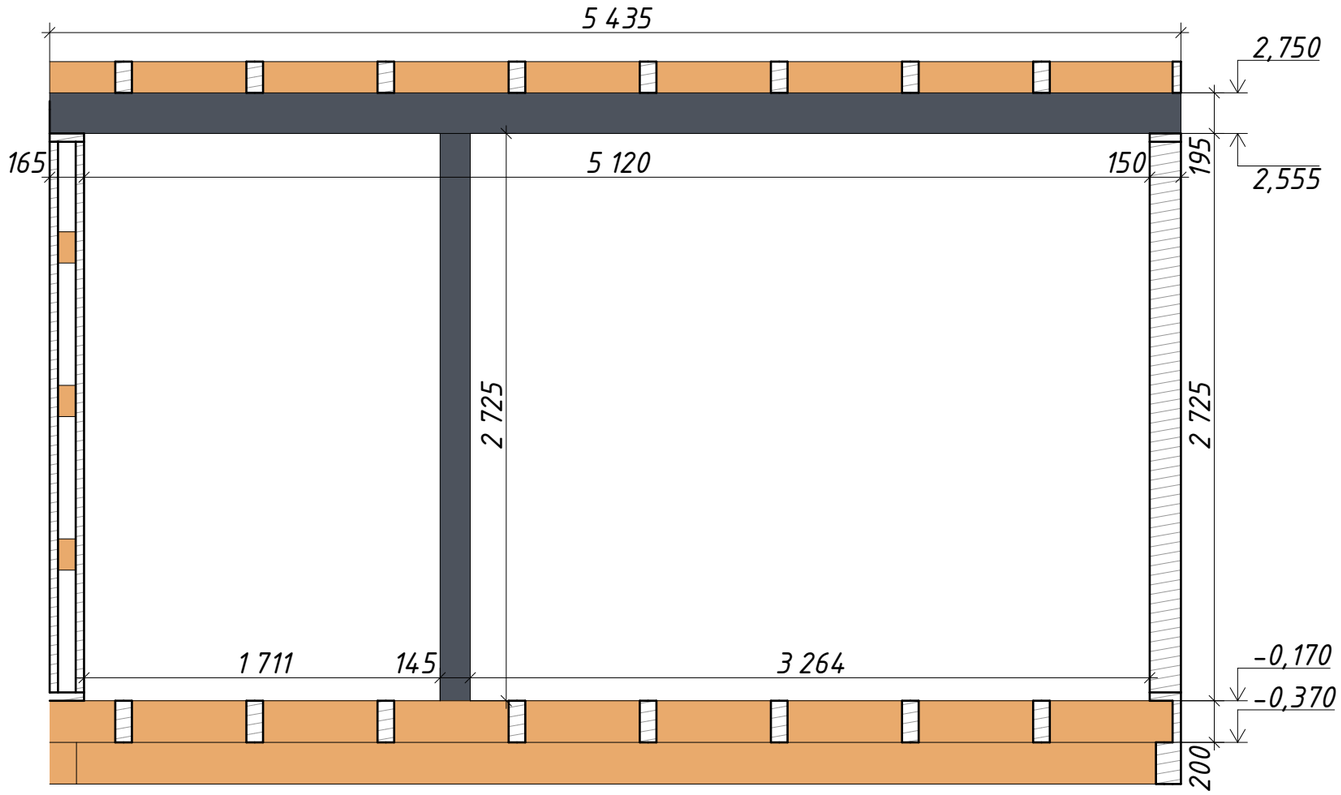



Б-2 Сечение балок 2

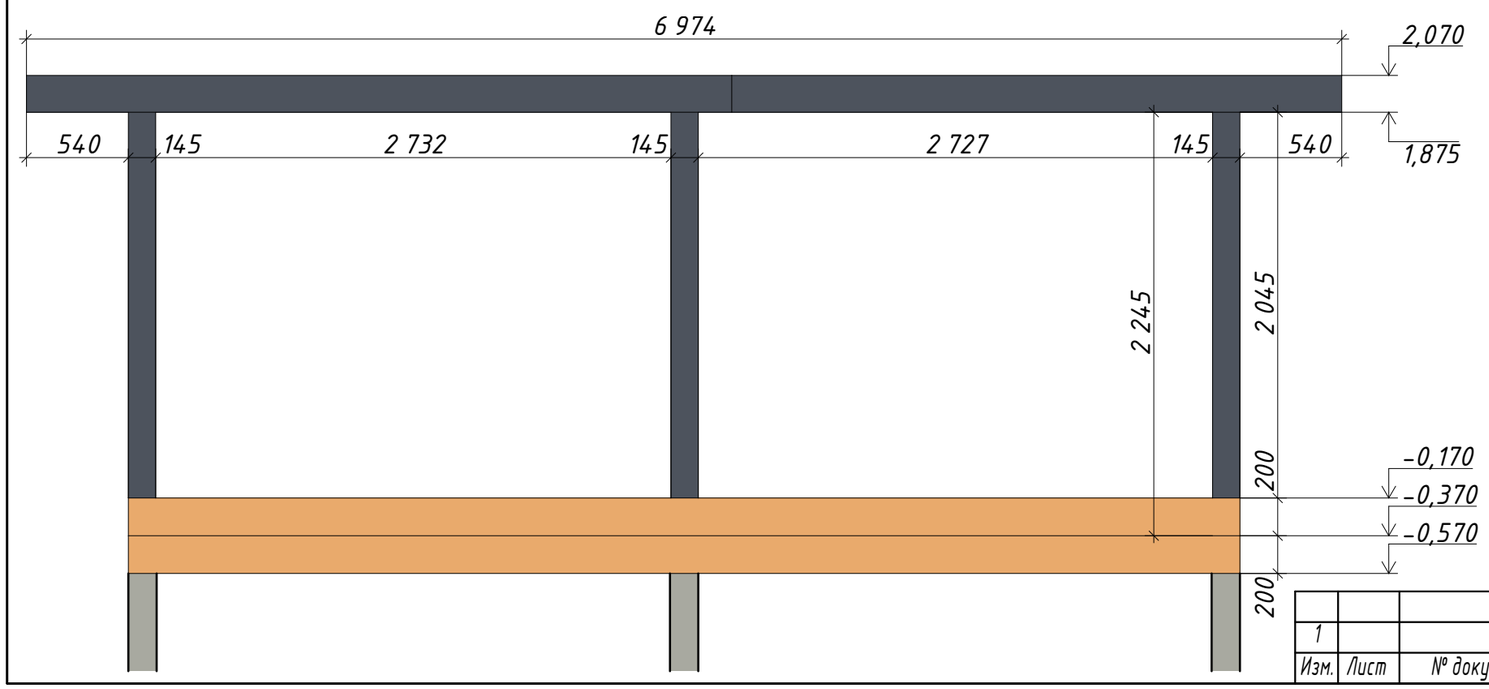

					Лист
1				03/2026	37
Изм.	Лист	№ докум.	Подпись	Дата	Балки 1-го этажа: сечения

План чердачного перекрытия

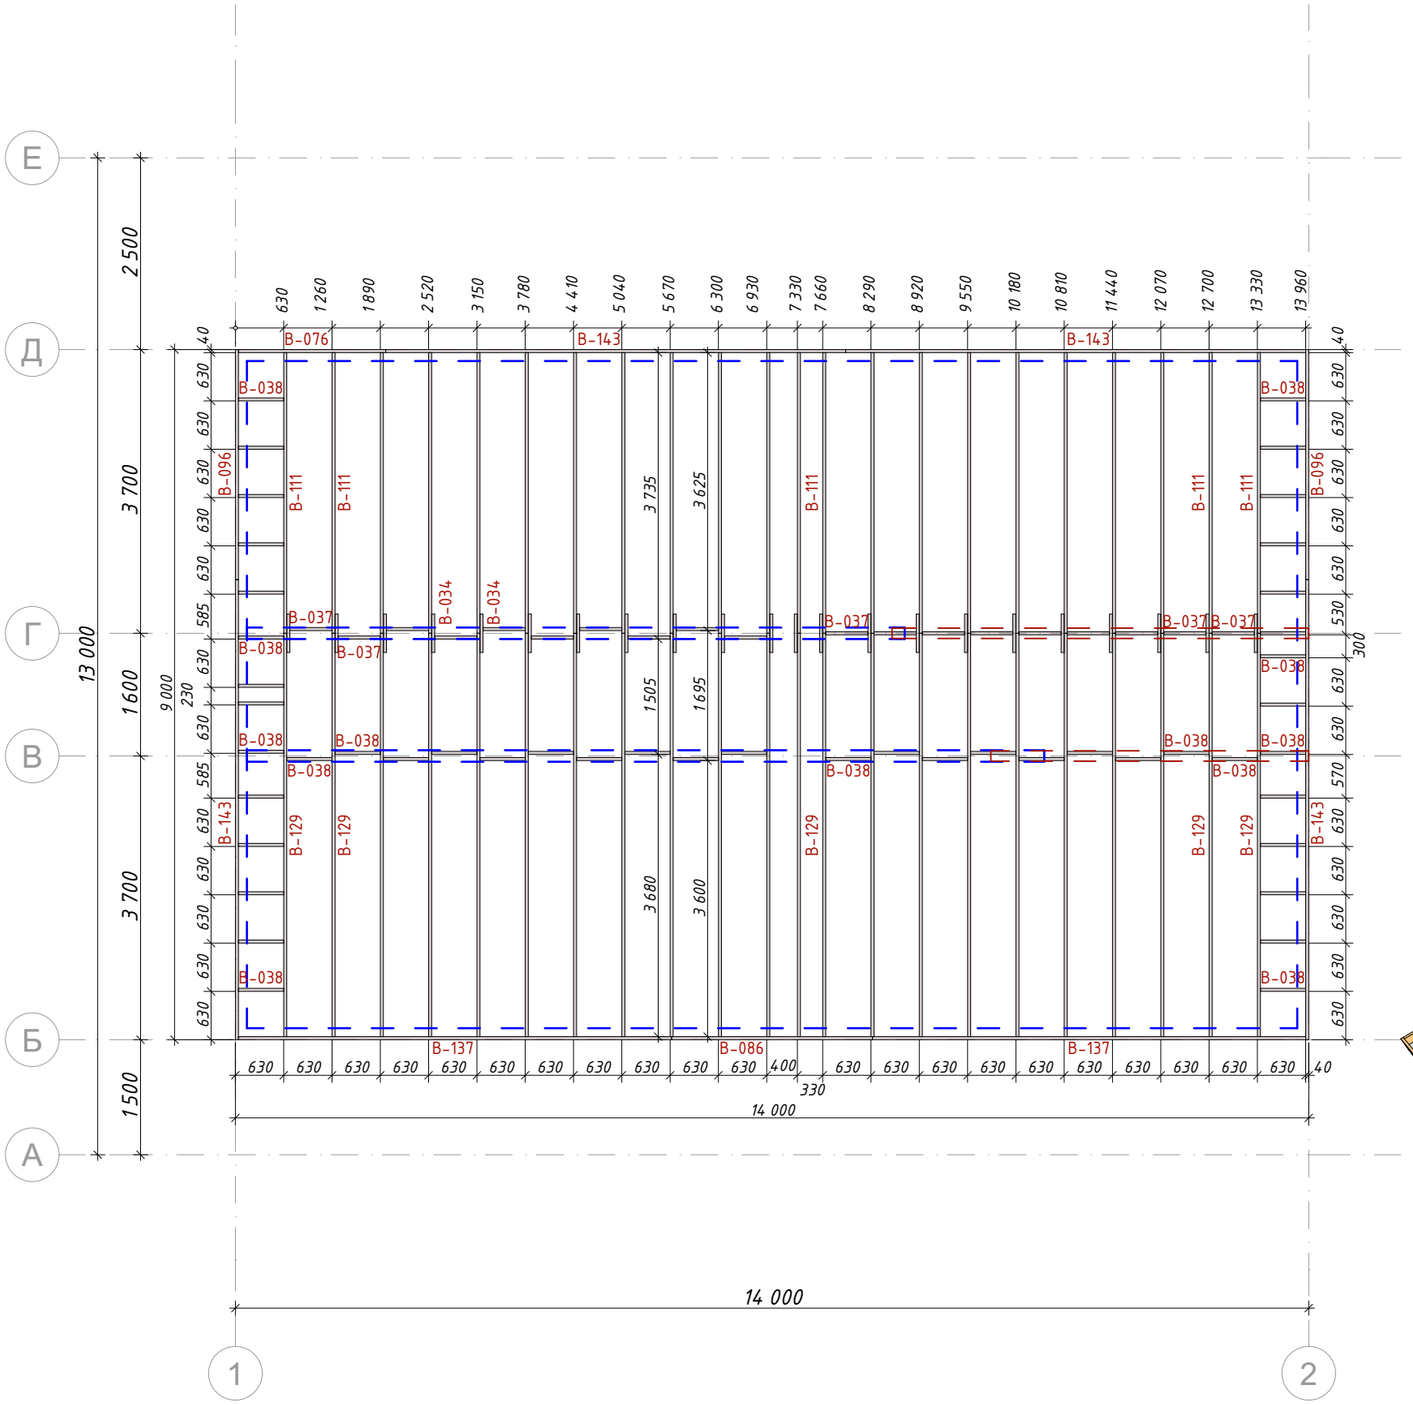

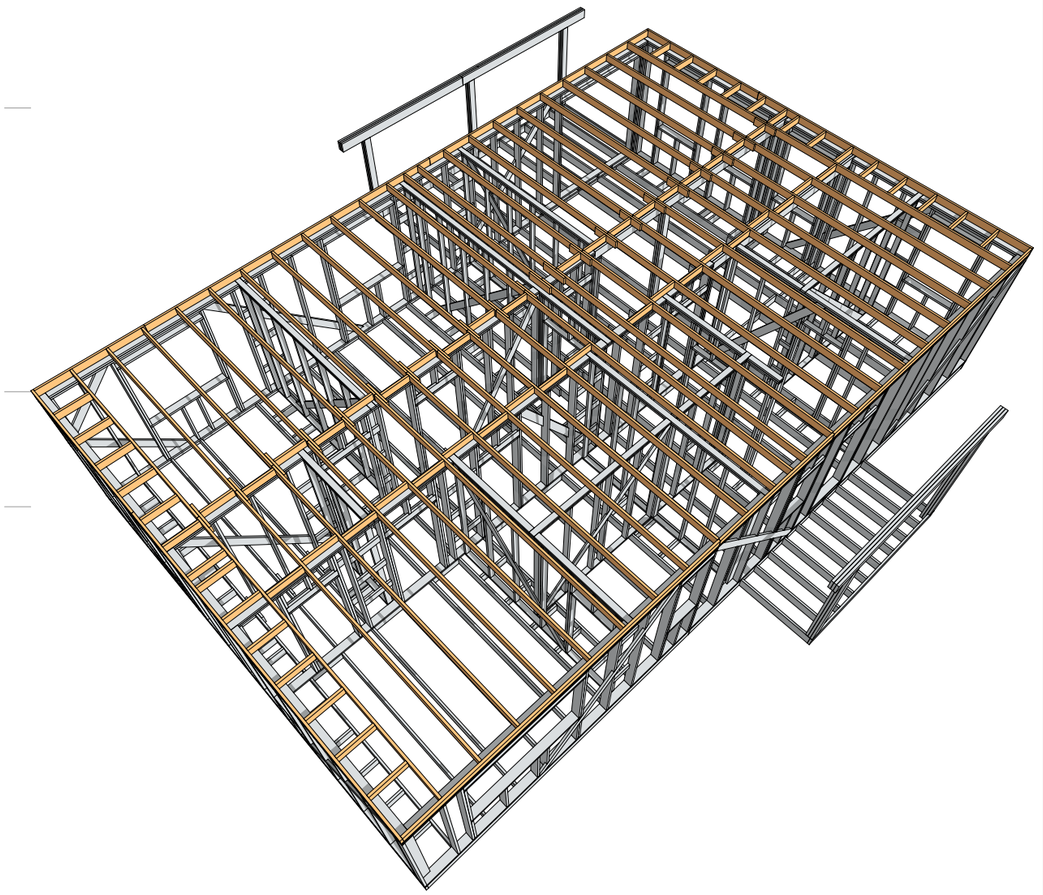

КД Спецификация деревянных элементов чердасного перекрытия


Сечение	Марка	Длина	Кол-во	Объем
40х150				
	B-034	500	22	0,066
	B-037	550	19	0,063
	B-038	590	47	0,166
	B-076	1 920	1	0,012
	B-086	2 620	1	0,016
	B-096	3 000	2	0,036
	B-111	3 660	22	0,483
	B-129	5 260	22	0,694
	B-137	5 650	2	0,068
	B-143	6 000	4	0,144
				1,748 м³

Примечание:

1. Синими линиями обозначены контуры несущих стен.
2. Красными линиями обозначены балки первого этажа.


Изм.	Лист	№ докум.	Подпись	Дата	План чердачного перекрытия	Лист
1				03/2026		38

План подстропильных конструкций

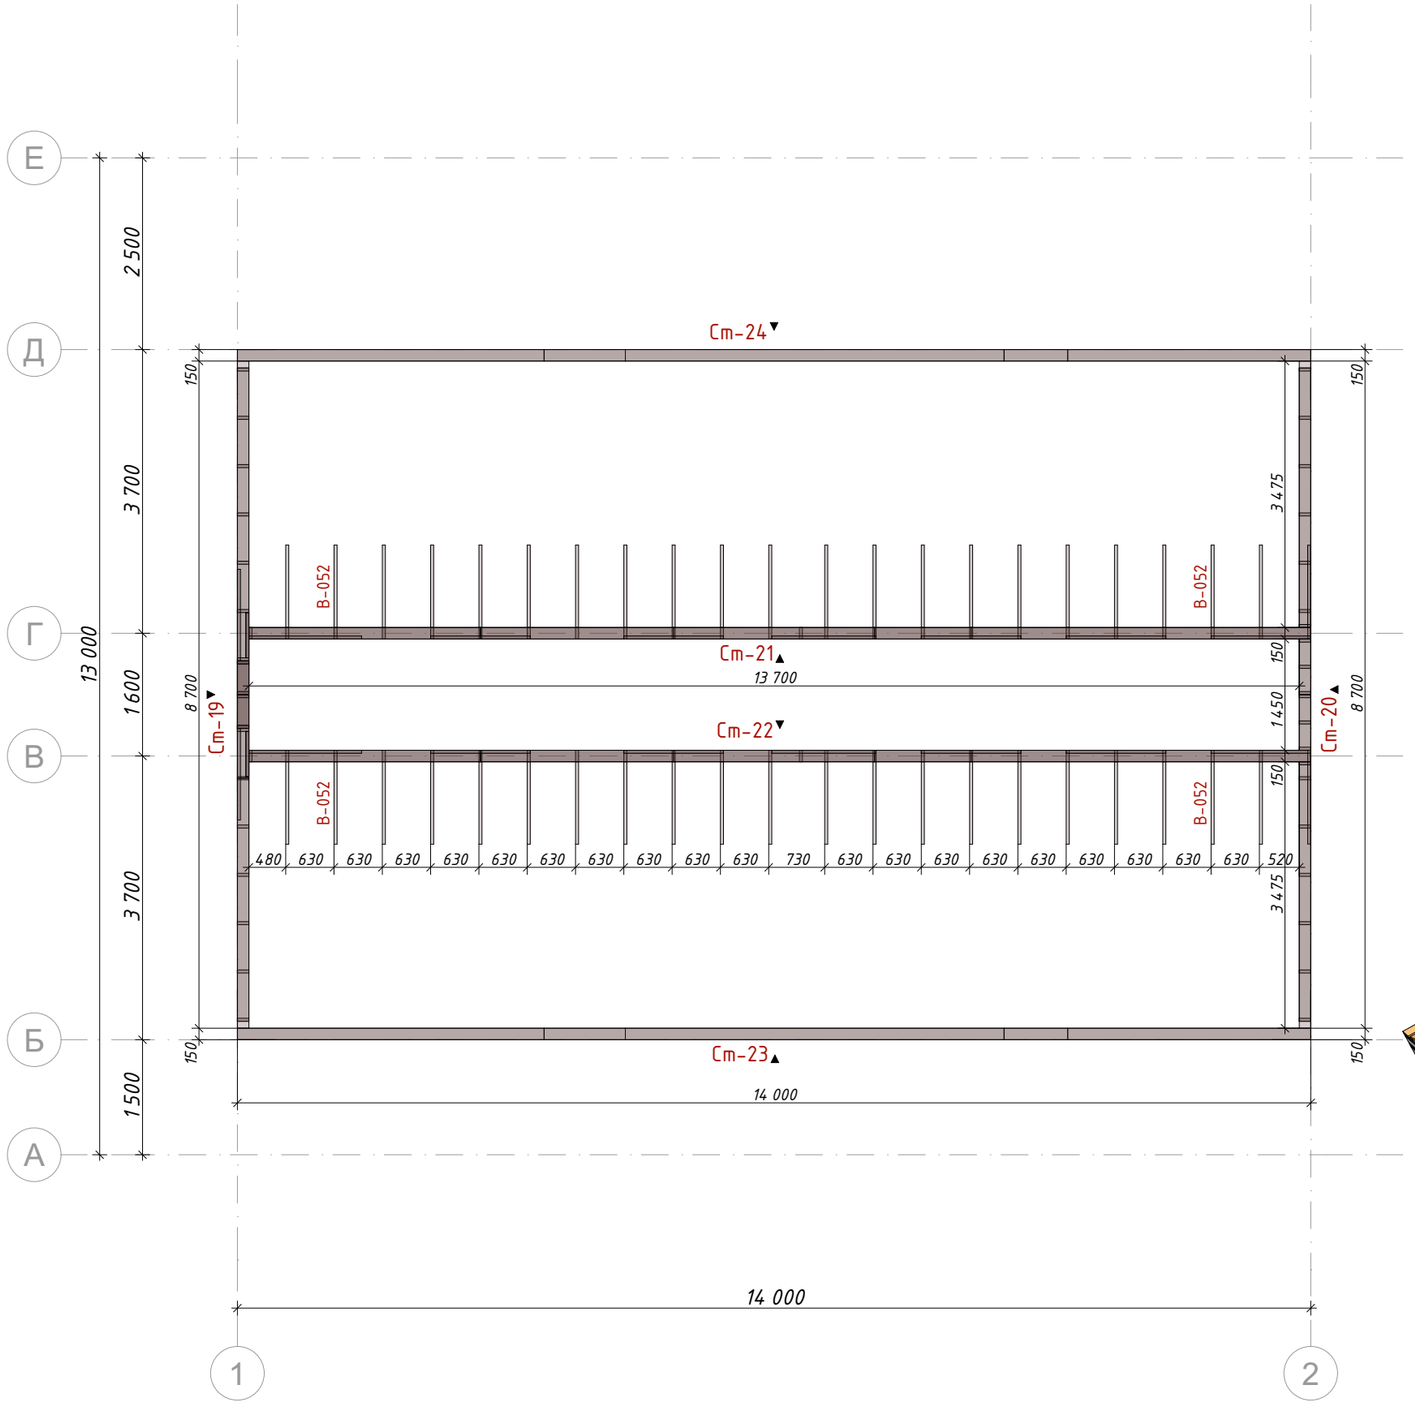


КД Спецификация деревянных элементов подстропильных стоек


Сечение	Марка	Длина	Кол-во	Объем
40х150				
	В-052	1 671	42	0,346
				0,346 м³

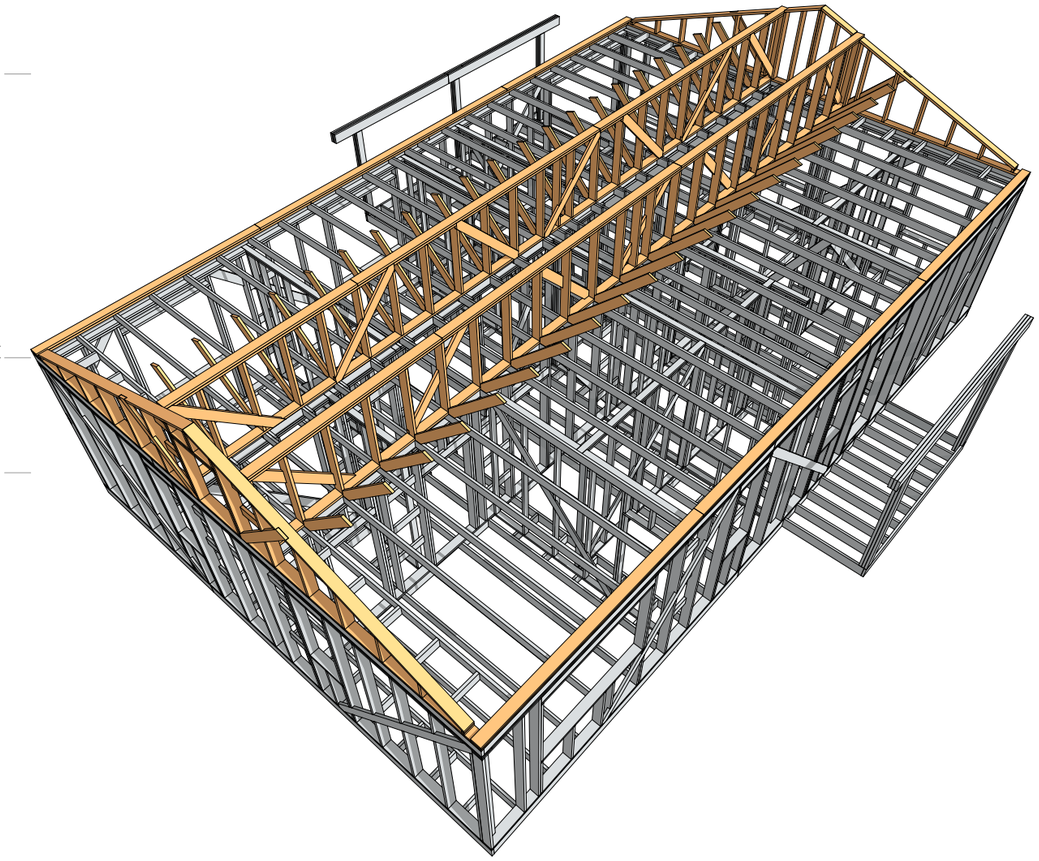


					План подстропильных конструкций	Лист
1				03/2026		39
Изм.	Лист	№ докум.	Подпись	Дата		


Стена Ст-19

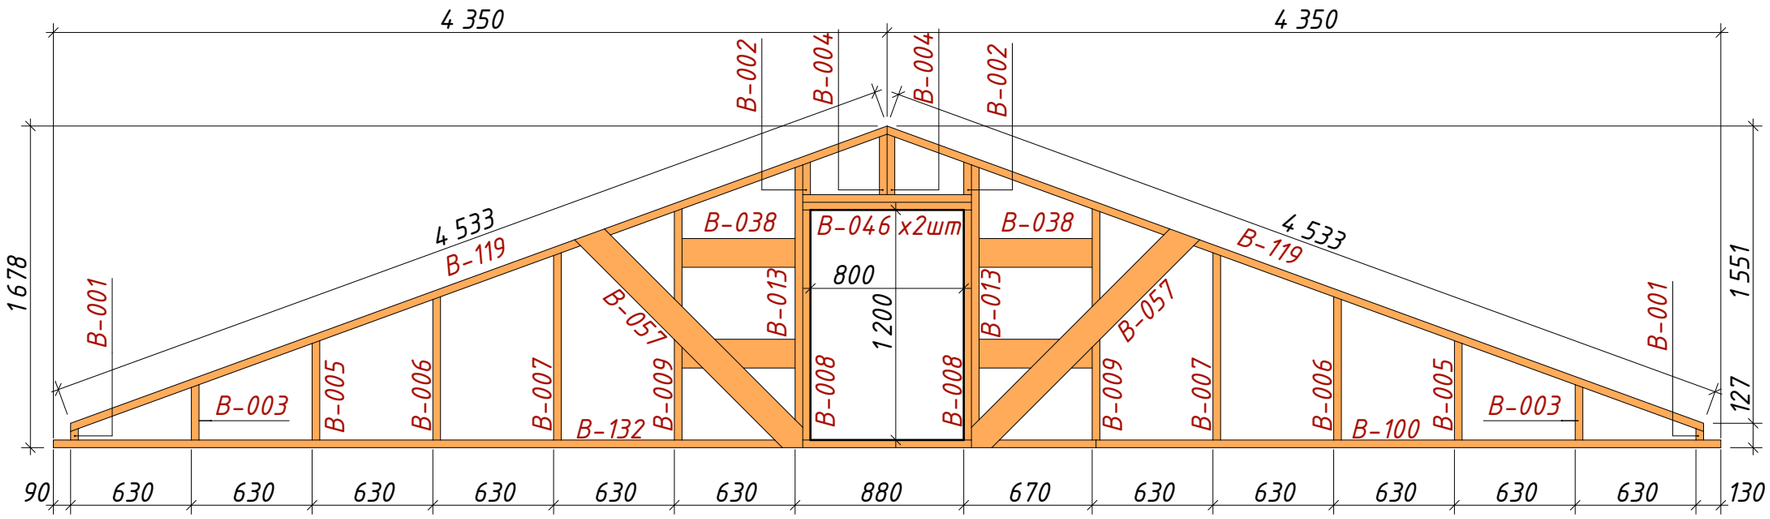

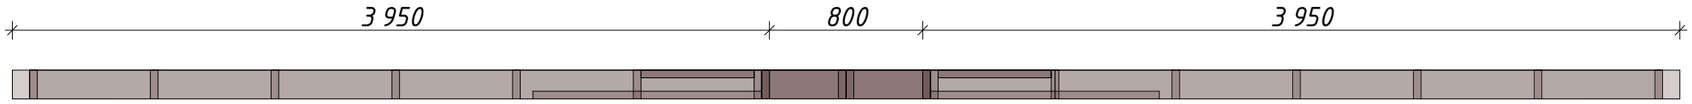

▲(Ст-19)

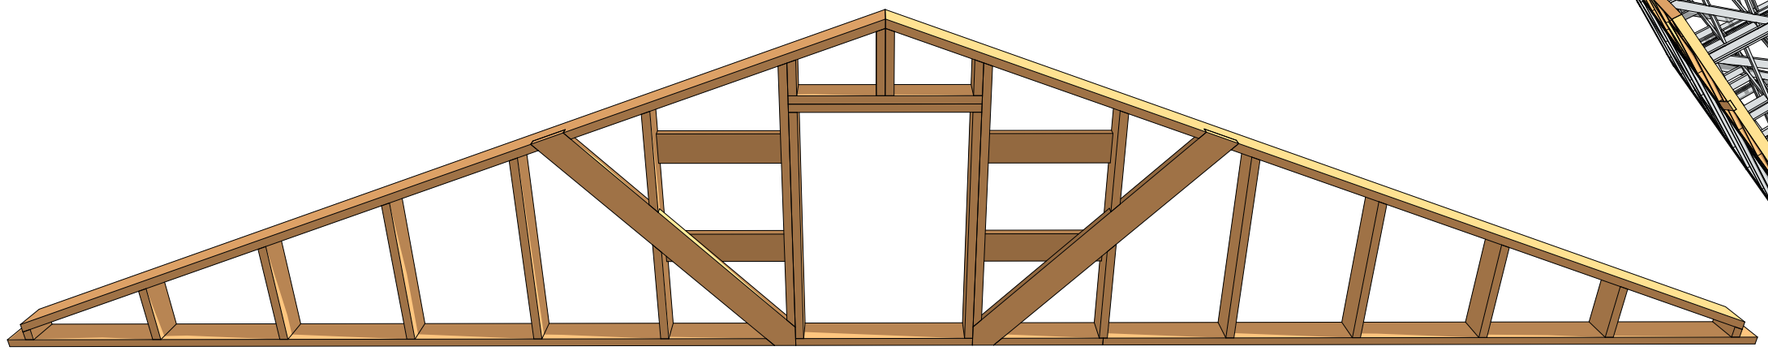


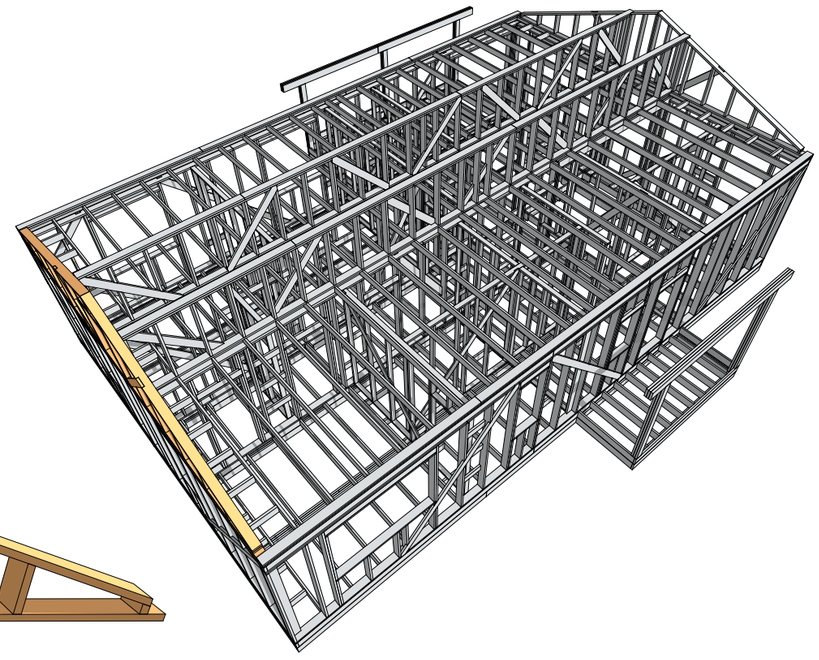

КД Спецификация деревянных элементов стены Ст-19				
Сечение	Марка	Длина	Кол-во	Объем
40х150				
	В-001	59	2	0,001
	В-002	170	2	0,002
	В-003	289	2	0,003
	В-004	315	2	0,004
	В-005	518	2	0,006
	В-038	590	4	0,014
	В-006	747	2	0,009
	В-046	880	2	0,011
	В-007	977	2	0,012
	В-008	1 200	2	0,014
	В-009	1 206	2	0,014
	В-013	1 435	2	0,017
	В-057	1 839	2	0,018
	В-100	3 260	1	0,020
	В-119	4 548	2	0,054
	В-132	5 440	1	0,032
				0,230 м³

					Стена Ст-19	Лист
1				03/2026		40
Изм.	Лист	№ докум.	Подпись	Дата		


Стена Ст-20

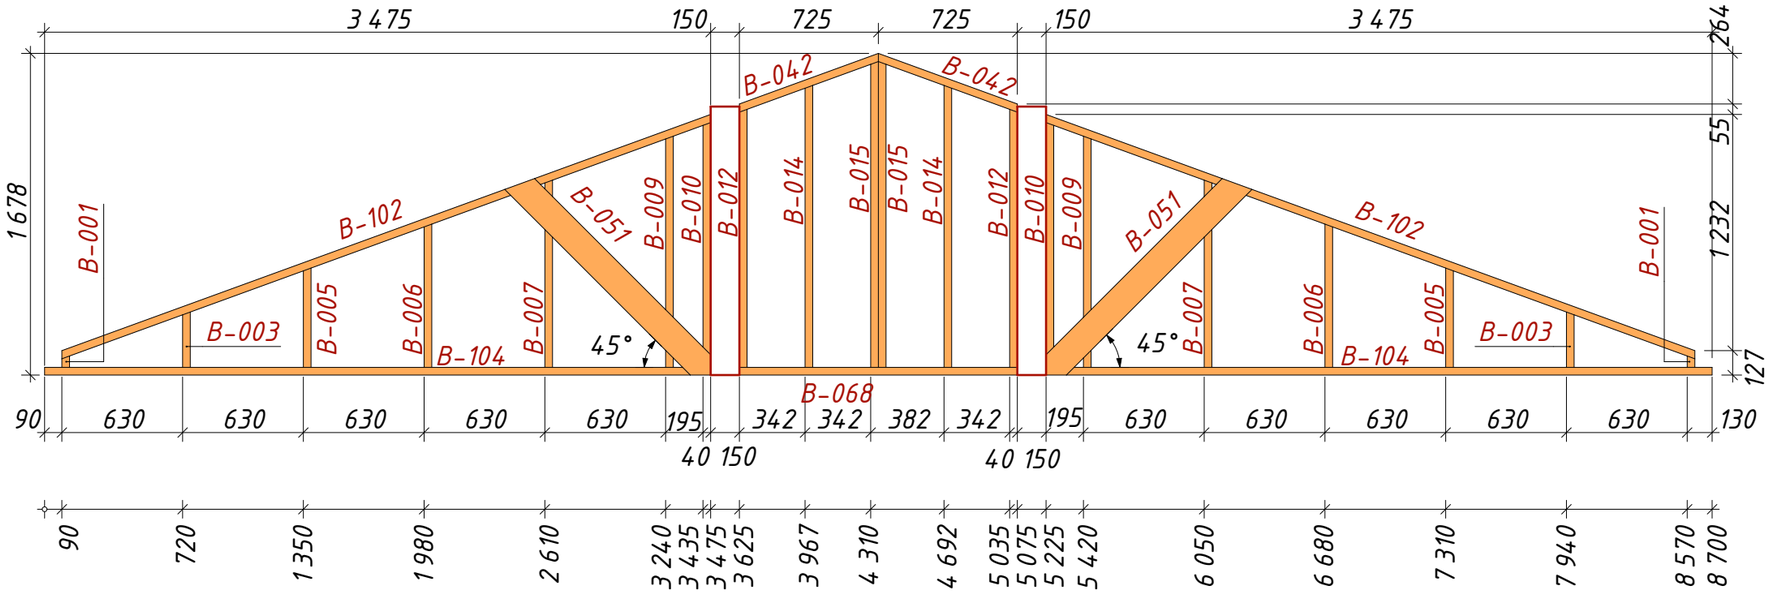


Ст-20▲

КД Спецификация деревянных элементов стены Ст-20


Сечение	Марка	Длина	Кол-во	Объем
40x150				
	B-001	59	2	0,001
	B-003	289	2	0,003
	B-005	518	2	0,006
	B-006	747	2	0,009
	B-042	786	2	0,009
	B-007	977	2	0,011
	B-009	1 206	2	0,014
	B-010	1 277	2	0,015
	B-012	1 346	2	0,016
	B-068	1 450	1	0,009
	B-014	1 471	2	0,018
	B-015	1 595	2	0,019
	B-051	1 668	2	0,016
	B-104	3 475	2	0,041
	B-102	3 617	2	0,043
				0,230 м³

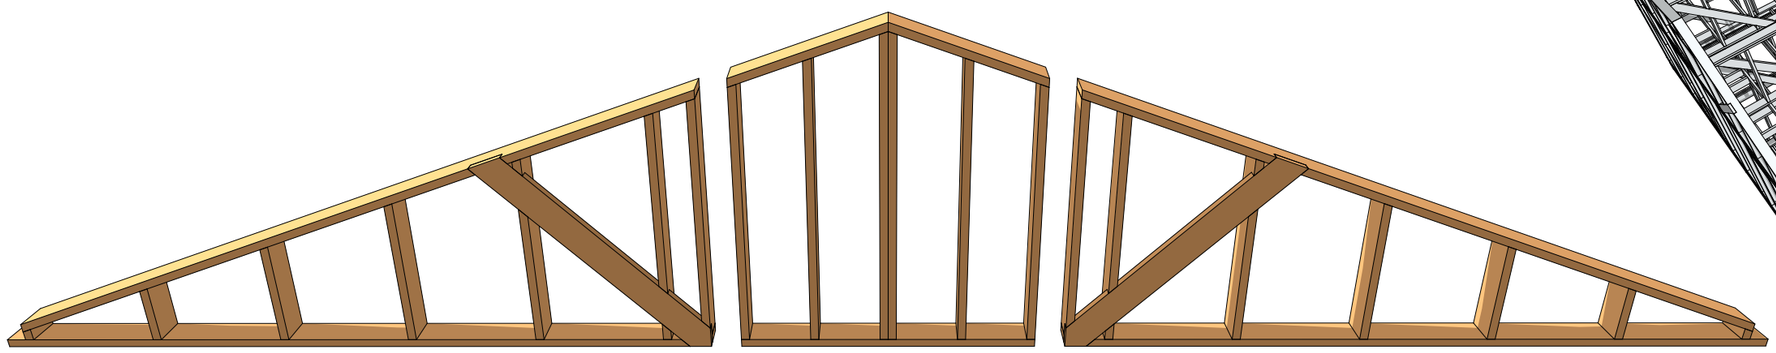

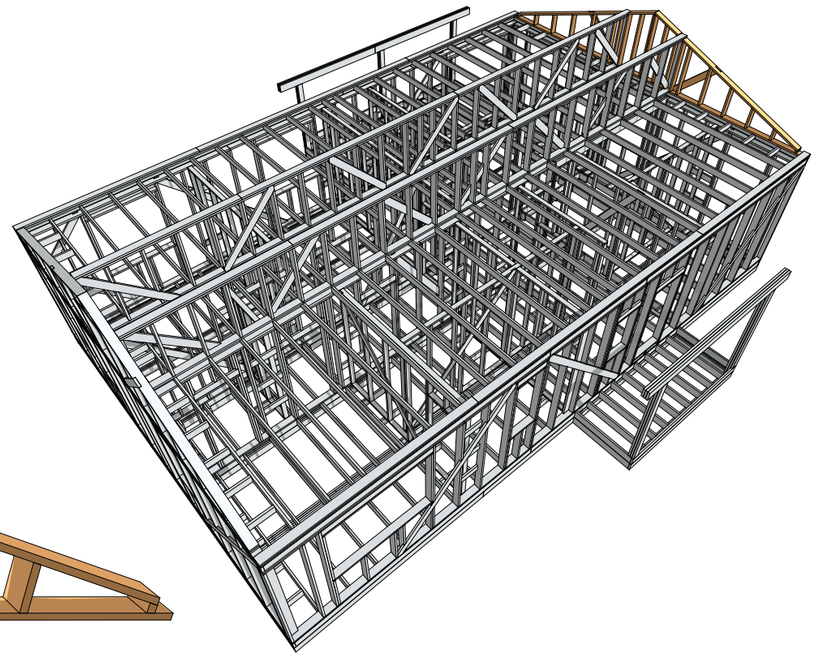


1				03/2026	Стена Ст-20	Лист 41
Изм.	Лист	№ докум.	Подпись	Дата		


Стена Ст-21

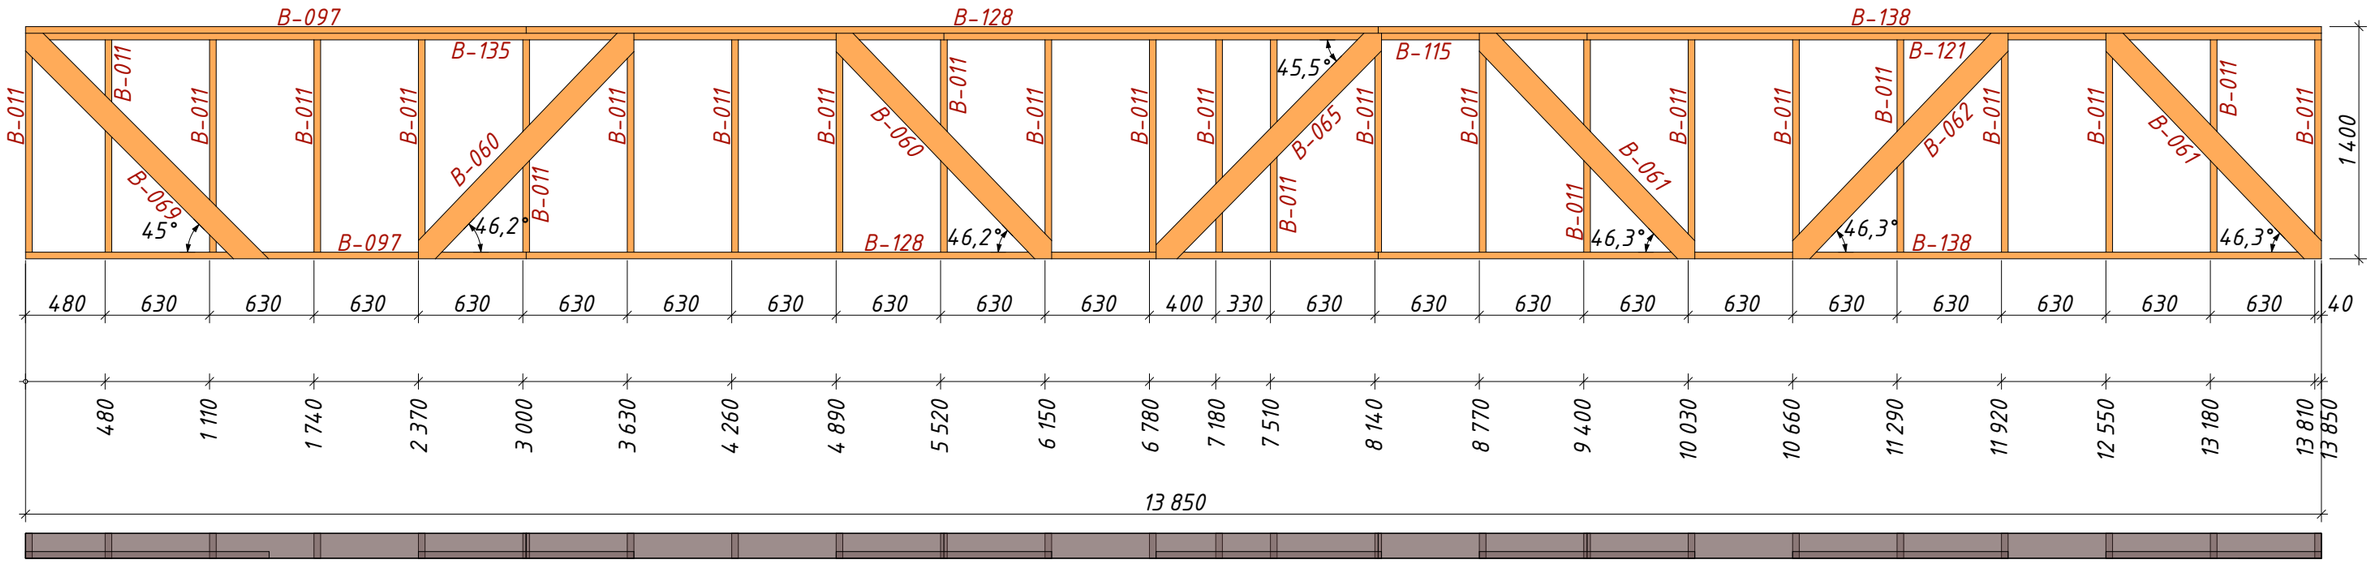

Ст-21▲

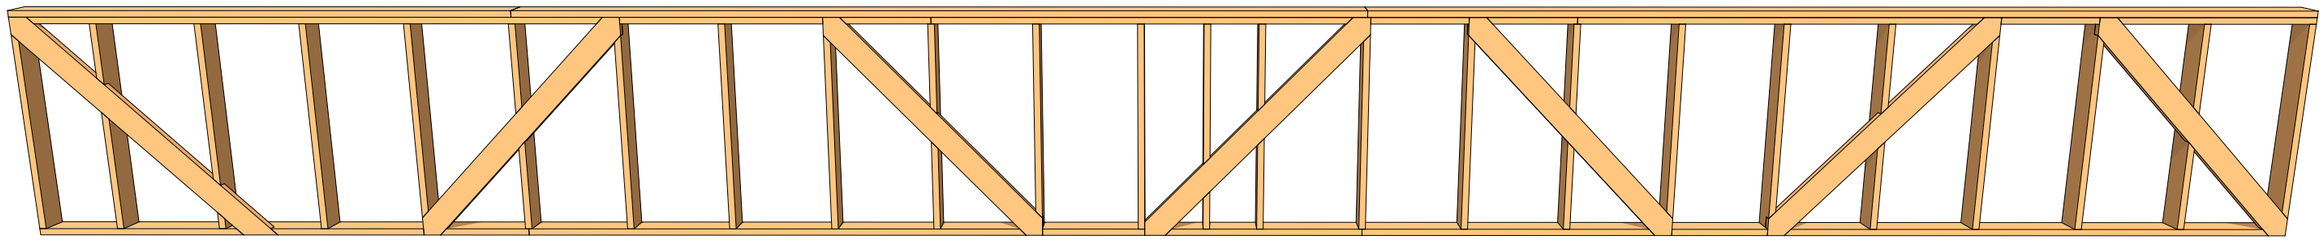



КД Спецификация деревянных элементов стены Ст-21				
Сечение	Марка	Длина	Кол-во	Объем
40х150				
	В-011	1 280	24	0,180
	В-060	2 035	2	0,022
	В-061	2 039	2	0,022
	В-062	2 039	1	0,011
	В-065	2 093	1	0,011
	В-069	2 228	1	0,011
	В-097	3 020	2	0,036
	В-115	3 880	1	0,023
	В-121	4 430	1	0,026
	В-128	5 140	2	0,061
	В-135	5 540	1	0,033
	В-138	5 690	2	0,068
				0,503 м³

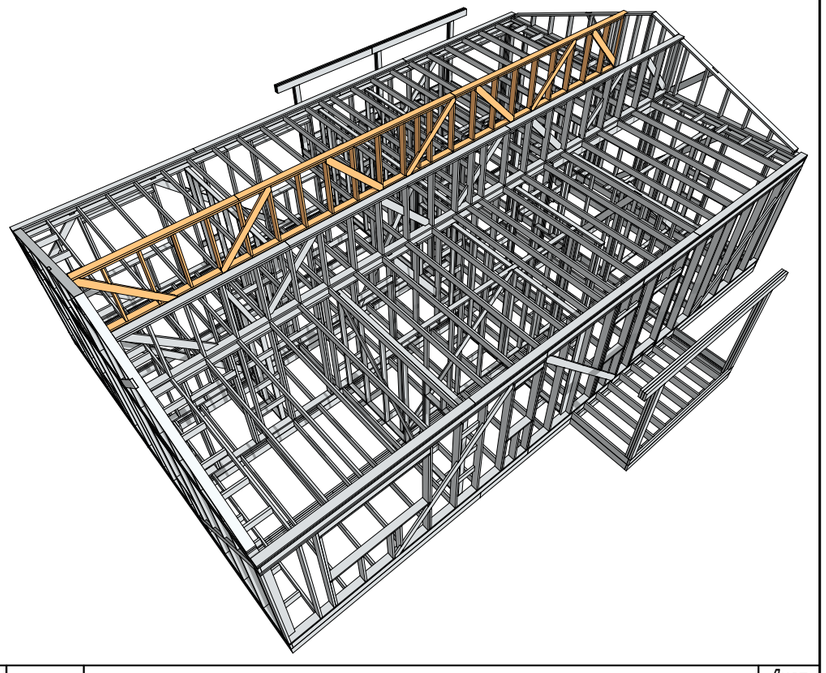


					Стена Ст-21	Лист
1				03/2026		42
Изм.	Лист	№ докум.	Подпись	Дата		

Стена Ст-22

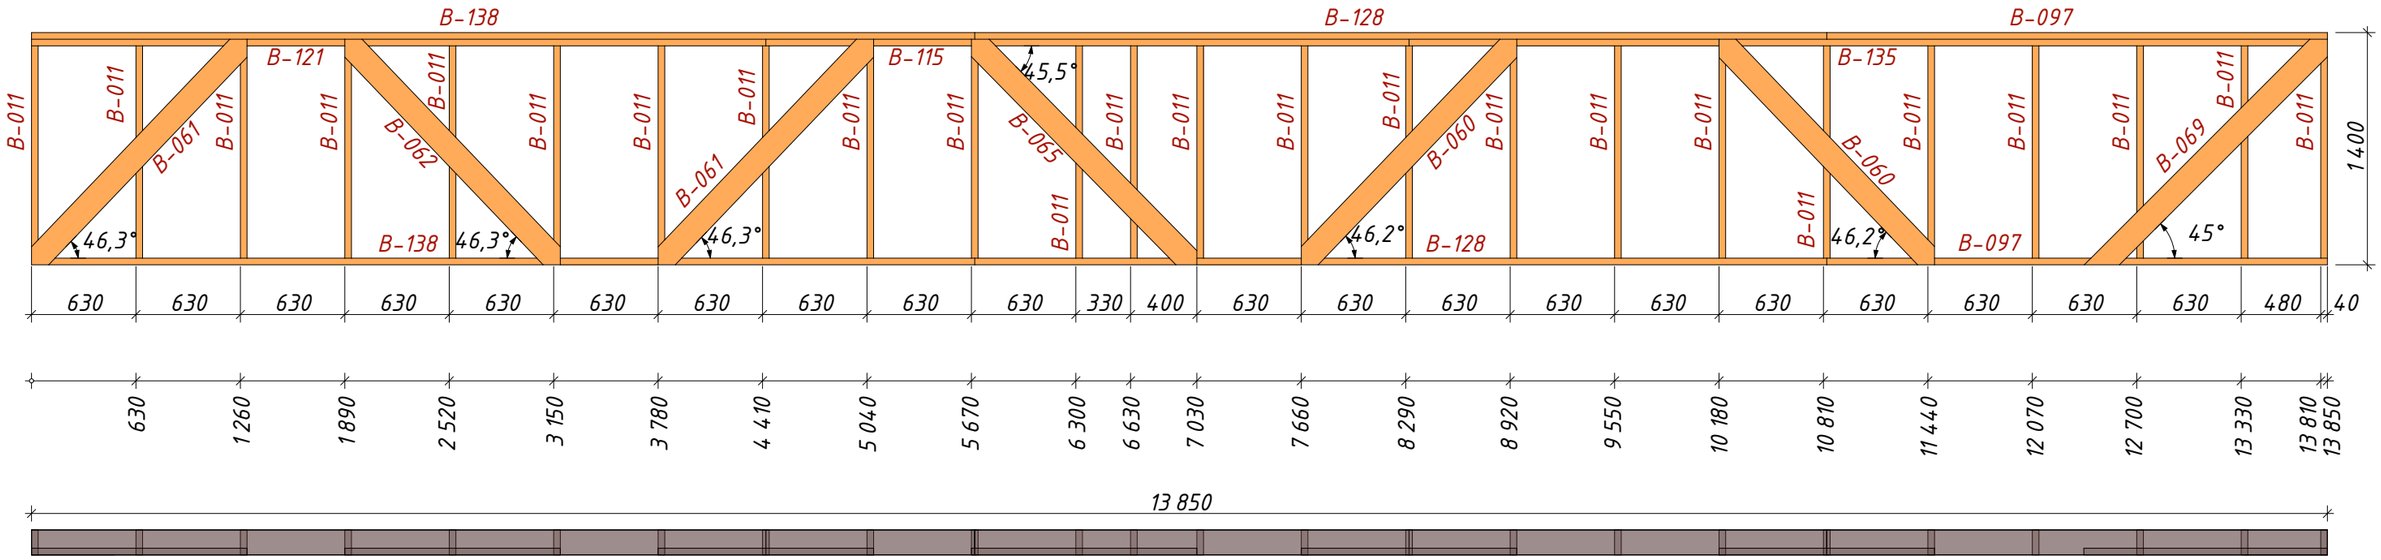

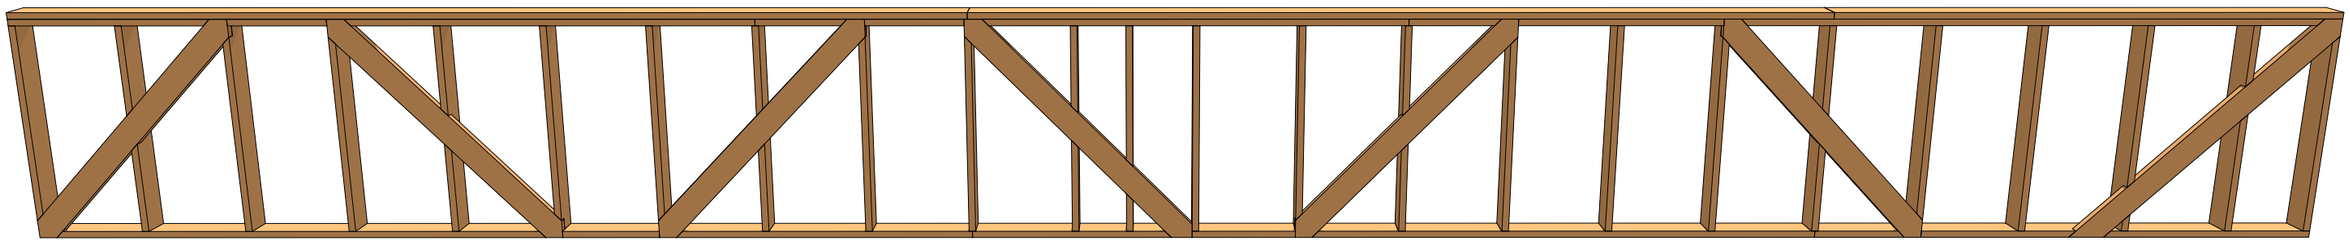


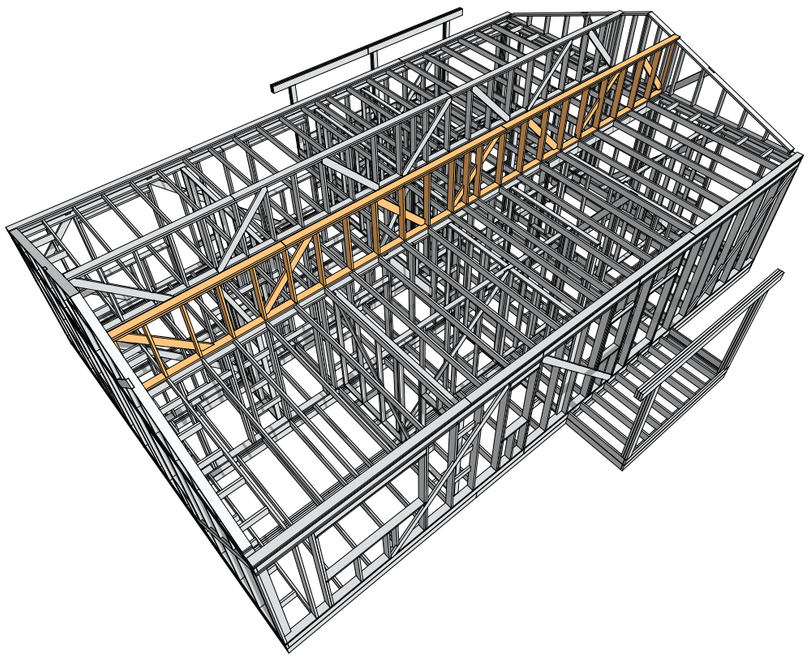

КД Спецификация деревянных элементов стены Ст-22				
Сечение	Марка	Длина	Кол-во	Объем
40x150				
	B-011	1 280	24	0,180
	B-060	2 035	2	0,022
	B-061	2 039	2	0,022
	B-062	2 039	1	0,011
	B-065	2 093	1	0,011
	B-069	2 228	1	0,011
	B-097	3 020	2	0,036
	B-115	3 880	1	0,023
	B-121	4 430	1	0,026
	B-128	5 140	2	0,061
	B-135	5 540	1	0,033
	B-138	5 690	2	0,068
				0,503 м³


						Лист
1				03/2026	Стена Ст-22	43
Изм.	Лист	№ докум.	Подпись	Дата		


Стены Ст-23/24

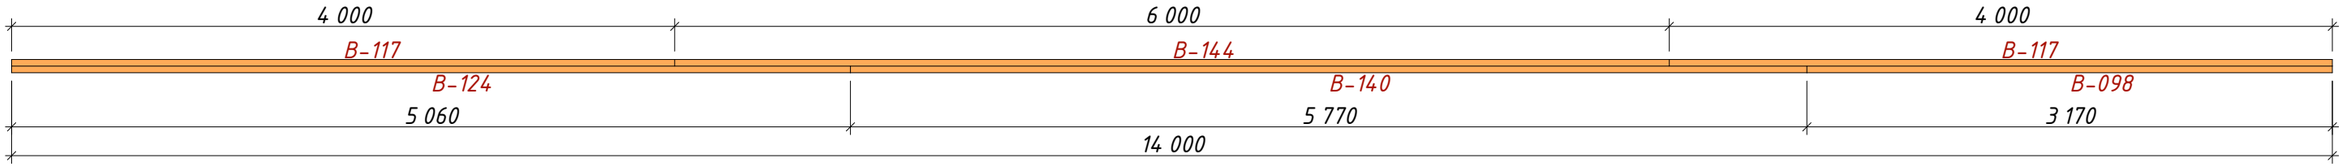

КД Спецификация деревянных элементов стены Ст-23

Сечение	Марка	Длина	Кол-во	Объем
40х150				
	В-098	3 170	1	0,019
	В-117	4 000	2	0,048
	В-124	5 060	1	0,030
	В-140	5 770	1	0,035
	В-144	6 000	1	0,036
				0,168 м^3

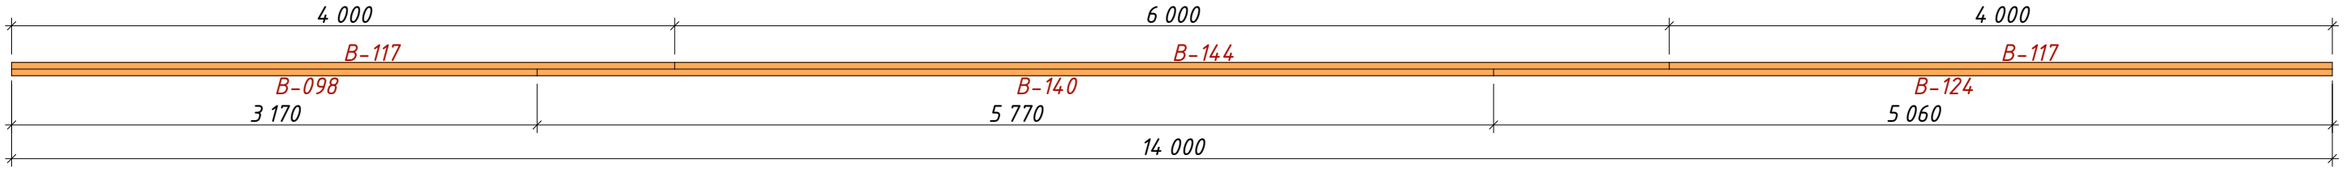

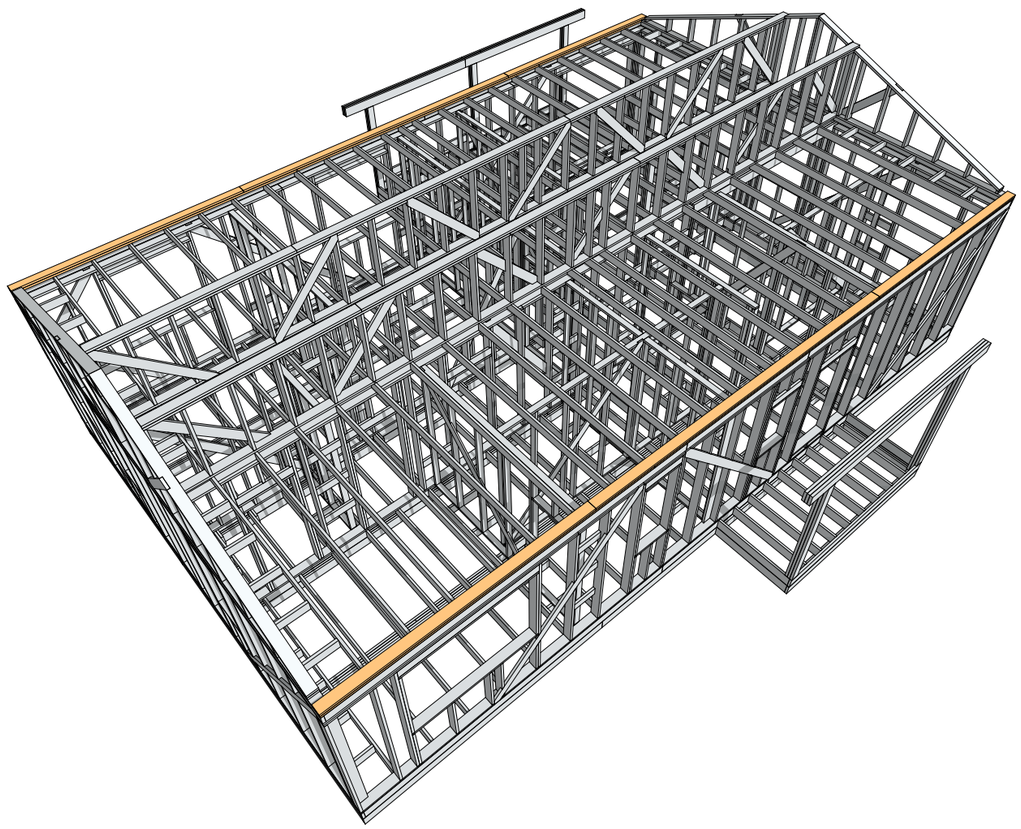



КД Спецификация деревянных элементов стены Ст-24

Сечение	Марка	Длина	Кол-во	Объем
40х150				
	В-098	3 170	1	0,019
	В-117	4 000	2	0,048
	В-124	5 060	1	0,030
	В-140	5 770	1	0,035
	В-144	6 000	1	0,036
				0,168 м^3

					Стены Ст-23/24	Лист
1				03/2026		44
Изм.	Лист	№ докум.	Подпись	Дата		

План стропильной системы

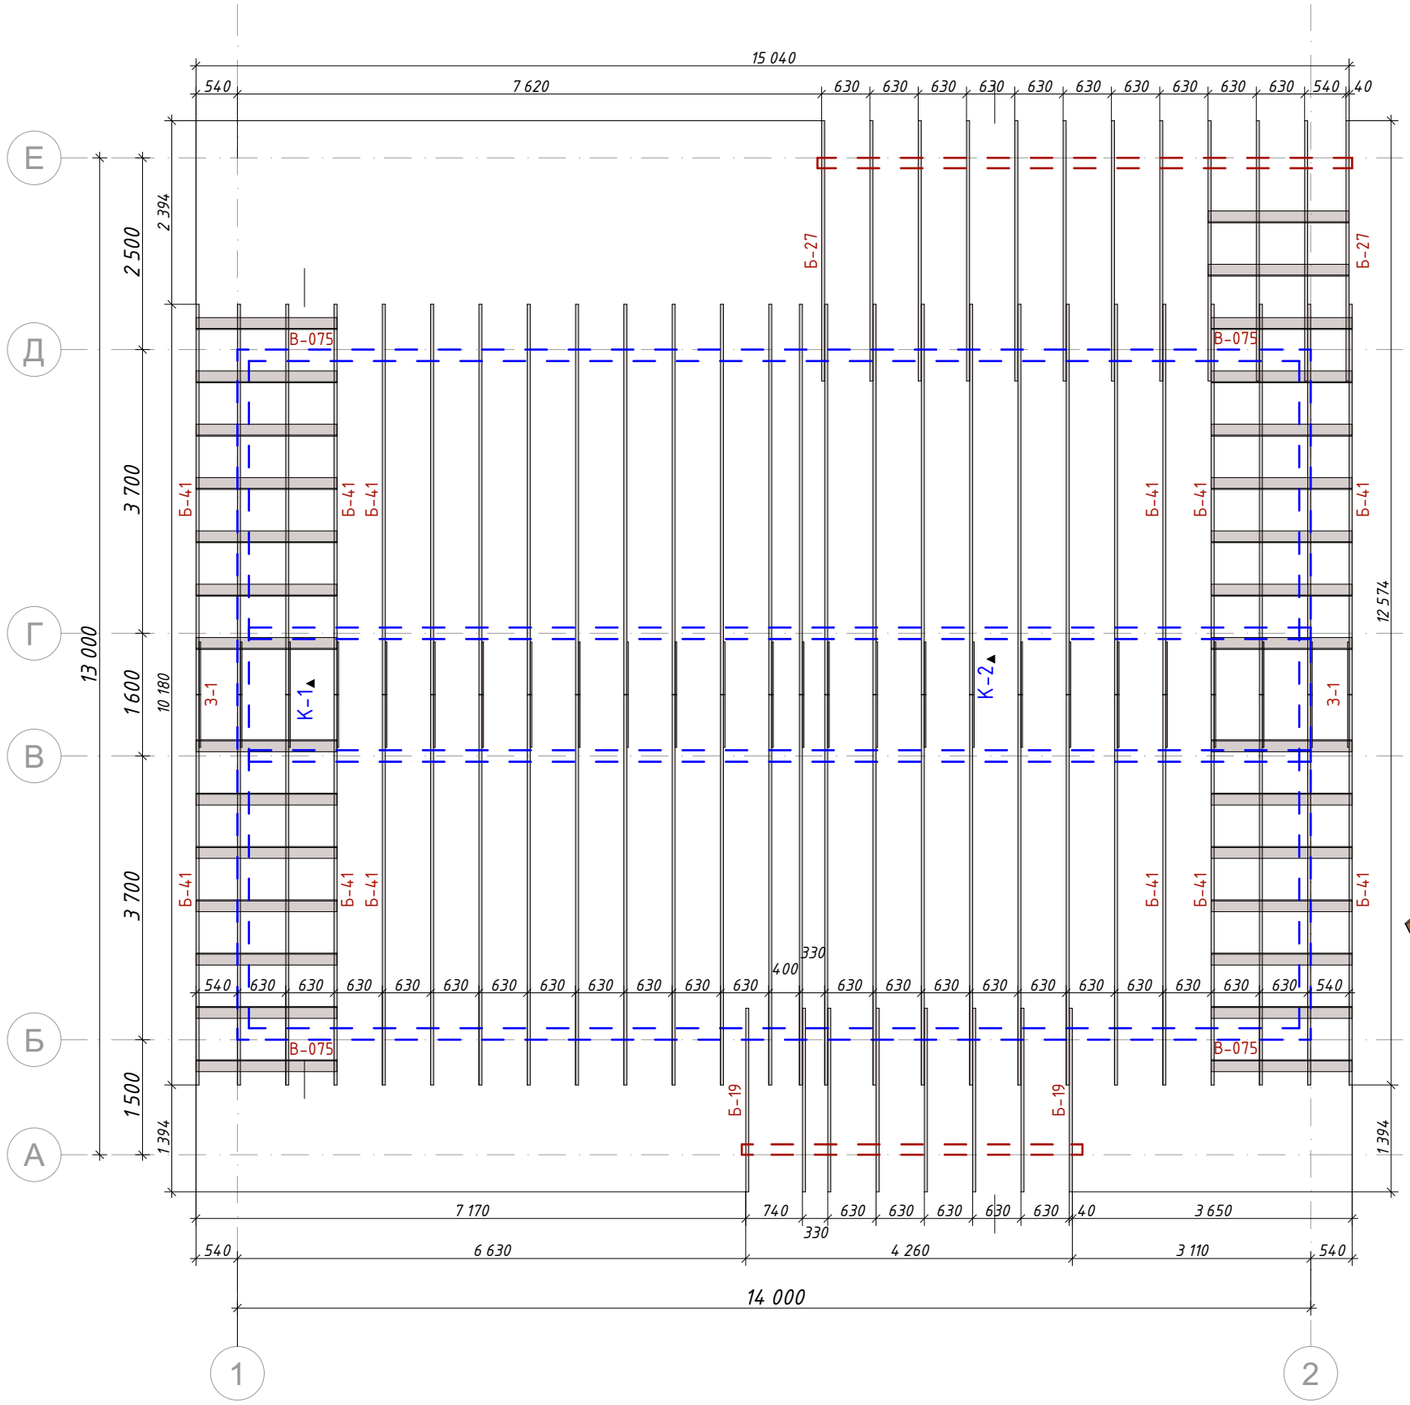

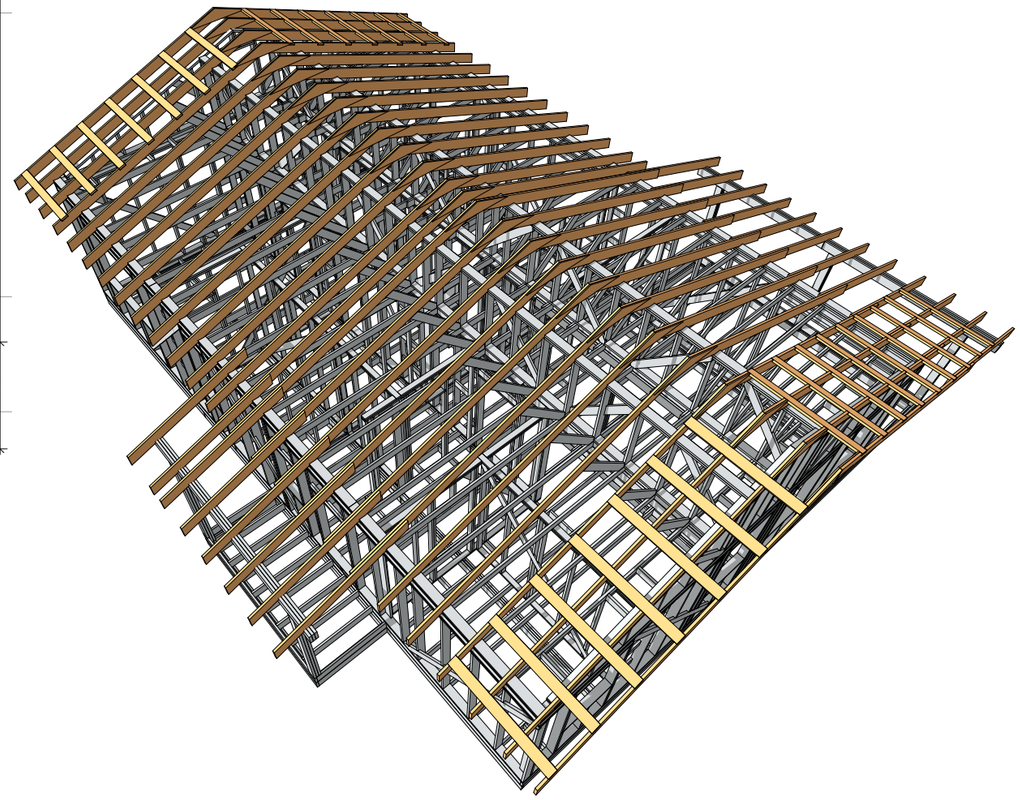

КД Спецификация деревянных элементов стропильной системы				
Сечение	Марка	Длина	Кол-во	Объем
40х150				
	В-075	1 840	30	0,331
				0,331 м³
40х200				
	Б-19	2 620	8	0,162
	Б-27	3 685	12	0,342
	Б-41	5 490	52	2,218
				2,723 м³
				3,054 м³


Примечание:

1. З-1 – накладки из фанеры толщиной 20 мм. Размеры (ВхШ) 1374х250 мм. Кол-во 26 шт.
2. Синими линиями обозначенынесущие подстропильные конструкции.
3. Красными линиями обозначены балки крыльца/террасы.


					План стропильной системы	Лист
1				03/2026		45
Изм.	Лист	№ докум.	Подпись	Дата		

Стропильная система: сечения

К-1 Сечение о/к 1

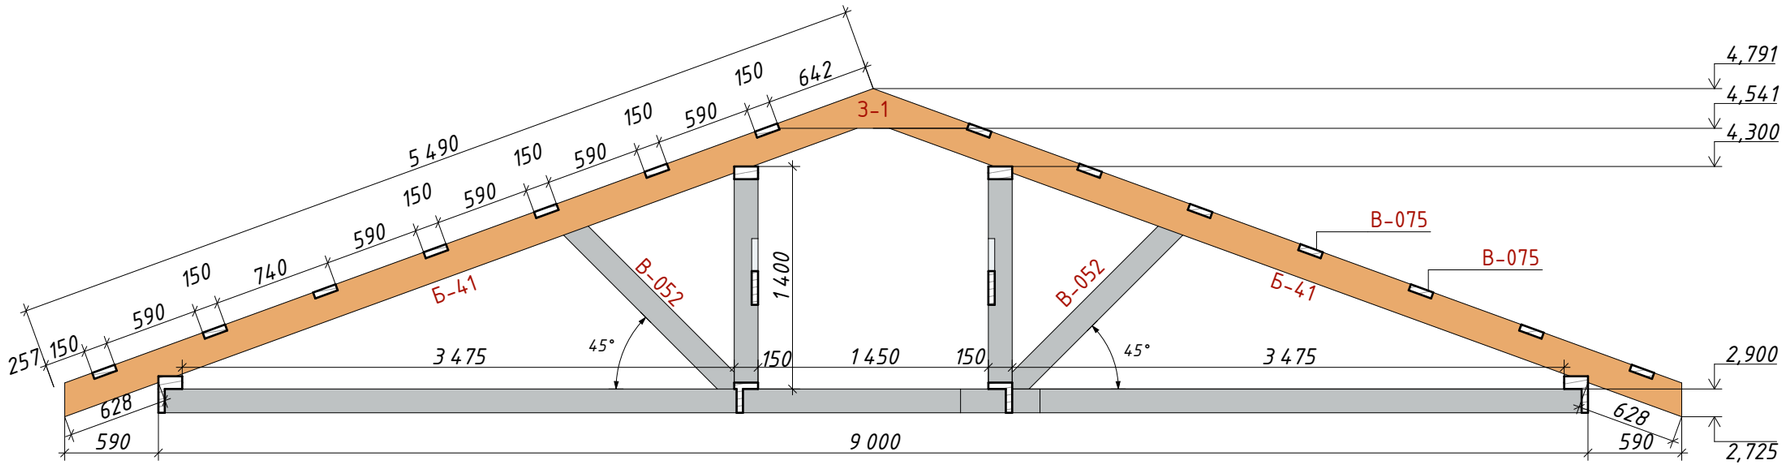

К-2 Сечение о/к 2

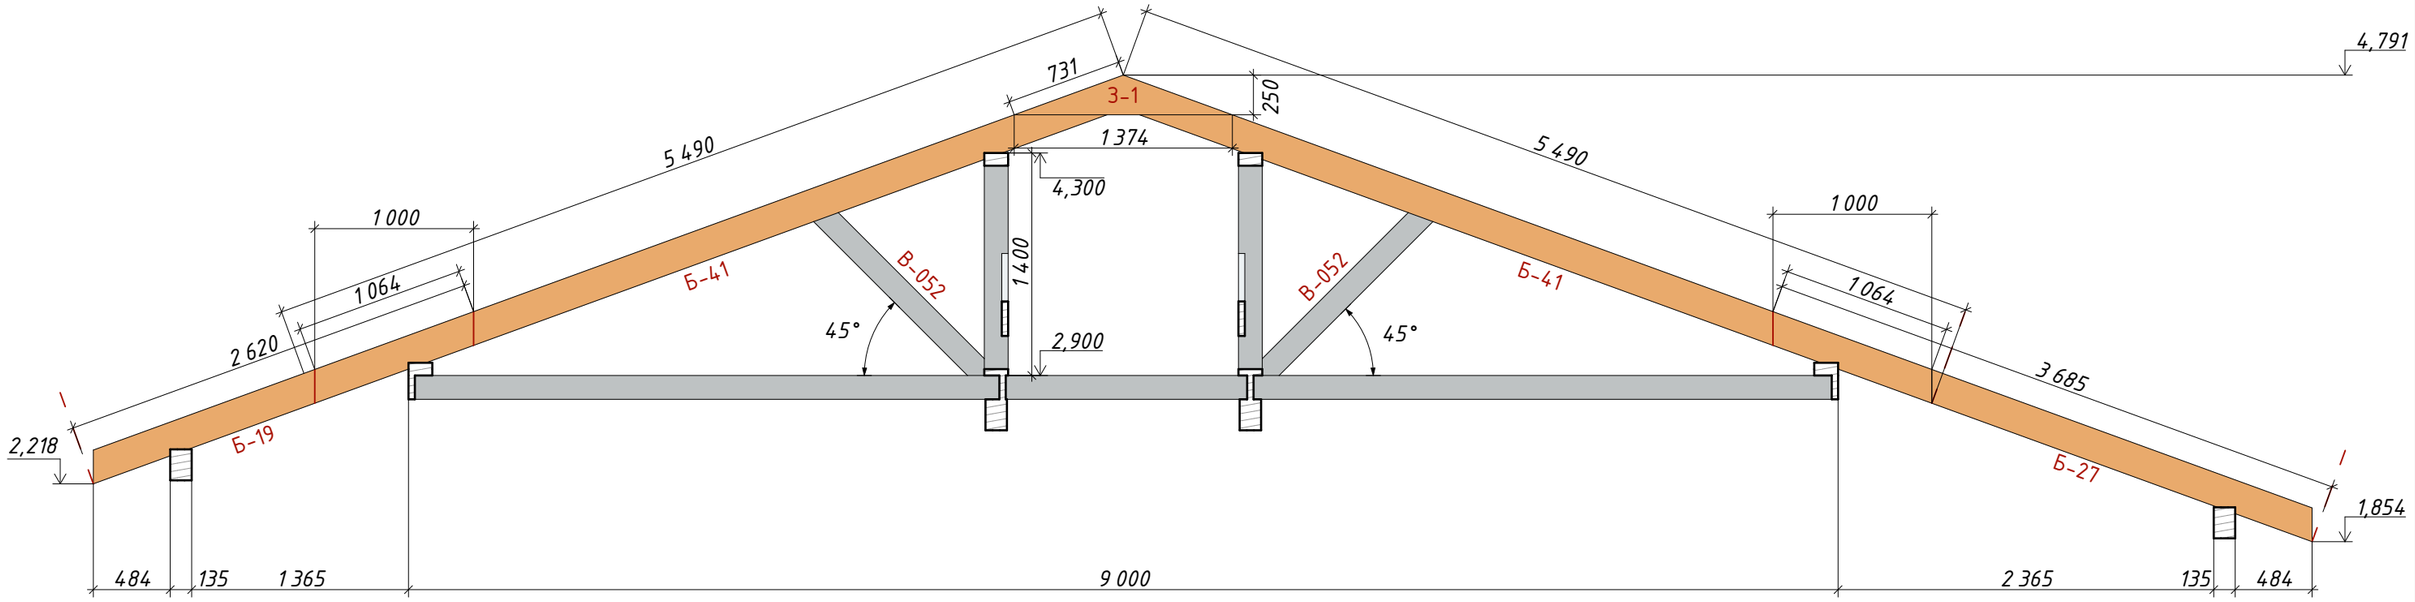

1				03/2026	Стропильная система: сечения	Лист 46
Изм.	Лист	№ докум.	Подпись	Дата		

Спецификация деревянных элементов силового каркаса

КД Спецификация деревянных элементов				
Сечение	Марка	Длина	Кол-во	Объем
25x150				
	М-01	3 821	1	0,013
	М-02	3 981	1	0,014
	М-03	4 169	1	0,015
	М-04	4 373	1	0,015
	М-05	4 374	3	0,045
				0,102 м³
40x100				
	К-01	560	12	0,027
	К-02	2 200	8	0,070
	К-03	2 800	76	0,844
	К-04	260	3	0,003
	К-05	645	1	0,003
	К-06	880	3	0,011
	К-07	1 280	1	0,005
	К-08	1 395	1	0,006
	К-09	1 450	4	0,023
	К-10	1 641	2	0,013
	К-11	1 734	2	0,014
	К-12	1 750	1	0,007
	К-13	1 791	2	0,014
	К-14	1 821	1	0,007
	К-15	1 884	1	0,008
	К-16	2 130	1	0,009
	К-17	2 386	2	0,019
	К-18	2 889	1	0,012
	К-19	3 300	2	0,026
	К-20	3 475	10	0,137
	К-21	3 550	1	0,014
	К-22	3 625	1	0,015
	К-23	3 775	2	0,030
	К-24	4 610	2	0,037
	К-25	5 375	1	0,021
				1,374 м³
40x150				
	В-001	59	4	0,001
	В-002	170	2	0,002
	В-003	289	4	0,007
	В-004	315	2	0,004
	В-005	518	4	0,012
	В-006	747	4	0,018
	В-007	977	4	0,023
	В-008	1 200	2	0,014
	В-009	1 206	4	0,027
	В-010	1 277	2	0,015
	В-011	1 280	48	0,359
	В-012	1 346	2	0,016

КД Спецификация деревянных элементов				
Сечение	Марка	Длина	Кол-во	Объем
	В-013	1 435	2	0,017
	В-014	1 471	2	0,018
	В-015	1 595	2	0,019
	В-016	85	3	0,002
	В-017	70	5	0,002
	В-018	100	3	0,002
	В-019	550	6	0,018
	В-020	560	21	0,066
	В-021	1 000	37	0,219
	В-022	1 170	2	0,014
	В-023	1 570	20	0,188
	В-024	2 070	2	0,025
	В-025	2 200	14	0,185
	В-026	2 500	2	0,030
	В-027	2 645	10	0,158
	В-028	2 800	111	1,848
	В-029	165	1	0,001
	В-030	175	2	0,002
	В-031	200	3	0,004
	В-032	306	1	0,002
	В-033	426	3	0,008
	В-034	500	22	0,066
	В-035	521	3	0,009
	В-036	525	3	0,009
	В-037	550	19	0,063
	В-038	590	78	0,276
	В-039	697	1	0,004
	В-040	720	4	0,017
	В-041	720	8	0,035
	В-042	786	2	0,009
	В-043	780	1	0,005
	В-044	780	1	0,005
	В-045	880	2	0,011
	В-046	880	4	0,021
	В-047	940	1	0,006
	В-048	940	2	0,011
	В-049	980	4	0,024
	В-050	980	4	0,024
	В-051	1 668	2	0,016
	В-052	1 671	42	0,346
	В-053	1 120	4	0,027
	В-054	1 120	8	0,054
	В-055	1 125	1	0,007
	В-056	1 190	1	0,007
	В-057	1 839	2	0,018
	В-058	1 845	1	0,010
	В-059	1 251	1	0,008

КД Спецификация деревянных элементов				
Сечение	Марка	Длина	Кол-во	Объем
	В-060	2 035	4	0,043
	В-061	2 039	4	0,043
	В-062	2 039	2	0,022
	В-063	1 314	1	0,008
	В-064	1 316	1	0,008
	В-065	2 093	2	0,022
	В-066	1 382	1	0,008
	В-067	1 425	2	0,017
	В-068	1 450	2	0,017
	В-069	2 228	2	0,023
	В-070	1 477	1	0,009
	В-071	1 620	2	0,019
	В-072	1 620	4	0,039
	В-073	2 672	1	0,014
	В-074	3 635	1	0,020
	В-075	1 840	30	0,331
	В-076	1 920	1	0,012
	В-077	3 692	1	0,020
	В-078	2 120	2	0,025
	В-079	2 120	2	0,025
	В-080	2 130	1	0,013
	В-081	2 341	2	0,028
	В-082	2 380	2	0,029
	В-083	2 380	2	0,029
	В-084	3 928	1	0,022
	В-085	2 415	1	0,014
	В-086	2 620	1	0,016
	В-087	4 071	1	0,023
	В-088	2 664	1	0,016
	В-089	4 058	1	0,023
	В-090	4 101	1	0,023
	В-091	2 723	1	0,016
	В-092	2 789	2	0,033
	В-093	4 177	2	0,047
	В-094	4 289	1	0,024
	В-095	4 376	2	0,048
	В-096	3 000	2	0,036
	В-097	3 020	4	0,071
	В-098	3 170	2	0,038
	В-099	3 190	2	0,038
	В-100	3 260	1	0,020
	В-101	3 300	1	0,020
	В-102	3 617	2	0,043
	В-103	3 463	2	0,041
	В-104	3 475	2	0,041
	В-105	3 481	1	0,021
	В-106	3 482	2	0,042

КД Спецификация деревянных элементов				
Сечение	Марка	Длина	Кол-во	Объем
	В-107	3 530	1	0,021
	В-108	3 543	1	0,021
	В-109	3 612	1	0,022
	В-110	3 625	2	0,043
	В-111	3 660	22	0,483
	В-112	3 719	1	0,022
	В-113	3 768	1	0,023
	В-114	3 856	1	0,023
	В-115	3 880	2	0,046
	В-116	3 943	1	0,024
	В-117	4 000	4	0,096
	В-118	4 227	1	0,025
	В-119	4 548	2	0,054
	В-120	4 280	1	0,025
	В-121	4 430	2	0,052
	В-122	4 660	1	0,028
	В-123	4 704	1	0,028
	В-124	5 060	2	0,061
	В-125	5 110	1	0,031
	В-126	5 116	1	0,031
	В-127	5 120	1	0,031
	В-128	5 140	4	0,123
	В-129	5 260	22	0,694
	В-130	5 290	1	0,032
	В-131	5 354	1	0,032
	В-132	5 440	2	0,065
	В-133	5 494	1	0,033
	В-134	5 510	2	0,066
	В-135	5 540	2	0,065
	В-136	5 621	1	0,034
	В-137	5 650	2	0,068
	В-138	5 690	4	0,135
	В-139	5 760	1	0,034
	В-140	5 770	2	0,069
	В-141	5 916	1	0,035
	В-142	5 978	1	0,036
	В-143	6 000	4	0,144
	В-144	6 000	3	0,108
				8,913 м³
40x200				
	Б-01	360	9	0,026
	Б-02	500	22	0,088
	Б-03	550	21	0,092
	Б-04	590	86	0,406
	Б-05	1 420	2	0,023
	Б-06	1 460	10	0,117
	Б-07	1 480	2	0,024

КД Спецификация деревянных элементов				
Сечение	Марка	Длина	Кол-во	Объем
	Б-08	1 500	4	0,048
	Б-09	1 560	2	0,025
	Б-10	1 607	1	0,013
	Б-11	1 693	4	0,054
	Б-12	1 708	4	0,055
	Б-13	1 773	4	0,057
	Б-14	1 788	4	0,057
	Б-15	1 813	1	0,015
	Б-16	1 920	1	0,015
	Б-17	2 190	6	0,105
	Б-18	2 380	1	0,019
	Б-19	2 620	8	0,162
	Б-20	2 420	1	0,019
	Б-21	2 460	15	0,295
	Б-22	2 500	2	0,040
	Б-23	2 620	1	0,021
	Б-24	2 629	1	0,021
	Б-25	3 000	1	0,024
	Б-26	3 335	2	0,053
	Б-27	3 685	12	0,342
	Б-28	3 412	2	0,055
	Б-29	3 415	2	0,055
	Б-30	3 447	4	0,110
	Б-31	3 495	1	0,028
	Б-32	3 575	2	0,057
	Б-33	3 660	23	0,673
	Б-34	3 722	1	0,030
	Б-35	3 974	4	0,127
	Б-36	4 304	10	0,344
	Б-37	4 309	15	0,517
	Б-38	4 348	1	0,035
	Б-39	4 384	2	0,070
	Б-40	4 823	1	0,039
	Б-41	5 490	52	2,218
	Б-42	5 226	10	0,418
	Б-43	5 260	24	1,010
	Б-44	5 460	1	0,044
	Б-45	5 650	2	0,090
	Б-46	5 654	1	0,045
	Б-47	5 694	1	0,046
	Б-48	5 734	1	0,046
	Б-49	5 774	1	0,046
	Б-50	5 814	1	0,047
	Б-51	5 894	2	0,094
	Б-52	6 000	4	0,192
	З-1	1 374	26	0,089
				8,741 м³

КД Спецификация деревянных элементов				
Сечение	Марка	Длина	Кол-во	Объем
45x145				
	Л-1	2 245	9	0,127
	Л-2	2 610	6	0,098
	Л-3	2 725	3	0,053
				0,279 м³
45x195				
	Т-1	3 234	2	0,057
	Т-2	3 240	1	0,028
	Т-3	3 734	1	0,033
	Т-4	3 740	2	0,066
	Т-5	4 147	3	0,109
	Т-6	4 443	3	0,117
	Т-7	5 435	3	0,143
				0,553 м³
				19,962 м